


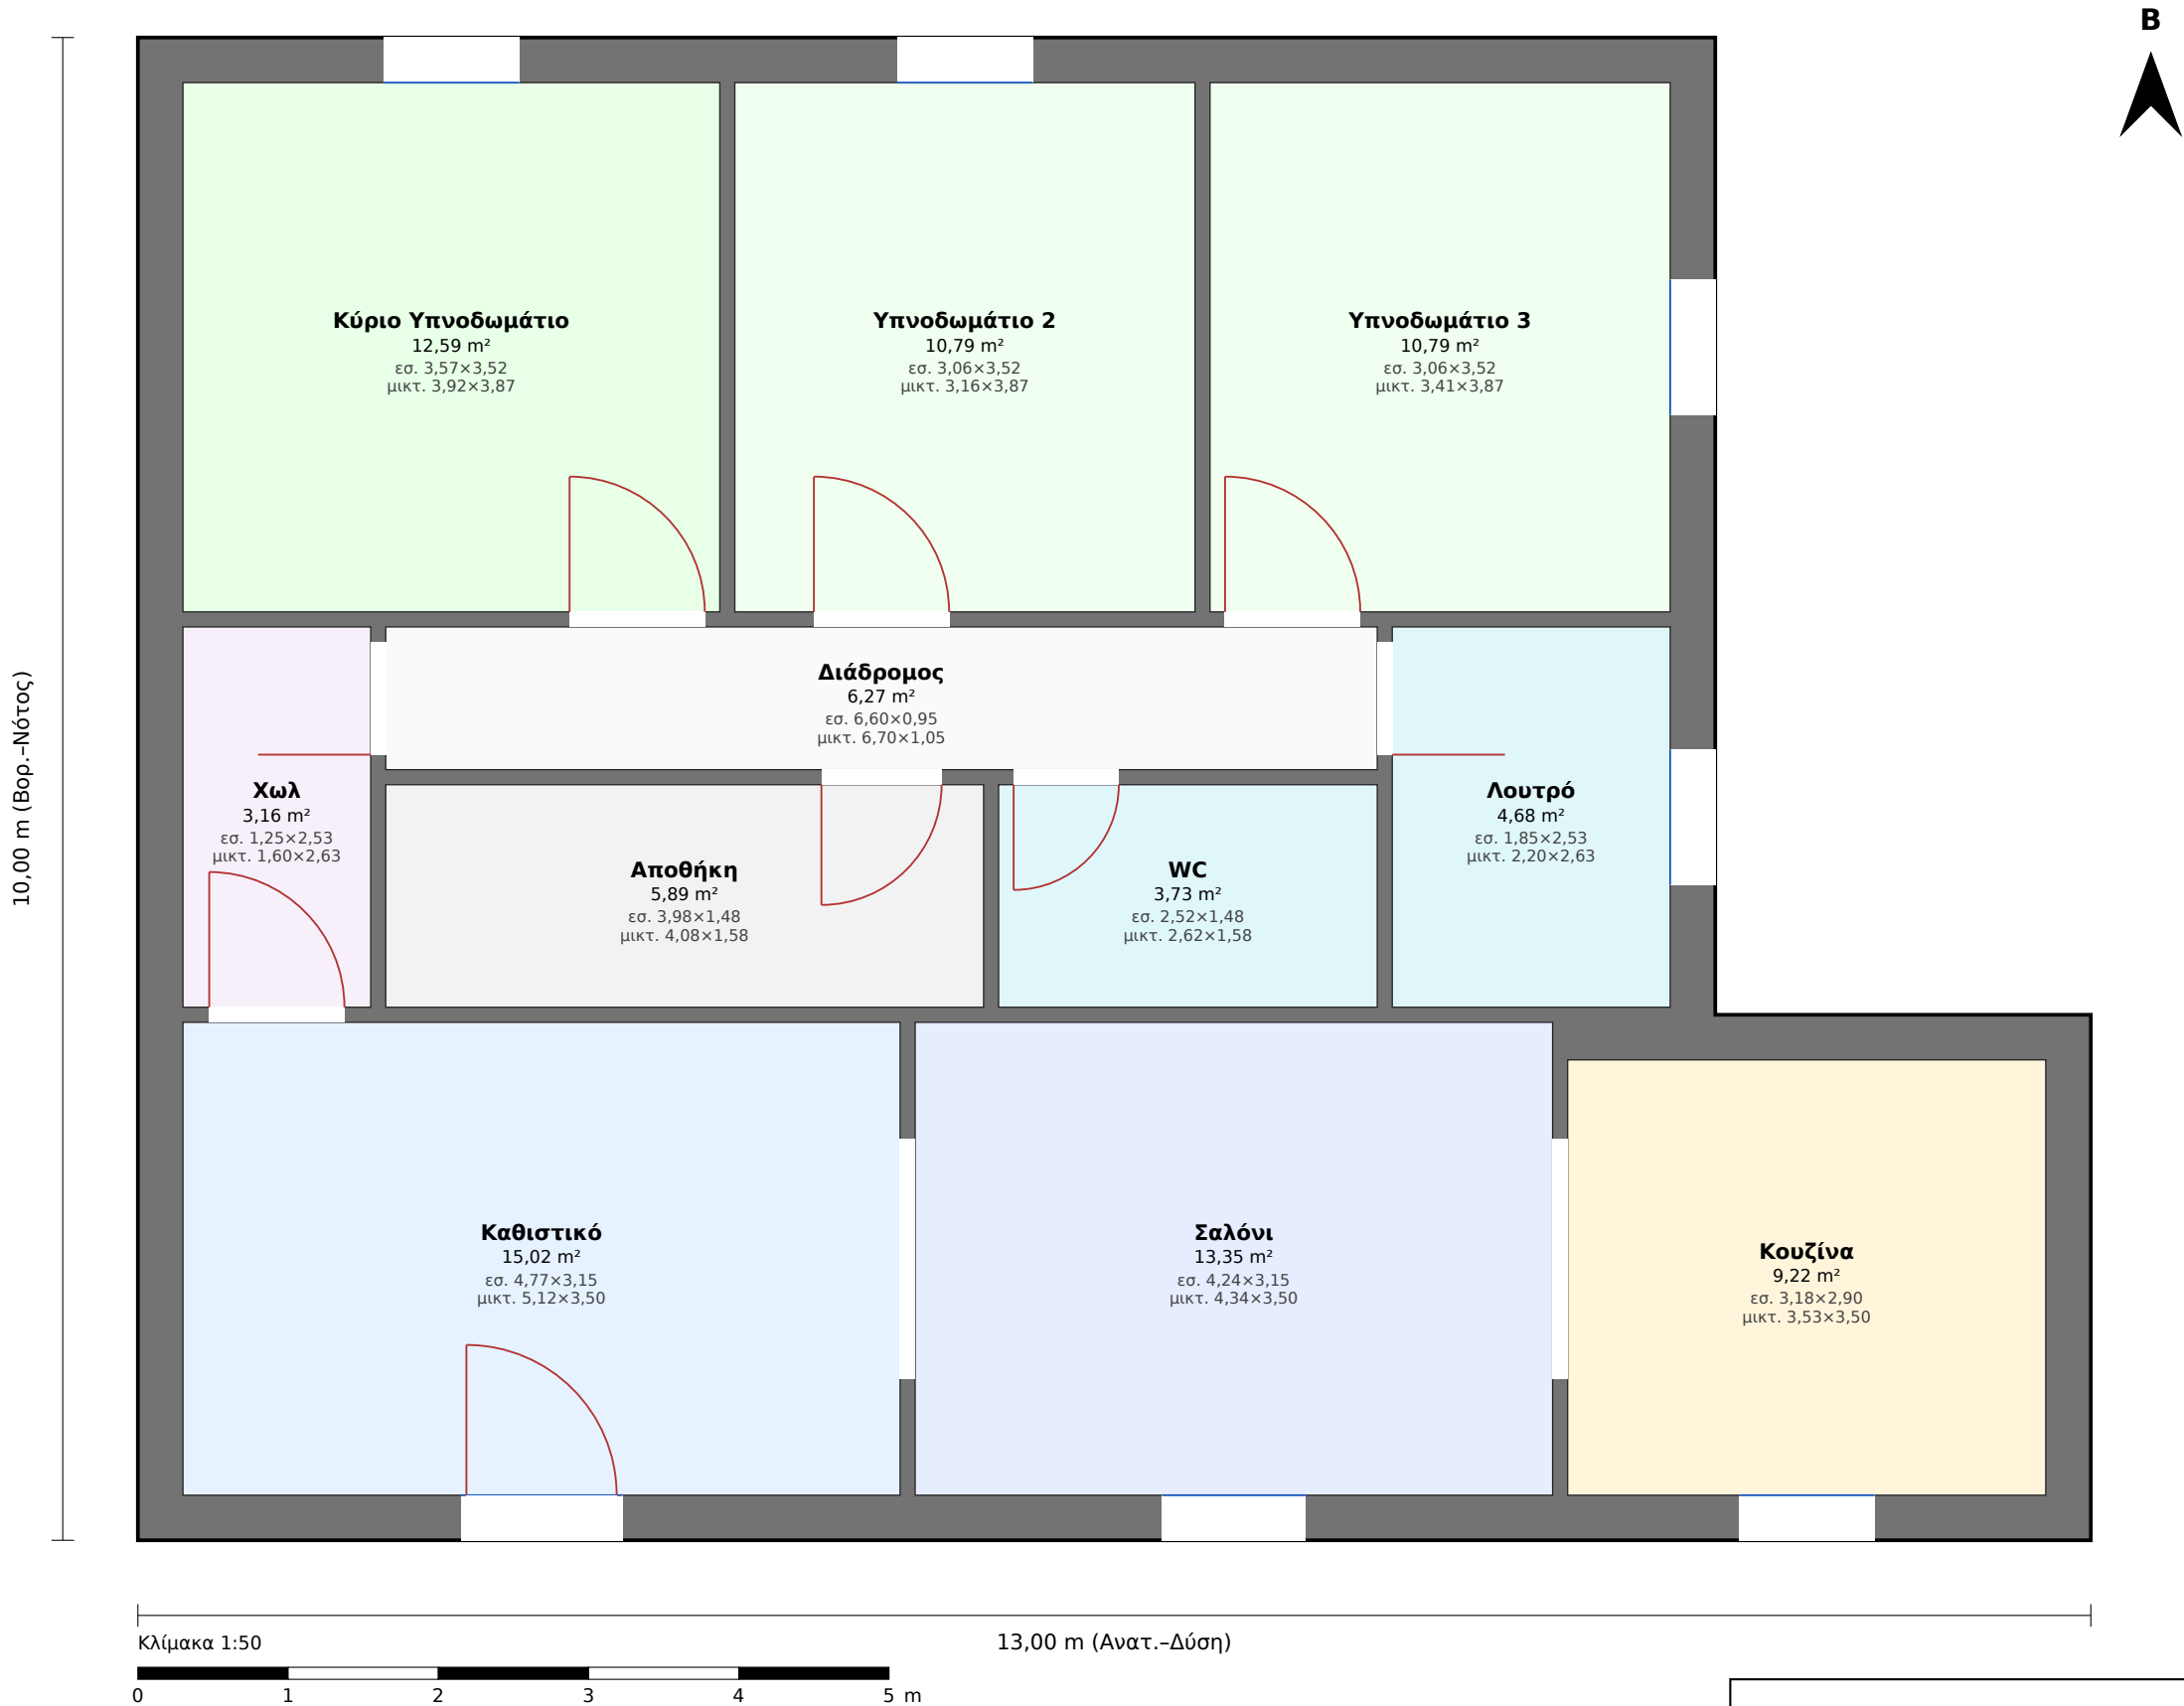

Τεχνικό Γραφείο Μελετών — Γεωργακόπουλος Χρ. / Φουντάς Αθ.
Έργο: Μονοκατοικία Αμαλιάδας
Πρόταση 1 — Ισόγειο
Κλίμακα 1:50 · Μικτό εμβ.: 113,74 m²
Είσοδος: Νότος · Αμαλιάδα, Π.Ε. Ηλείας
Ημερομηνία: 16.08.2026 · Σχεδ.: Γεωργακόπουλος Χρ. (AM TEE 101893)

Μονοκατοικία Αμαλιάδας — Πρόταση 1: Πίνακες χώρων & έλεγχοι

Διαστάσεις: «καθαρές» = εσωτερικές ελεύθερες · «μικτές» = με τοίχους (εξωτ. πλήρες πάχος, εσωτ. μισό). Βορράς: επάνω.


■ Ισόγειο (μικτό 113,74 m², καθαρό 95,50 m²)

#	Χώρος	Καθ. εμβ. (m²)	Καθ. Α×Β (m)	Μικτές Α×Β (m)	Ζώνη
1	Καθιστικό	15,02	4,77×3,15	5,12×3,50	κύρια
2	Σαλόνι	13,35	4,24×3,15	4,34×3,50	κύρια
3	Κουζίνα	9,22	3,18×2,90	3,53×3,50	κύρια
4	Κύριο Υπνοδωμάτιο	12,59	3,57×3,52	3,92×3,87	κύρια
5	Υπνοδωμάτιο 2	10,79	3,06×3,52	3,16×3,87	κύρια
6	Υπνοδωμάτιο 3	10,79	3,06×3,52	3,41×3,87	κύρια
7	Χωλ	3,16	1,25×2,53	1,60×2,63	βοηθ.
8	Αποθήκη	5,89	3,98×1,48	4,08×1,58	βοηθ.
9	WC	3,73	2,52×1,48	2,62×1,58	βοηθ.
10	Λουτρό	4,68	1,85×2,53	2,20×2,63	βοηθ.
11	Διάδρομος	6,27	6,60×0,95	6,70×1,05	βοηθ.

Έλεγχος φωτισμού & αερισμού (Κ.Κ. αρ. 20 §5.1.2 / αρ. 21 §5.2)

Χώρος	Εμβ.	Φως≥10%	Υαλοπ.	Αερ.≥5%	Ανοιγ.	Φως	Αερ.
Καθιστικό	15,0	1,50	1,50	0,75	0,75	✓	✓
Σαλόνι	13,4	1,34	1,34	0,67	0,67	✓	✓
Κουζίνα	9,2	0,92	1,26	0,46	0,63	✓	✓
Κύριο Υπνοδωμάτιο	12,6	1,26	1,26	0,63	0,63	✓	✓
Υπνοδωμάτιο 2	10,8	1,08	1,26	0,54	0,63	✓	✓
Υπνοδωμάτιο 3	10,8	1,08	1,26	0,54	0,63	✓	✓
Χωλ	3,2	0,32	0,00	0,16	0,00	✓	✓
Αποθήκη	5,9	0,59	0,00	0,29	0,00	✓	✓
WC	3,7	0,37	0,00	0,19	0,00	✓	✓
Λουτρό	4,7	0,47	1,26	0,23	0,63	✓	✓

→ Όλοι οι χώροι κύριας χρήσης πληρούν φωτισμό ≥10% & αερισμό ≥5%.

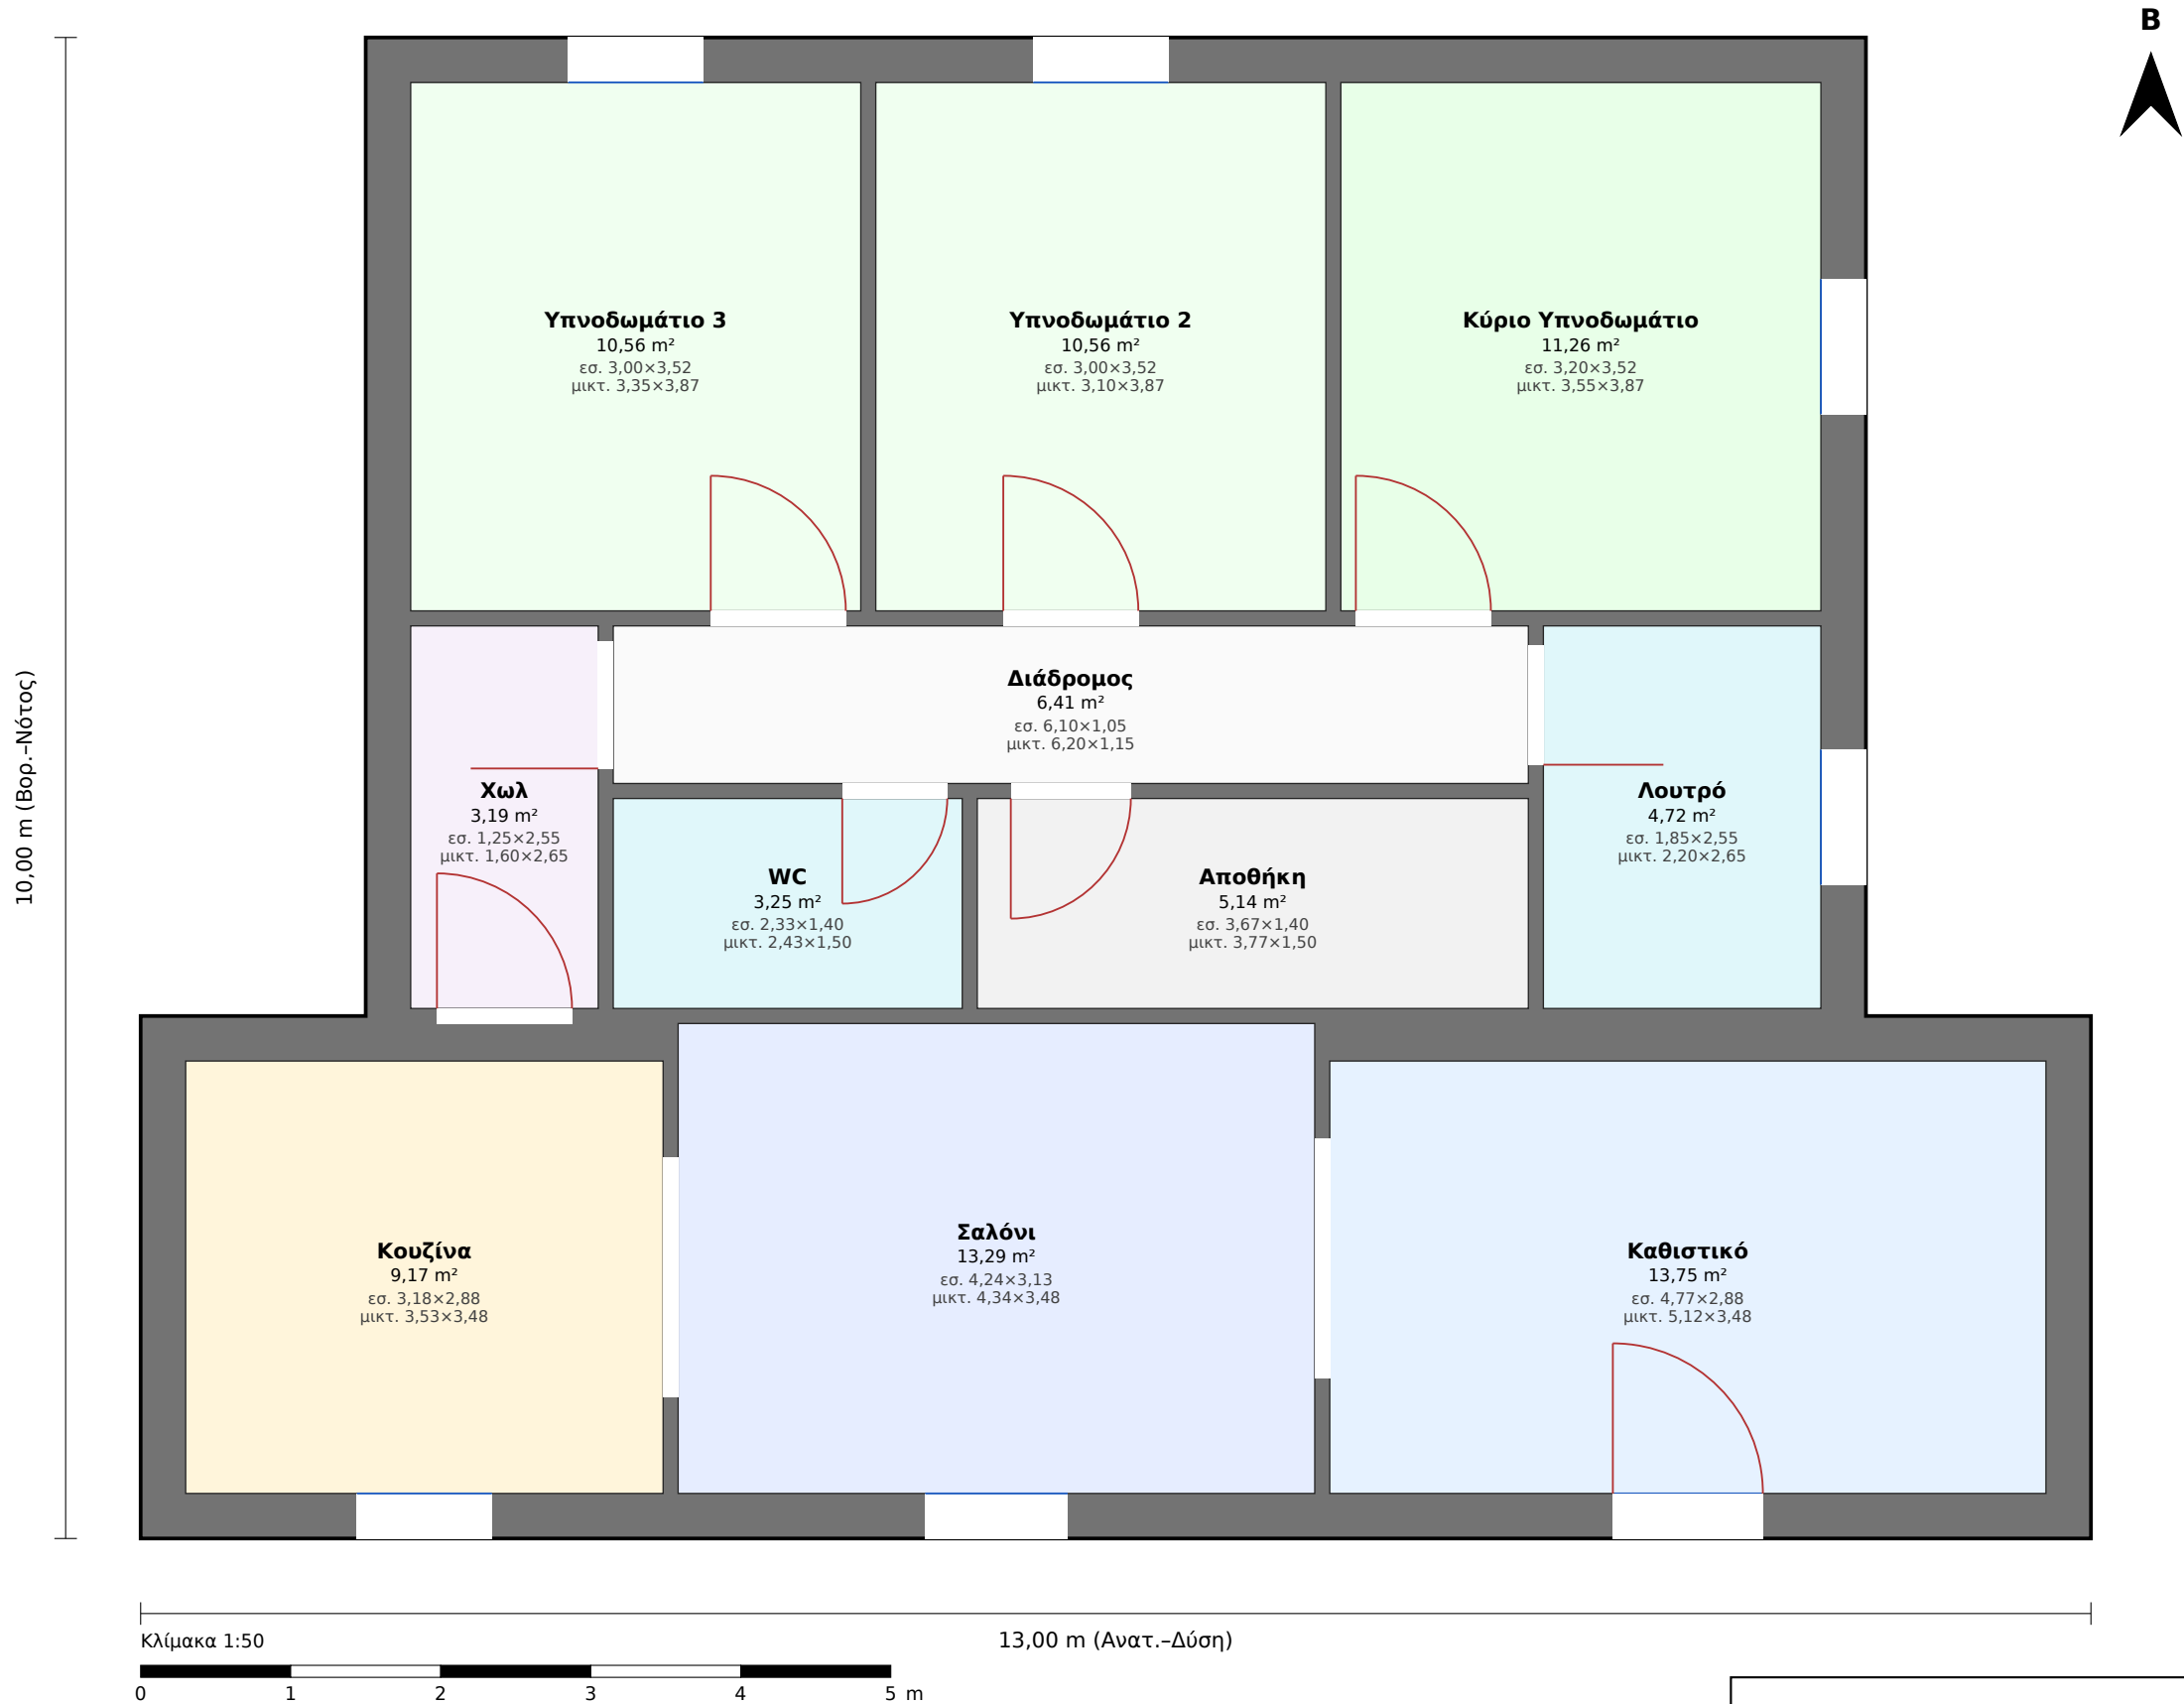

Τεχνικό Γραφείο Μελετών — Γεωργακόπουλος Χρ. / Φουντάς Αθ.
Έργο: Μονοκατοικία Αμαλιάδας
Πρόταση 2 — Ισόγειο
Κλίμακα 1:50 · Μικτό εμβ.: 110,44 m²
Είσοδος: Νότος · Αμαλιάδα, Π.Ε. Ηλείας
Ημερομηνία: 16.08.2026 · Σχεδ.: Γεωργακόπουλος Χρ. (AM TEE 101893)

Μονοκατοικία Αμαλιάδας — Πρόταση 2: Πίνακες χώρων & έλεγχοι

Διαστάσεις: «καθαρές» = εσωτερικές ελεύθερες · «μικτές» = με τοίχους (εξωτ. πλήρες πάχος, εσωτ. μισό). Βορράς: επάνω.


■ **Ισόγειο (μικτό 110,44 m², καθαρό 91,29 m²)**

#	Χώρος	Καθ. εμβ. (m²)	Καθ. Α×Β (m)	Μικτές Α×Β (m)	Ζώνη
1	Κουζίνα	9,17	3,18×2,88	3,53×3,48	κύρια
2	Σαλόνι	13,29	4,24×3,13	4,34×3,48	κύρια
3	Καθιστικό	13,75	4,77×2,88	5,12×3,48	κύρια
4	Υπνοδωμάτιο 3	10,56	3,00×3,52	3,35×3,87	κύρια
5	Υπνοδωμάτιο 2	10,56	3,00×3,52	3,10×3,87	κύρια
6	Κύριο Υπνοδωμάτιο	11,26	3,20×3,52	3,55×3,87	κύρια
7	Χωλ	3,19	1,25×2,55	1,60×2,65	βοηθ.
8	WC	3,25	2,33×1,40	2,43×1,50	βοηθ.
9	Αποθήκη	5,14	3,67×1,40	3,77×1,50	βοηθ.
10	Λουτρό	4,72	1,85×2,55	2,20×2,65	βοηθ.
11	Διάδρομος	6,41	6,10×1,05	6,20×1,15	βοηθ.

Έλεγχος φωτισμού & αερισμού (Κ.Κ. αρ. 20 §5.1.2 / αρ. 21 §5.2)

Χώρος	Εμβ.	Φως≥10%	Υαλοπ.	Αερ.≥5%	Ανοιγ.	Φως	Αερ.
Κουζίνα	9,2	0,92	1,26	0,46	0,63	✓	✓
Σαλόνι	13,3	1,33	1,33	0,66	0,66	✓	✓
Καθιστικό	13,8	1,38	1,38	0,69	0,69	✓	✓
Υπνοδωμάτιο 3	10,6	1,06	1,26	0,53	0,63	✓	✓
Υπνοδωμάτιο 2	10,6	1,06	1,26	0,53	0,63	✓	✓
Κύριο Υπνοδωμάτιο	11,3	1,13	1,26	0,56	0,63	✓	✓
Χωλ	3,2	0,32	0,00	0,16	0,00	✓	✓
WC	3,3	0,33	0,00	0,16	0,00	✓	✓
Αποθήκη	5,1	0,51	0,00	0,26	0,00	✓	✓
Λουτρό	4,7	0,47	1,26	0,24	0,63	✓	✓

→ Όλοι οι χώροι κύριας χρήσης πληρούν φωτισμό ≥10% & αερισμό ≥5%.

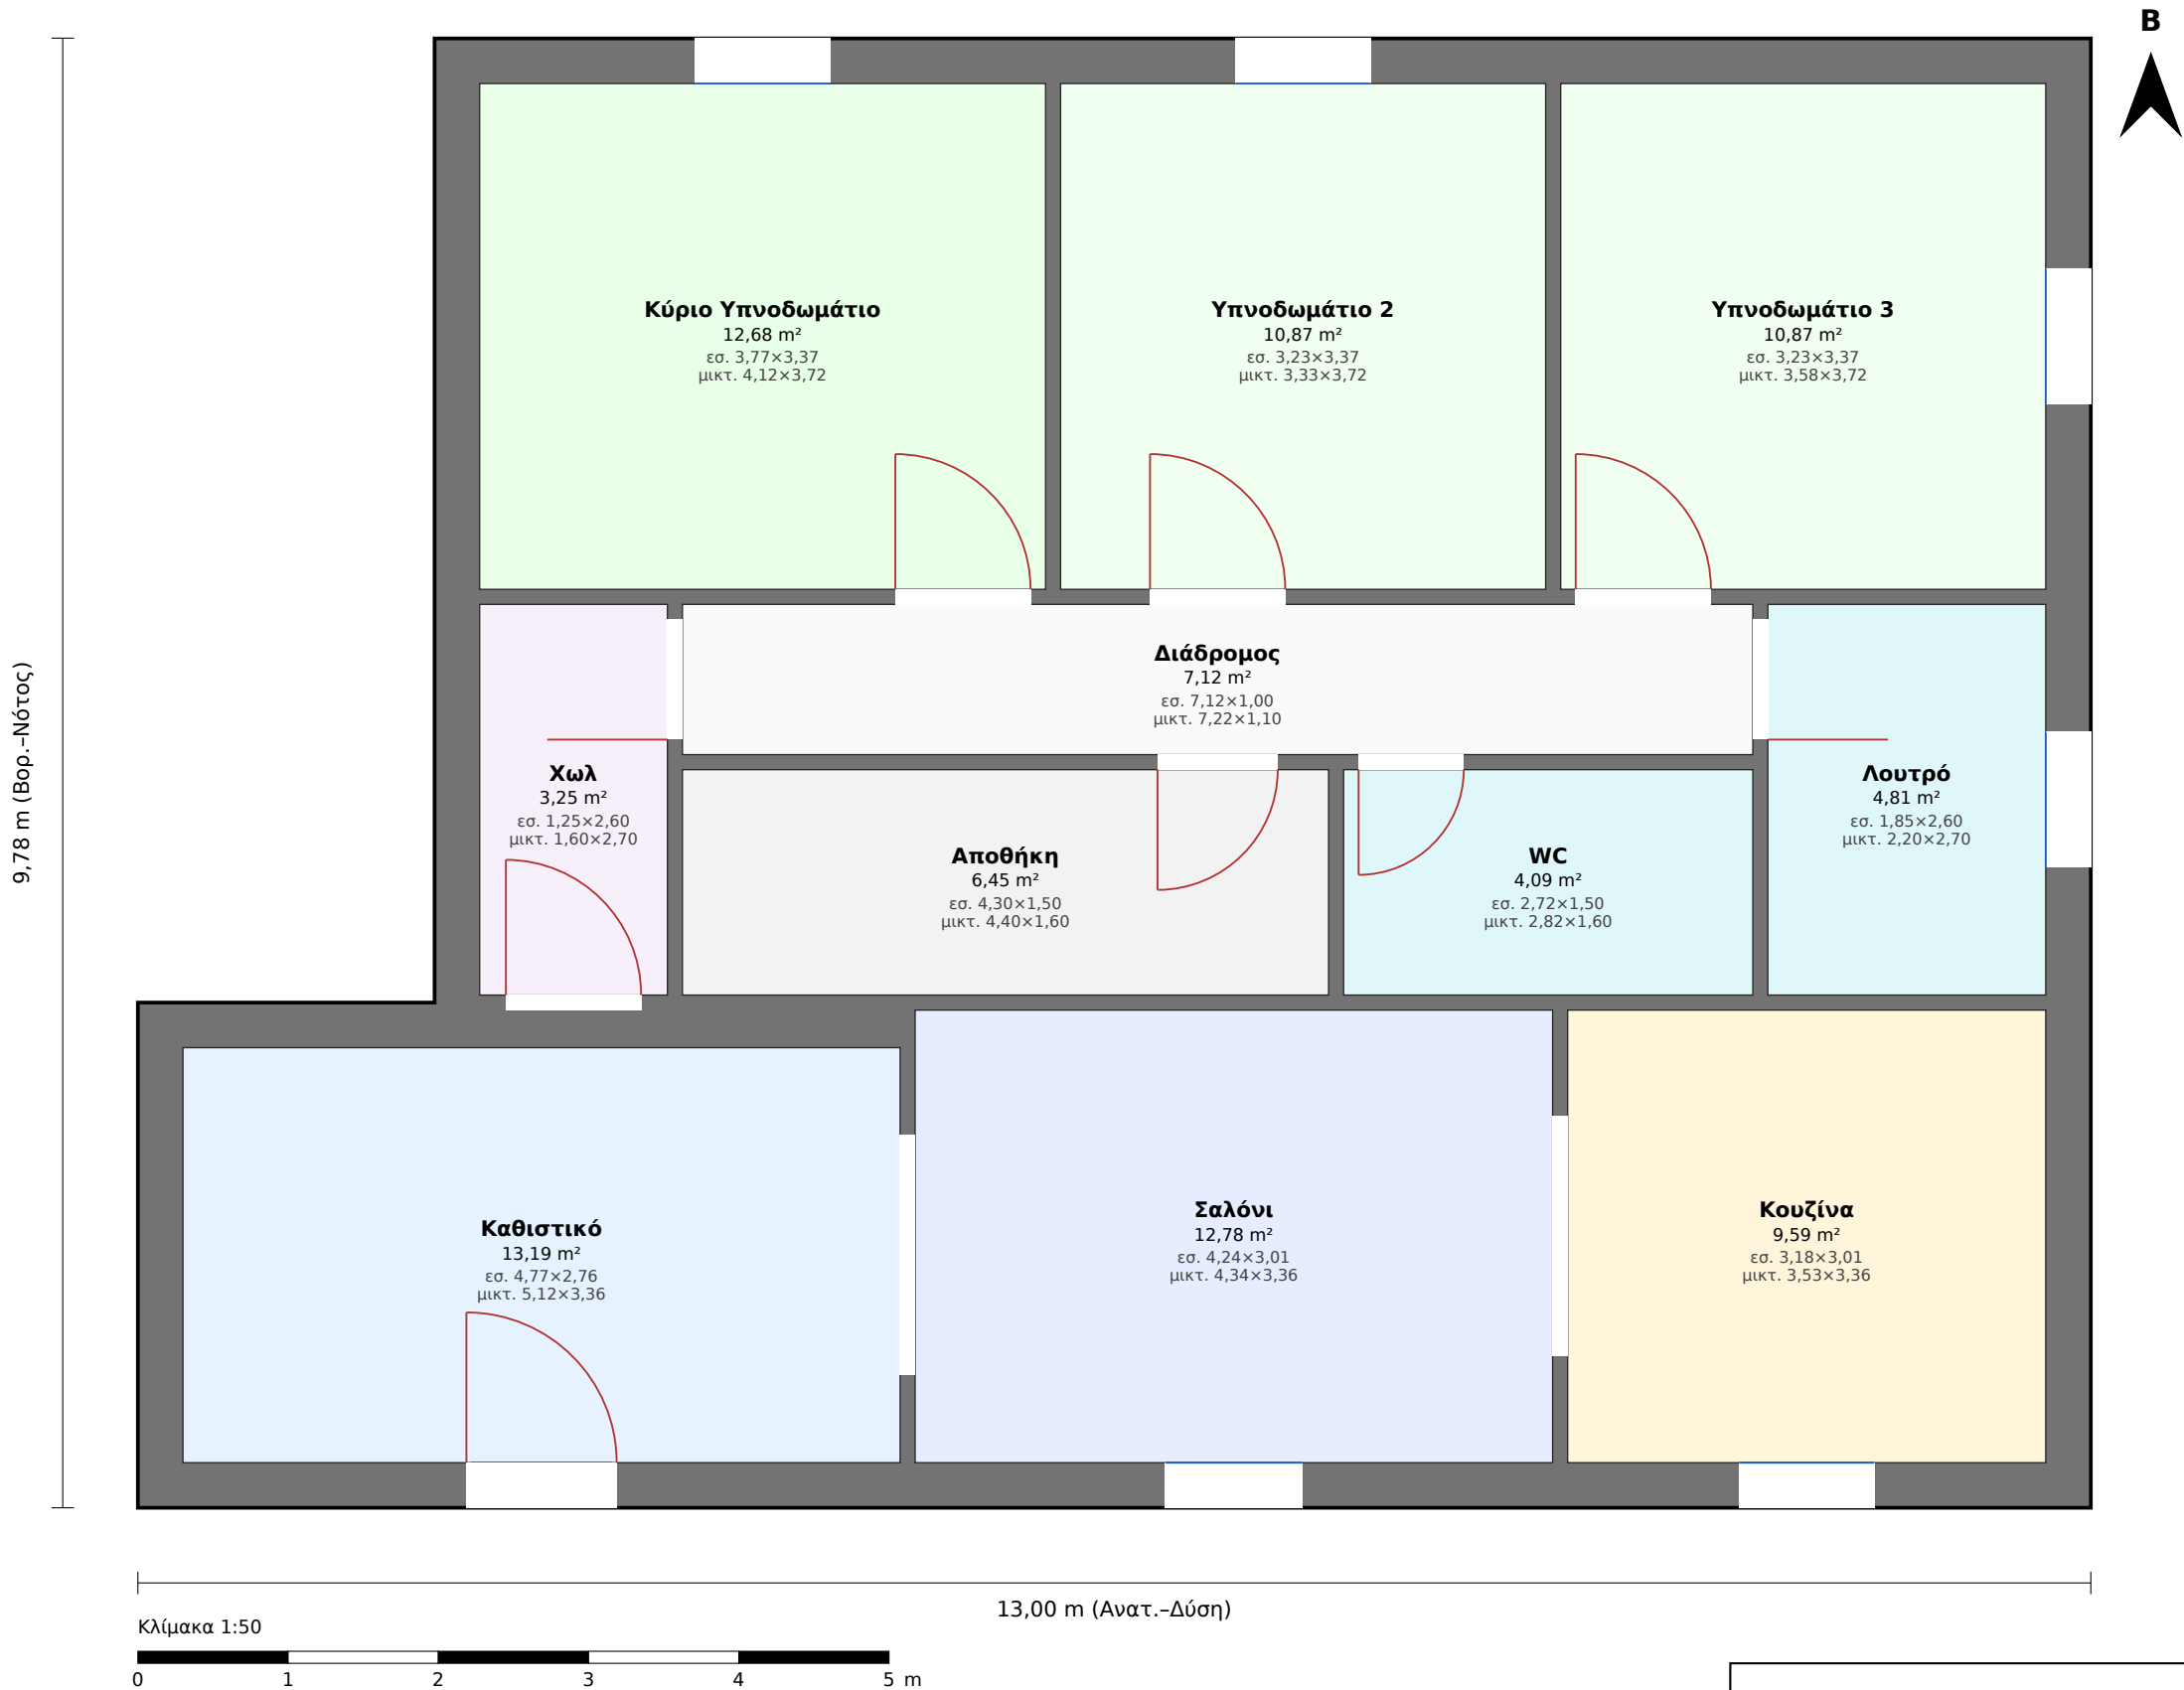

Τεχνικό Γραφείο Μελετών — Γεωργακόπουλος Χρ. / Φουντάς Αθ.
Έργο: Μονοκατοικία Αμαλιάδας
Πρόταση 3 — Ισόγειο
Κλίμακα 1:50 · Μικτό εμβ.: 114,44 m²
Είσοδος: Νότος · Αμαλιάδα, Π.Ε. Ηλείας
Ημερομηνία: 16.08.2026 · Σχεδ.: Γεωργακόπουλος Χρ. (ΑΜ ΤΕΕ 101893)

Μονοκατοικία Αμαλιάδας — Πρόταση 3: Πίνακες χώρων & έλεγχοι

Διαστάσεις: «καθαρές» = εσωτερικές ελεύθερες · «μικτές» = με τοίχους (εξωτ. πλήρες πάχος, εσωτ. μισό). Βορράς: επάνω.

■ Ισόγειο (μικτό 114,44 m², καθαρό 95,69 m²)

#	Χώρος	Καθ. εμβ. (m²)	Καθ. Α×Β (m)	Μικτές Α×Β (m)	Ζώνη
1	Καθιστικό	13,19	4,77×2,76	5,12×3,36	κύρια
2	Σαλόνι	12,78	4,24×3,01	4,34×3,36	κύρια
3	Κουζίνα	9,59	3,18×3,01	3,53×3,36	κύρια
4	Κύριο Υπνοδωμάτιο	12,68	3,77×3,37	4,12×3,72	κύρια
5	Υπνοδωμάτιο 2	10,87	3,23×3,37	3,33×3,72	κύρια
6	Υπνοδωμάτιο 3	10,87	3,23×3,37	3,58×3,72	κύρια
7	Χωλ	3,25	1,25×2,60	1,60×2,70	βοηθ.
8	Αποθήκη	6,45	4,30×1,50	4,40×1,60	βοηθ.
9	WC	4,09	2,72×1,50	2,82×1,60	βοηθ.
10	Λουτρό	4,81	1,85×2,60	2,20×2,70	βοηθ.
11	Διάδρομος	7,12	7,12×1,00	7,22×1,10	βοηθ.

Έλεγχος φωτισμού & αερισμού (Κ.Κ. αρ. 20 §5.1.2 / αρ. 21 §5.2)

Χώρος	Εμβ.	Φως≥10%	Υαλοπ.	Αερ.≥5%	Ανοιγ.	Φως	Αερ.
Καθιστικό	13,2	1,32	1,32	0,66	0,66	✓	✓
Σαλόνι	12,8	1,28	1,28	0,64	0,64	✓	✓
Κουζίνα	9,6	0,96	1,26	0,48	0,63	✓	✓
Κύριο Υπνοδωμάτιο	12,7	1,27	1,27	0,63	0,63	✓	✓
Υπνοδωμάτιο 2	10,9	1,09	1,26	0,54	0,63	✓	✓
Υπνοδωμάτιο 3	10,9	1,09	1,26	0,54	0,63	✓	✓
Χωλ	3,2	0,32	0,00	0,16	0,00	✓	✓
Αποθήκη	6,5	0,65	0,00	0,32	0,00	✓	✓
WC	4,1	0,41	0,00	0,20	0,00	✓	✓
Λουτρό	4,8	0,48	1,26	0,24	0,63	✓	✓

→ Όλοι οι χώροι κύριας χρήσης πληρούν φωτισμό ≥10% & αερισμό ≥5%.