


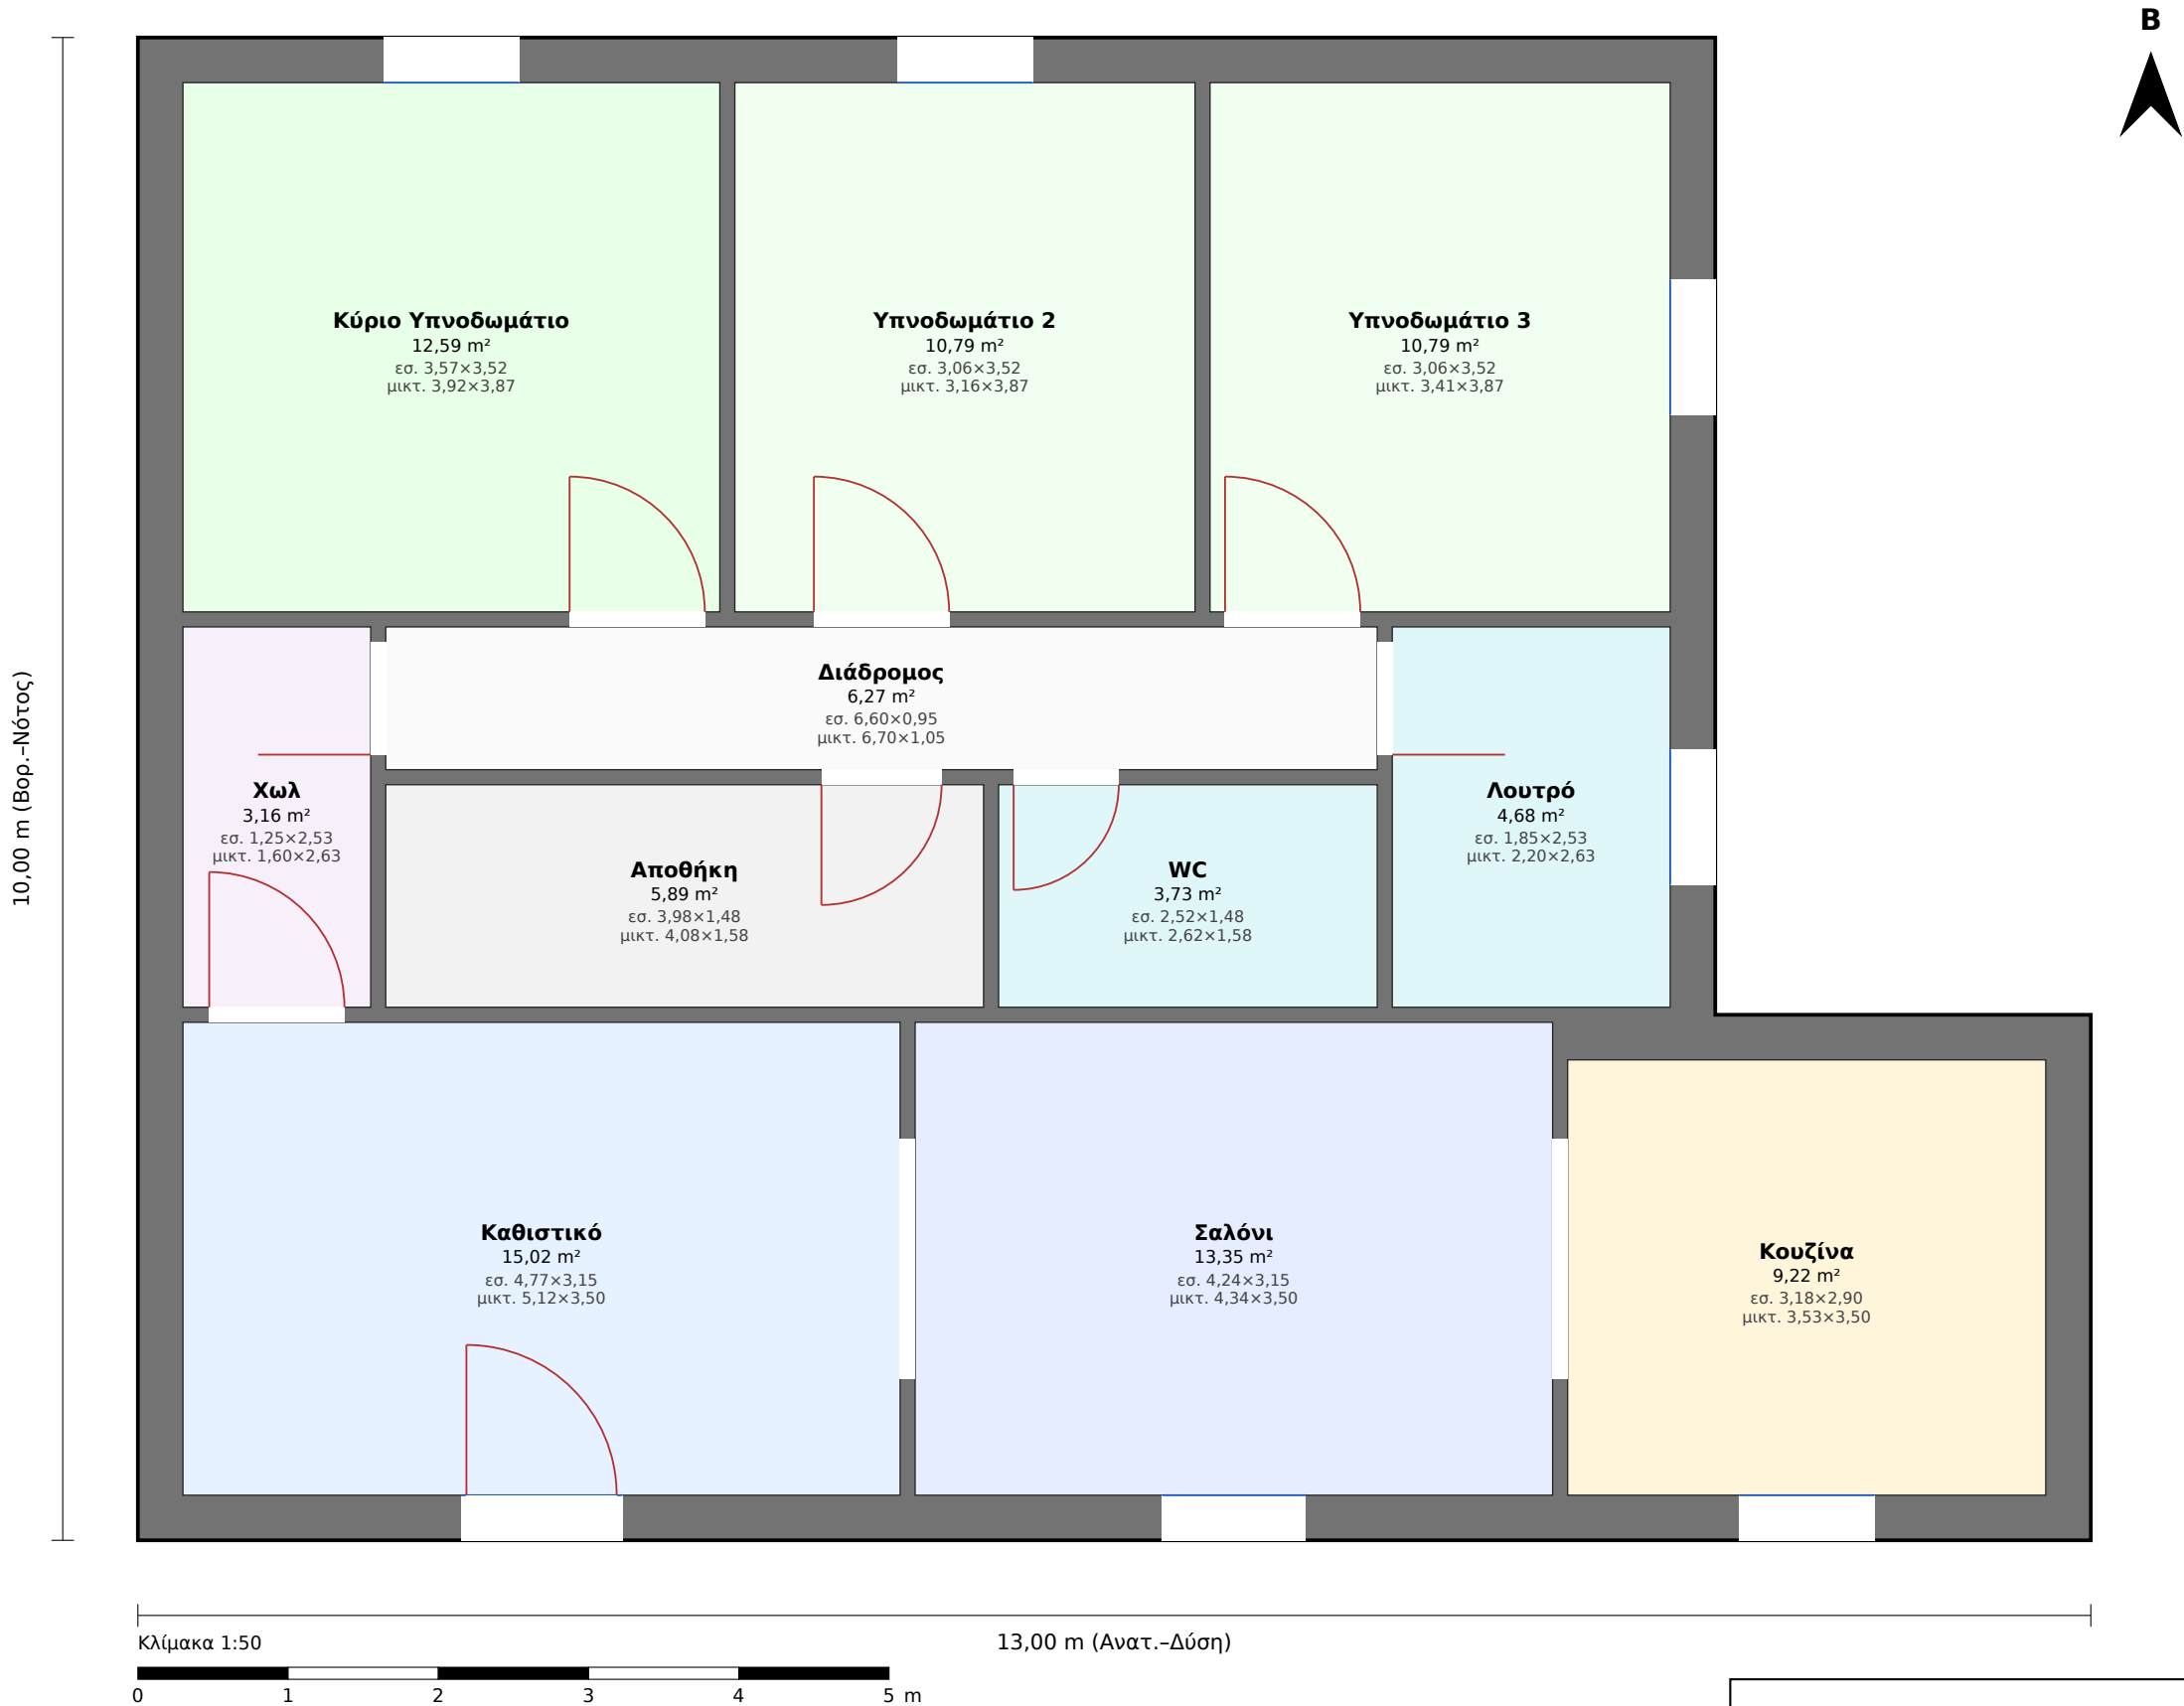

Τεχνικό Γραφείο Μελετών — Γεωργακόπουλος Χρ. / Φουντάς Αθ.
Έργο: Μονοκατοικία Αμαλιάδας
Πρόταση 1 — Ισόγειο
Κλίμακα 1:50 · Μικτό εμβ.: 113,74 m²
Είσοδος: Νότος · Αμαλιάδα, Π.Ε. Ηλείας
Ημερομηνία: 16.08.2026 · Σχεδ.: Γεωργακόπουλος Χρ. (AM TEE 101893)

Μονοκατοικία Αμαλιάδας — Πρόταση 1: Πίνακες χώρων & έλεγχοι

Διαστάσεις: «καθαρές» = εσωτερικές ελεύθερες · «μικτές» = με τοίχους (εξωτ. πλήρες πάχος, εσωτ. μισό). Βορράς: επάνω.

■ **Ισόγειο (μικτό 113,74 m², καθαρό 95,50 m²)**

#	Χώρος	Καθ. εμβ. (m²)	Καθ. Α×Β (m)	Μικτές Α×Β (m)	Ζώνη
1	Καθιστικό	15,02	4,77×3,15	5,12×3,50	κύρια
2	Σαλόνι	13,35	4,24×3,15	4,34×3,50	κύρια
3	Κουζίνα	9,22	3,18×2,90	3,53×3,50	κύρια
4	Κύριο Υπνοδωμάτιο	12,59	3,57×3,52	3,92×3,87	κύρια
5	Υπνοδωμάτιο 2	10,79	3,06×3,52	3,16×3,87	κύρια
6	Υπνοδωμάτιο 3	10,79	3,06×3,52	3,41×3,87	κύρια
7	Χωλ	3,16	1,25×2,53	1,60×2,63	βοηθ.
8	Αποθήκη	5,89	3,98×1,48	4,08×1,58	βοηθ.
9	WC	3,73	2,52×1,48	2,62×1,58	βοηθ.
10	Λουτρό	4,68	1,85×2,53	2,20×2,63	βοηθ.
11	Διάδρομος	6,27	6,60×0,95	6,70×1,05	βοηθ.

Έλεγχος φωτισμού & αερισμού (Κ.Κ. αρ. 20 §5.1.2 / αρ. 21 §5.2)

Χώρος	Εμβ.	Φως≥10%	Υαλοπ.	Αερ.≥5%	Ανοιγ.	Φως	Αερ.
Καθιστικό	15,0	1,50	1,50	0,75	0,75	✓	✓
Σαλόνι	13,4	1,34	1,34	0,67	0,67	✓	✓
Κουζίνα	9,2	0,92	1,26	0,46	0,63	✓	✓
Κύριο Υπνοδωμάτιο	12,6	1,26	1,26	0,63	0,63	✓	✓
Υπνοδωμάτιο 2	10,8	1,08	1,26	0,54	0,63	✓	✓
Υπνοδωμάτιο 3	10,8	1,08	1,26	0,54	0,63	✓	✓
Χωλ	3,2	0,32	0,00	0,16	0,00	✓	✓
Αποθήκη	5,9	0,59	0,00	0,29	0,00	✓	✓
WC	3,7	0,37	0,00	0,19	0,00	✓	✓
Λουτρό	4,7	0,47	1,26	0,23	0,63	✓	✓

→ Όλοι οι χώροι κύριας χρήσης πληρούν φωτισμό ≥10% & αερισμό ≥5%.