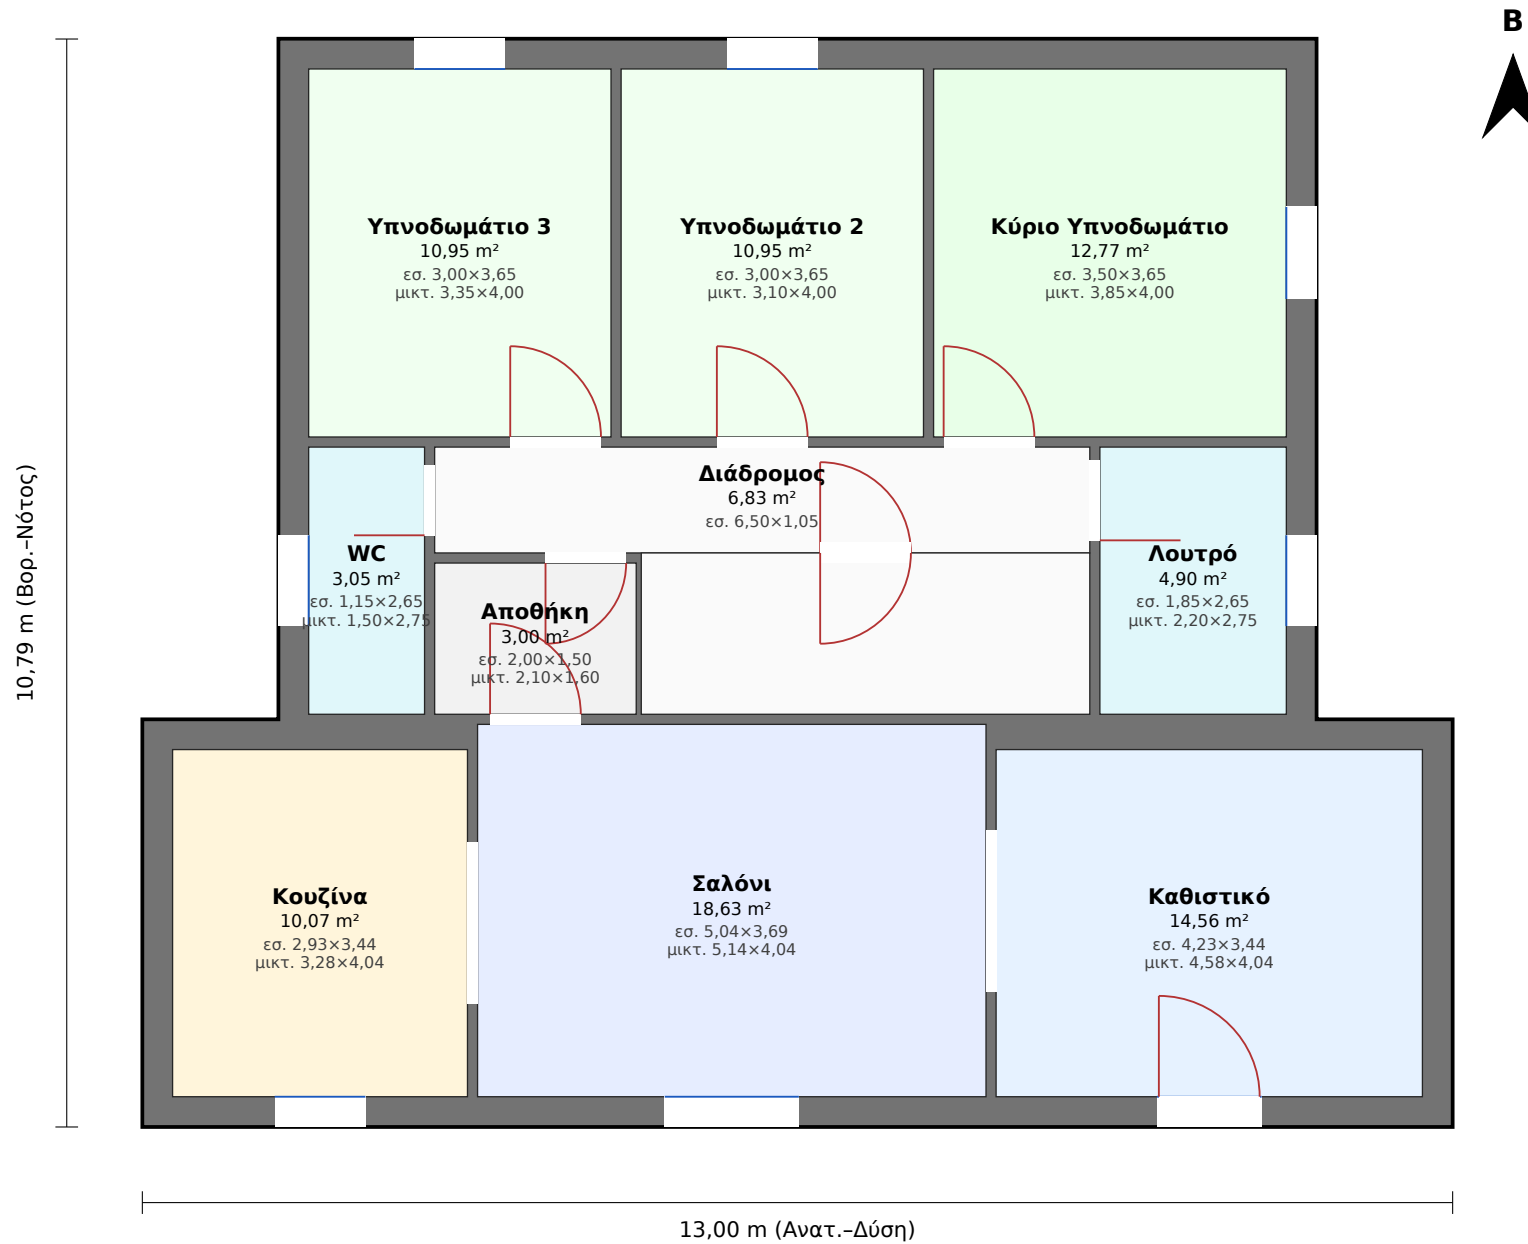


Τεχνικό Γραφείο Μελετών — Γεωργακόπουλος Χρ. / Φουντάς Αθ.
Έργο: Μονοκατοικία Αμαλιάδας
Πρόταση 2 — Ισόγειο
Κλίμακα 1:75 · Μικτό εμβ.: 122,08 m²
Είσοδος: Νότος · Αμαλιάδα, Π.Ε. Ηλείας
Ημερομηνία: 16.08.2026 · Σχεδ.: Γεωργακόπουλος Χρ. (ΑΜ ΤΕΕ 101893)

Μονοκατοικία Αμαλιάδας — Πρόταση 2: Πίνακες χώρων & έλεγχοι

Διαστάσεις: «καθαρές» = εσωτερικές ελεύθερες · «μικτές» = με τοίχους (εξωτ. πλήρες πάχος, εσωτ. μισό). Βορράς: επάνω.

■ **Ισόγειο** (μικτό 122,08 m², καθαρό 102,84 m²)

#	Χώρος	Καθ. εμβ. (m²)	Καθ. Α×Β (m)	Μικτές Α×Β (m)	Ζώνη
1	Κουζίνα	10,07	2,93×3,44	3,28×4,04	κύρια
2	Σαλόνι	18,63	5,04×3,69	5,14×4,04	κύρια
3	Καθιστικό	14,56	4,23×3,44	4,58×4,04	κύρια
4	Υπνοδωμάτιο 3	10,95	3,00×3,65	3,35×4,00	κύρια
5	Υπνοδωμάτιο 2	10,95	3,00×3,65	3,10×4,00	κύρια
6	Κύριο Υπνοδωμάτιο	12,77	3,50×3,65	3,85×4,00	κύρια
7	WC	3,05	1,15×2,65	1,50×2,75	βοηθ.
8	Αποθήκη	3,00	2,00×1,50	2,10×1,60	βοηθ.
9	Λουτρό	4,90	1,85×2,65	2,20×2,75	βοηθ.
10	Διάδρομος	6,83	6,50×1,05	6,60×1,15	βοηθ.
11		7,12	4,45×1,60	4,55×1,70	βοηθ.

Έλεγχος φωτισμού & αερισμού (Κ.Κ. αρ. 20 §5.1.2 / αρ. 21 §5.2)

Χώρος	Εμβ.	Φως≥10%	Υαλοπ.	Αερ.≥5%	Ανοιγ.	Φως	Αερ.
Κουζίνα	10,1	1,01	1,26	0,50	0,63	✓	✓
Σαλόνι	18,6	1,86	1,86	0,93	0,93	✓	✓
Καθιστικό	14,6	1,46	1,46	0,73	0,73	✓	✓
Υπνοδωμάτιο 3	10,9	1,09	1,26	0,55	0,63	✓	✓
Υπνοδωμάτιο 2	10,9	1,09	1,26	0,55	0,63	✓	✓
Κύριο Υπνοδωμάτιο	12,8	1,28	1,28	0,64	0,64	✓	✓
WC	3,0	0,30	1,26	0,15	0,63	✓	✓
Αποθήκη	3,0	0,30	0,00	0,15	0,00	✓	✓
Λουτρό	4,9	0,49	1,26	0,25	0,63	✓	✓

→ Όλοι οι χώροι κύριας χρήσης πληρούν φωτισμό ≥10% & αερισμό ≥5%.