


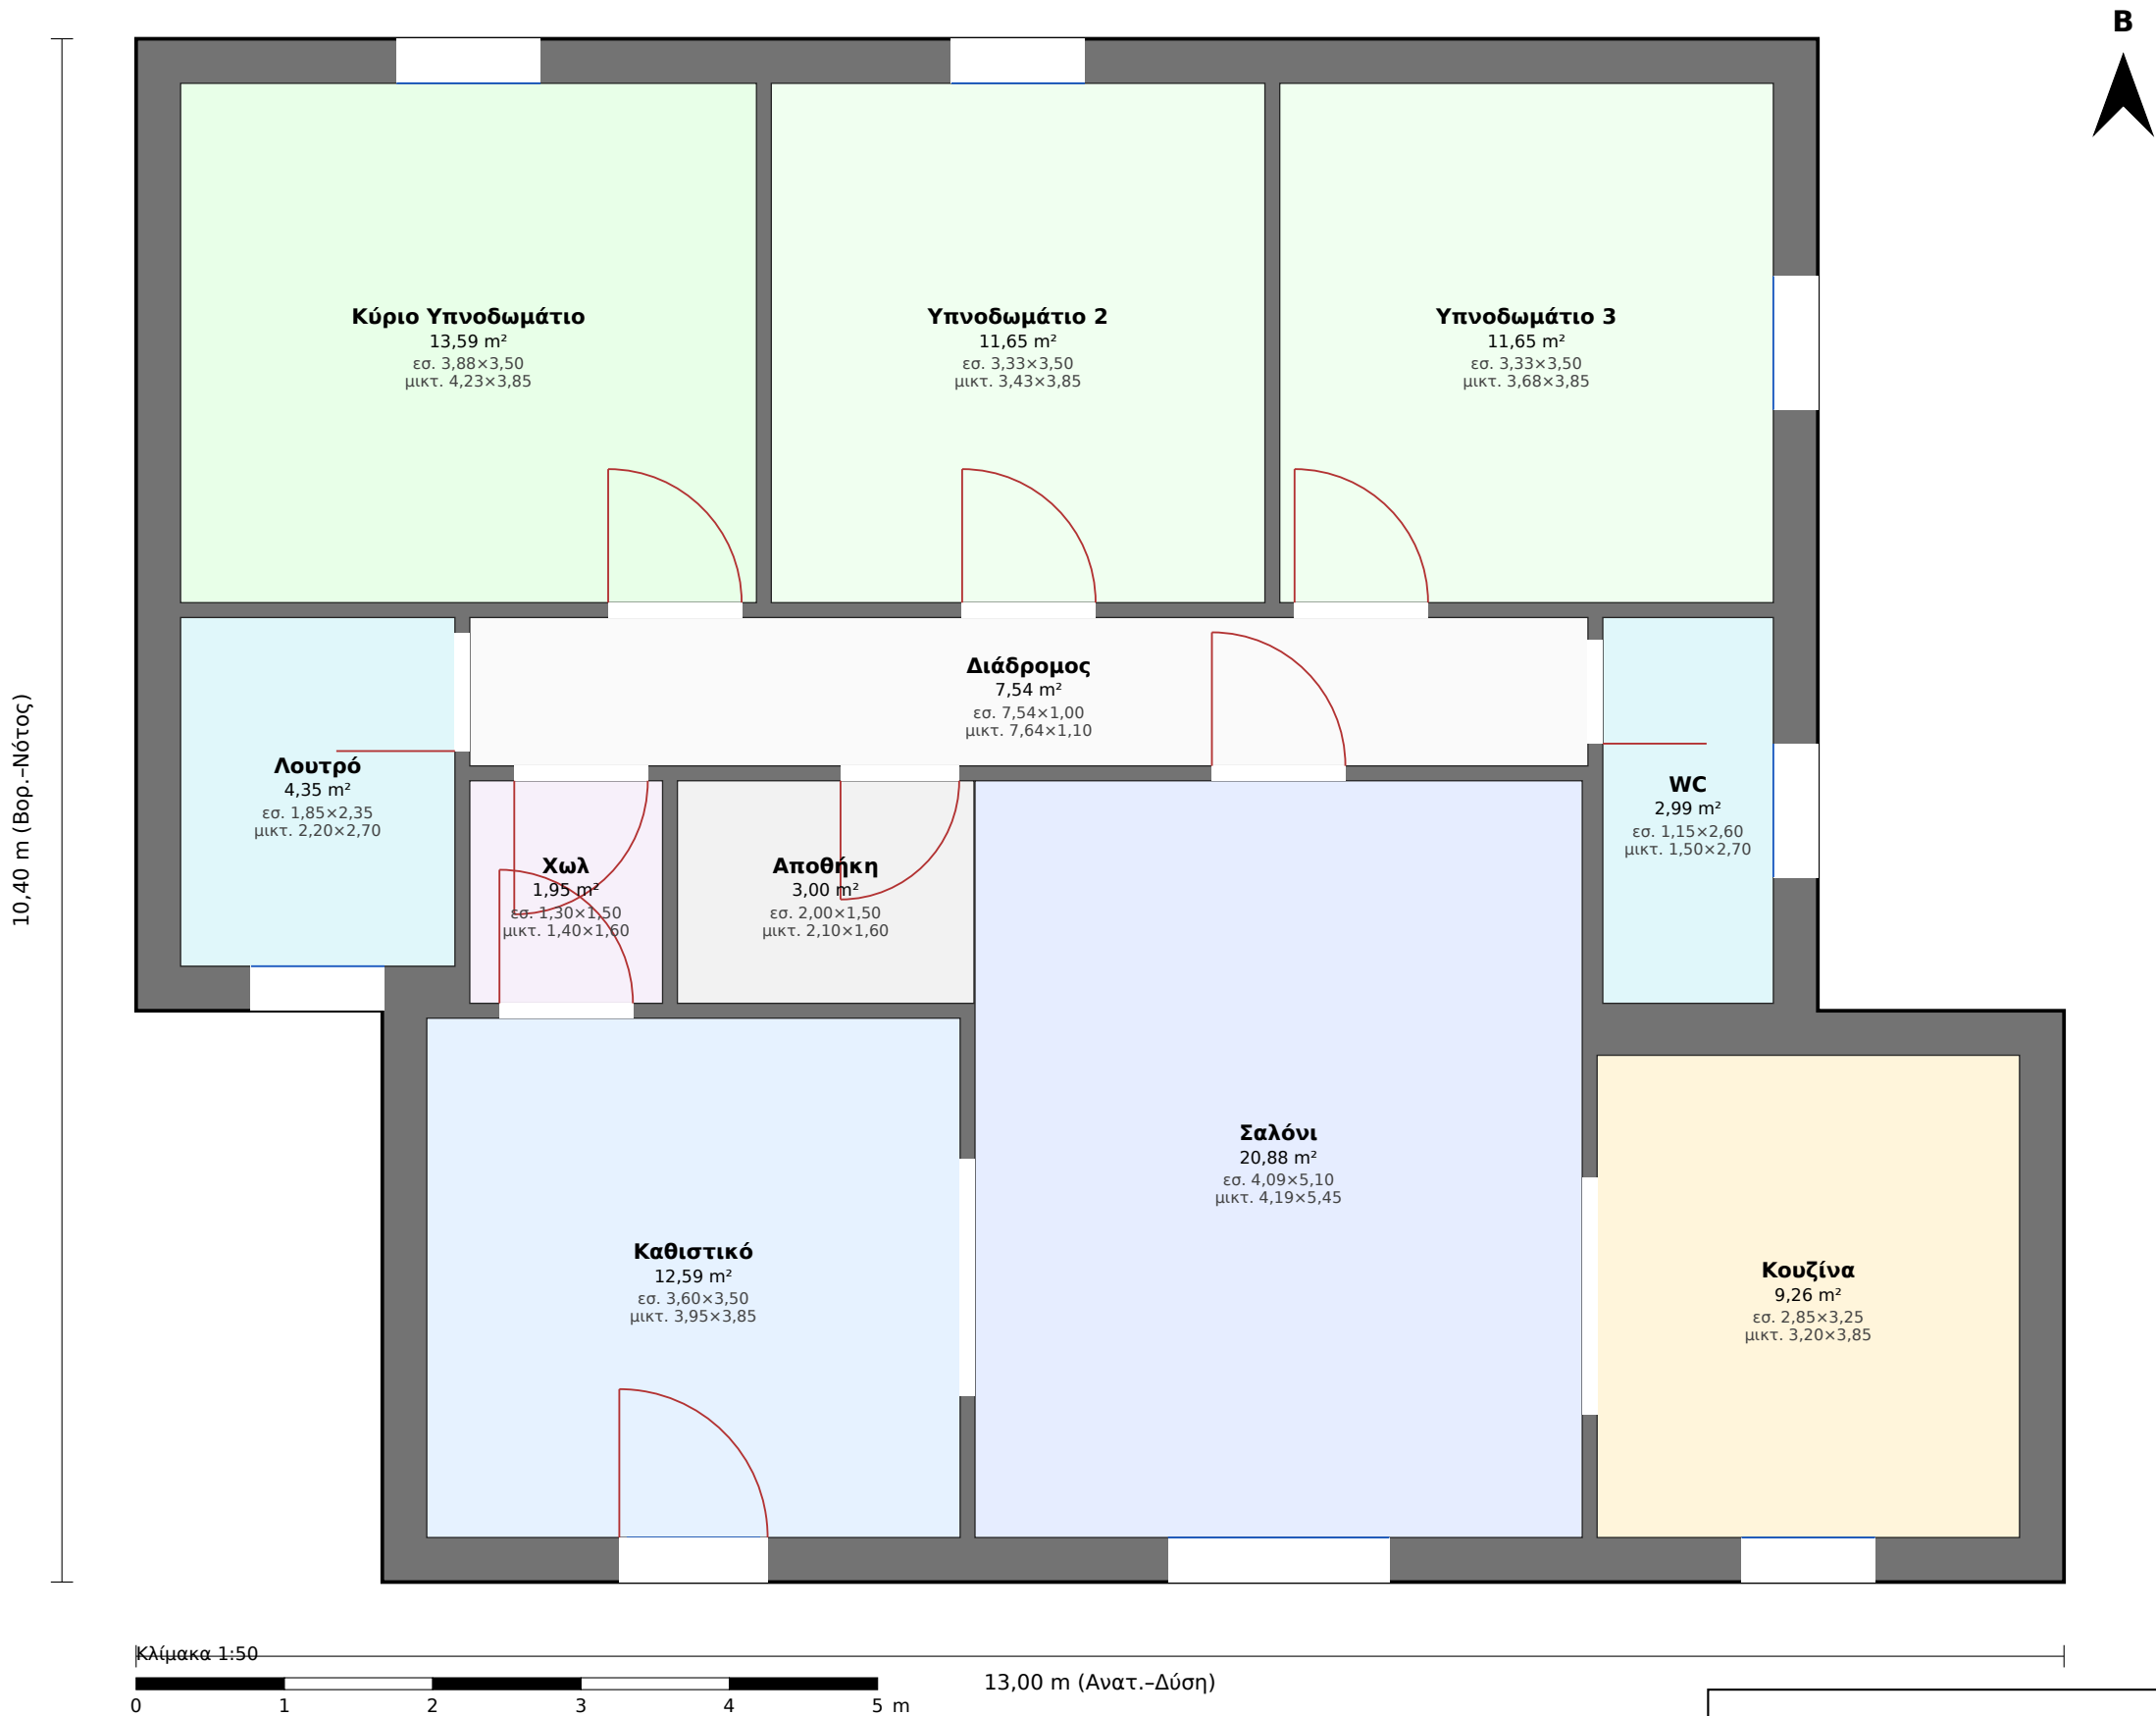

Τεχνικό Γραφείο Μελετών — Γεωργακόπουλος Χρ. / Φουντάς Αθ.
Έργο: Μονοκατοικία Αμαλιάδας
Πρόταση 3 — Ισόγειο
Κλίμακα 1:50 · Μικτό εμβ.: 117,94 m²
Είσοδος: Νότος · Αμαλιάδα, Π.Ε. Ηλείας
Ημερομηνία: 17.08.2026 · Σχεδ.: Γεωργακόπουλος Χρ. (AM TEE 101893)

Μονοκατοικία Αμαλιάδας — Πρόταση 3: Πίνακες χώρων & έλεγχοι

Διαστάσεις: «καθαρές» = εσωτερικές ελεύθερες · «μικτές» = με τοίχους (εξωτ. πλήρες πάχος, εσωτ. μισό). Βορράς: επάνω.

■ Ισόγειο (μικτό 117,94 m², καθαρό 99,45 m²)

#	Χώρος	Καθ. εμβ. (m²)	Καθ. Α×Β (m)	Μικτές Α×Β (m)	Ζώνη
1	Καθιστικό	12,59	3,60×3,50	3,95×3,85	κύρια
2	Σαλόνι	20,88	4,09×5,10	4,19×5,45	κύρια
3	Κουζίνα	9,26	2,85×3,25	3,20×3,85	κύρια
4	Κύριο Υπνοδωμάτιο	13,59	3,88×3,50	4,23×3,85	κύρια
5	Υπνοδωμάτιο 2	11,65	3,33×3,50	3,43×3,85	κύρια
6	Υπνοδωμάτιο 3	11,65	3,33×3,50	3,68×3,85	κύρια
7	Λουτρό	4,35	1,85×2,35	2,20×2,70	βοηθ.
8	Χωλ	1,95	1,30×1,50	1,40×1,60	βοηθ.
9	Αποθήκη	3,00	2,00×1,50	2,10×1,60	βοηθ.
10	WC	2,99	1,15×2,60	1,50×2,70	βοηθ.
11	Διάδρομος	7,54	7,54×1,00	7,64×1,10	βοηθ.

Έλεγχος φωτισμού & αερισμού (Κ.Κ. αρ. 20 §5.1.2 / αρ. 21 §5.2)

Χώρος	Εμβ.	Φως≥10%	Υαλοπ.	Αερ.≥5%	Ανοιγ.	Φως	Αερ.
Καθιστικό	12,6	1,26	1,26	0,63	0,63	✓	✓
Σαλόνι	20,9	2,09	2,09	1,04	1,04	✓	✓
Κουζίνα	9,3	0,93	1,26	0,46	0,63	✓	✓
Κύριο Υπνοδωμάτιο	13,6	1,36	1,36	0,68	0,68	✓	✓
Υπνοδωμάτιο 2	11,6	1,16	1,26	0,58	0,63	✓	✓
Υπνοδωμάτιο 3	11,6	1,16	1,26	0,58	0,63	✓	✓
Λουτρό	4,3	0,43	1,26	0,22	0,63	✓	✓
Χωλ	2,0	0,20	0,00	0,10	0,00	✓	✓
Αποθήκη	3,0	0,30	0,00	0,15	0,00	✓	✓
WC	3,0	0,30	1,26	0,15	0,63	✓	✓

→ Όλοι οι χώροι κύριας χρήσης πληρούν φωτισμό ≥10% & αερισμό ≥5%.