



Τεχνικό Γραφείο Μελετών — Γεωργακόπουλος Χρ. / Φουντάς Αθ.
Έργο: Μονοκατοικία Αμαλιάδας
Πρόταση 1 — Ισόγειο
Κλίμακα 1:50 · Μικτό εμβ.: 113,74 m²
Είσοδος: Νότος · Αμαλιάδα, Π.Ε. Ηλείας
Ημερομηνία: 15.08.2026 · Σχεδ.: Γεωργακόπουλος Χρ. (ΑΜ ΤΕΕ 101893)

Μονοκατοικία Αμαλιάδας — Πρόταση 1: Πίνακες χώρων & έλεγχοι

Διαστάσεις: «καθαρές» = εσωτερικές ελεύθερες · «μικτές» = με τοίχους (εξωτ. πλήρες πάχος, εσωτ. μισό). Βορράς: επάνω.


■ Ισόγειο (μικτό 113,74 m², καθαρό 96,18 m²)

#	Χώρος	Καθ. εμβ. (m²)	Καθ. Α×Β (m)	Μικτές Α×Β (m)	Ζώνη
1	Καθιστικό	15,02	4,77×3,15	5,12×3,50	κύρια
2	Σαλόνι	13,35	4,24×3,15	4,34×3,50	κύρια
3	Κουζίνα	10,02	3,18×3,15	3,53×3,50	κύρια
4	Κύριο Υπνοδωμάτιο	12,59	3,57×3,52	3,92×3,87	κύρια
5	Υπνοδωμάτιο 2	10,79	3,06×3,52	3,16×3,87	κύρια
6	Υπνοδωμάτιο 3	10,79	3,06×3,52	3,41×3,87	κύρια
7	Λουτρό	4,78	3,23×1,48	3,58×1,58	βοηθ.
8	WC	2,27	1,53×1,48	1,63×1,58	βοηθ.
9	Αποθήκη	3,58	2,42×1,48	2,52×1,58	βοηθ.
10	Χωλ	3,58	2,42×1,48	2,77×1,58	βοηθ.
11	Διάδρομος	9,41	9,90×0,95	10,00×1,05	βοηθ.

Έλεγχος φωτισμού & αερισμού (Κ.Κ. αρ. 20 §5.1.2 / αρ. 21 §5.2)

Χώρος	Εμβ.	Φως≥10%	Υαλοπ.	Αερ.≥5%	Ανοιγ.	Φως	Αερ.
Καθιστικό	15,0	1,50	1,50	0,75	0,75	✓	✓
Σαλόνι	13,4	1,34	1,34	0,67	0,67	✓	✓
Κουζίνα	10,0	1,00	1,26	0,50	0,63	✓	✓
Κύριο Υπνοδωμάτιο	12,6	1,26	1,26	0,63	0,63	✓	✓
Υπνοδωμάτιο 2	10,8	1,08	1,26	0,54	0,63	✓	✓
Υπνοδωμάτιο 3	10,8	1,08	1,26	0,54	0,63	✓	✓
Λουτρό	4,8	0,48	1,23	0,24	0,62	✓	✓
WC	2,3	0,23	0,00	0,11	0,00	✓	✓
Αποθήκη	3,6	0,36	0,00	0,18	0,00	✓	✓
Χωλ	3,6	0,36	0,00	0,18	0,00	✓	✓

→ Όλοι οι χώροι κύριας χρήσης πληρούν φωτισμό ≥10% & αερισμό ≥5%.

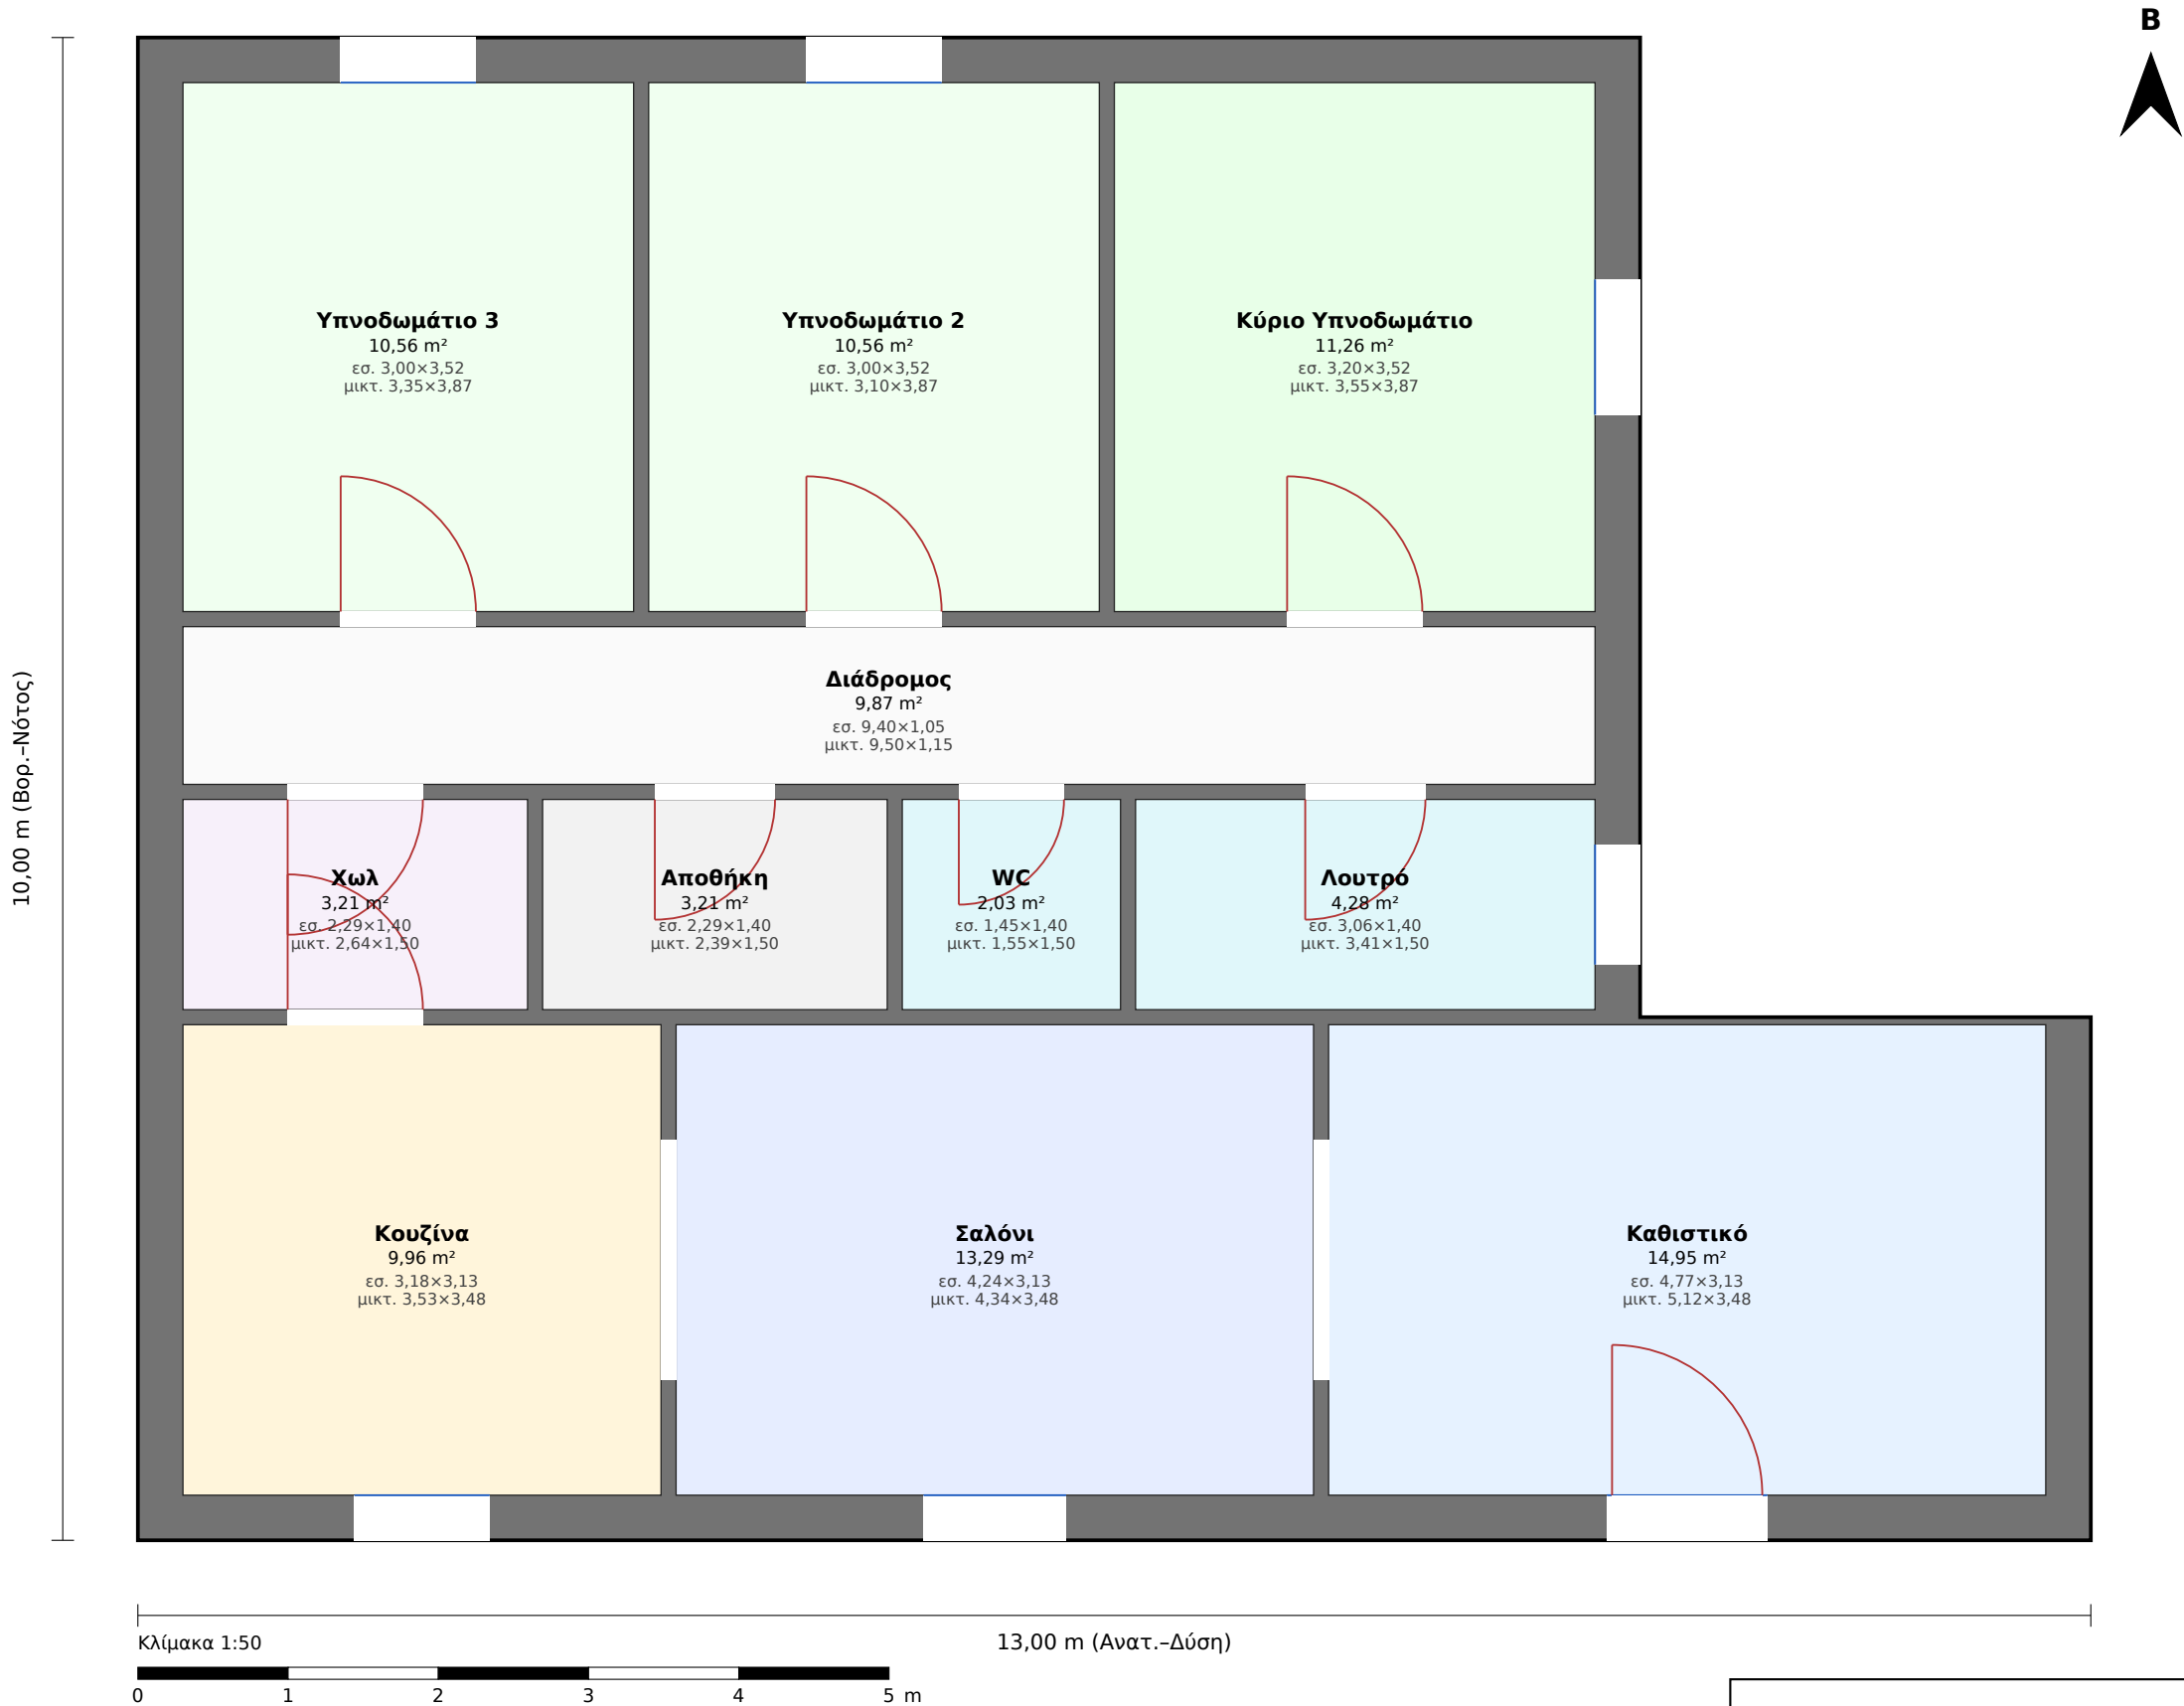

Τεχνικό Γραφείο Μελετών — Γεωργακόπουλος Χρ. / Φουντάς Αθ.
Έργο: Μονοκατοικία Αμαλιάδας
Πρόταση 2 — Ισόγειο
Κλίμακα 1:50 · Μικτό εμβ.: 110,44 m²
Είσοδος: Νότος · Αμαλιάδα, Π.Ε. Ηλείας
Ημερομηνία: 15.08.2026 · Σχεδ.: Γεωργακόπουλος Χρ. (ΑΜ ΤΕΕ 101893)

Μονοκατοικία Αμαλιάδας — Πρόταση 2: Πίνακες χώρων & έλεγχοι

Διαστάσεις: «καθαρές» = εσωτερικές ελεύθερες · «μικτές» = με τοίχους (εξωτ. πλήρες πάχος, εσωτ. μισό). Βορράς: επάνω.

■ **Ισόγειο (μικτό 110,44 m², καθαρό 93,18 m²)**

#	Χώρος	Καθ. εμβ. (m²)	Καθ. Α×Β (m)	Μικτές Α×Β (m)	Ζώνη
1	Κουζίνα	9,96	3,18×3,13	3,53×3,48	κύρια
2	Σαλόνι	13,29	4,24×3,13	4,34×3,48	κύρια
3	Καθιστικό	14,95	4,77×3,13	5,12×3,48	κύρια
4	Υπνοδωμάτιο 3	10,56	3,00×3,52	3,35×3,87	κύρια
5	Υπνοδωμάτιο 2	10,56	3,00×3,52	3,10×3,87	κύρια
6	Κύριο Υπνοδωμάτιο	11,26	3,20×3,52	3,55×3,87	κύρια
7	Χωλ	3,21	2,29×1,40	2,64×1,50	βοηθ.
8	Αποθήκη	3,21	2,29×1,40	2,39×1,50	βοηθ.
9	WC	2,03	1,45×1,40	1,55×1,50	βοηθ.
10	Λουτρό	4,28	3,06×1,40	3,41×1,50	βοηθ.
11	Διάδρομος	9,87	9,40×1,05	9,50×1,15	βοηθ.

Έλεγχος φωτισμού & αερισμού (Κ.Κ. αρ. 20 §5.1.2 / αρ. 21 §5.2)

Χώρος	Εμβ.	Φως≥10%	Υαλοπ.	Αερ.≥5%	Ανοιγ.	Φως	Αερ.
Κουζίνα	10,0	1,00	1,26	0,50	0,63	✓	✓
Σαλόνι	13,3	1,33	1,33	0,66	0,66	✓	✓
Καθιστικό	14,9	1,49	1,49	0,75	0,75	✓	✓
Υπνοδωμάτιο 3	10,6	1,06	1,26	0,53	0,63	✓	✓
Υπνοδωμάτιο 2	10,6	1,06	1,26	0,53	0,63	✓	✓
Κύριο Υπνοδωμάτιο	11,3	1,13	1,26	0,56	0,63	✓	✓
Χωλ	3,2	0,32	0,00	0,16	0,00	✓	✓
Αποθήκη	3,2	0,32	0,00	0,16	0,00	✓	✓
WC	2,0	0,20	0,00	0,10	0,00	✓	✓
Λουτρό	4,3	0,43	1,12	0,21	0,56	✓	✓

→ Όλοι οι χώροι κύριας χρήσης πληρούν φωτισμό ≥10% & αερισμό ≥5%.



Τεχνικό Γραφείο Μελετών — Γεωργακόπουλος Χρ. / Φουντάς Αθ.
Έργο: Μονοκατοικία Αμαλιάδας
Πρόταση 3 — Ισόγειο
Κλίμακα 1:50 · Μικτό εμβ.: 114,44 m²
Είσοδος: Νότος · Αμαλιάδα, Π.Ε. Ηλείας
Ημερομηνία: 15.08.2026 · Σχεδ.: Γεωργακόπουλος Χρ. (AM TEE 101893)

Μονοκατοικία Αμαλιάδας — Πρόταση 3: Πίνακες χώρων & έλεγχοι

Διαστάσεις: «καθαρές» = εσωτερικές ελεύθερες · «μικτές» = με τοίχους (εξωτ. πλήρες πάχος, εσωτ. μισό). Βορράς: επάνω.

■ Ισόγειο (μικτό 114,44 m², καθαρό 96,78 m²)

#	Χώρος	Καθ. εμβ. (m²)	Καθ. Α×Β (m)	Μικτές Α×Β (m)	Ζώνη
1	Καθιστικό	14,38	4,77×3,01	5,12×3,36	κύρια
2	Σαλόνι	12,78	4,24×3,01	4,34×3,36	κύρια
3	Κουζίνα	9,59	3,18×3,01	3,53×3,36	κύρια
4	Κύριο Υπνοδωμάτιο	12,68	3,77×3,37	4,12×3,72	κύρια
5	Υπνοδωμάτιο 2	10,87	3,23×3,37	3,33×3,72	κύρια
6	Υπνοδωμάτιο 3	10,87	3,23×3,37	3,58×3,72	κύρια
7	Λουτρό	5,11	3,40×1,50	3,75×1,60	βοηθ.
8	WC	2,42	1,62×1,50	1,72×1,60	βοηθ.
9	Αποθήκη	3,83	2,55×1,50	2,65×1,60	βοηθ.
10	Χωλ	3,83	2,55×1,50	2,90×1,60	βοηθ.
11	Διάδρομος	10,42	10,42×1,00	10,53×1,10	βοηθ.

Έλεγχος φωτισμού & αερισμού (Κ.Κ. αρ. 20 §5.1.2 / αρ. 21 §5.2)

Χώρος	Εμβ.	Φως≥10%	Υαλοπ.	Αερ.≥5%	Ανοιγ.	Φως	Αερ.
Καθιστικό	14,4	1,44	1,44	0,72	0,72	✓	✓
Σαλόνι	12,8	1,28	1,28	0,64	0,64	✓	✓
Κουζίνα	9,6	0,96	1,26	0,48	0,63	✓	✓
Κύριο Υπνοδωμάτιο	12,7	1,27	1,27	0,63	0,63	✓	✓
Υπνοδωμάτιο 2	10,9	1,09	1,26	0,54	0,63	✓	✓
Υπνοδωμάτιο 3	10,9	1,09	1,26	0,54	0,63	✓	✓
Λουτρό	5,1	0,51	1,26	0,26	0,63	✓	✓
WC	2,4	0,24	0,00	0,12	0,00	✓	✓
Αποθήκη	3,8	0,38	0,00	0,19	0,00	✓	✓
Χωλ	3,8	0,38	0,00	0,19	0,00	✓	✓

→ Όλοι οι χώροι κύριας χρήσης πληρούν φωτισμό ≥10% & αερισμό ≥5%.