


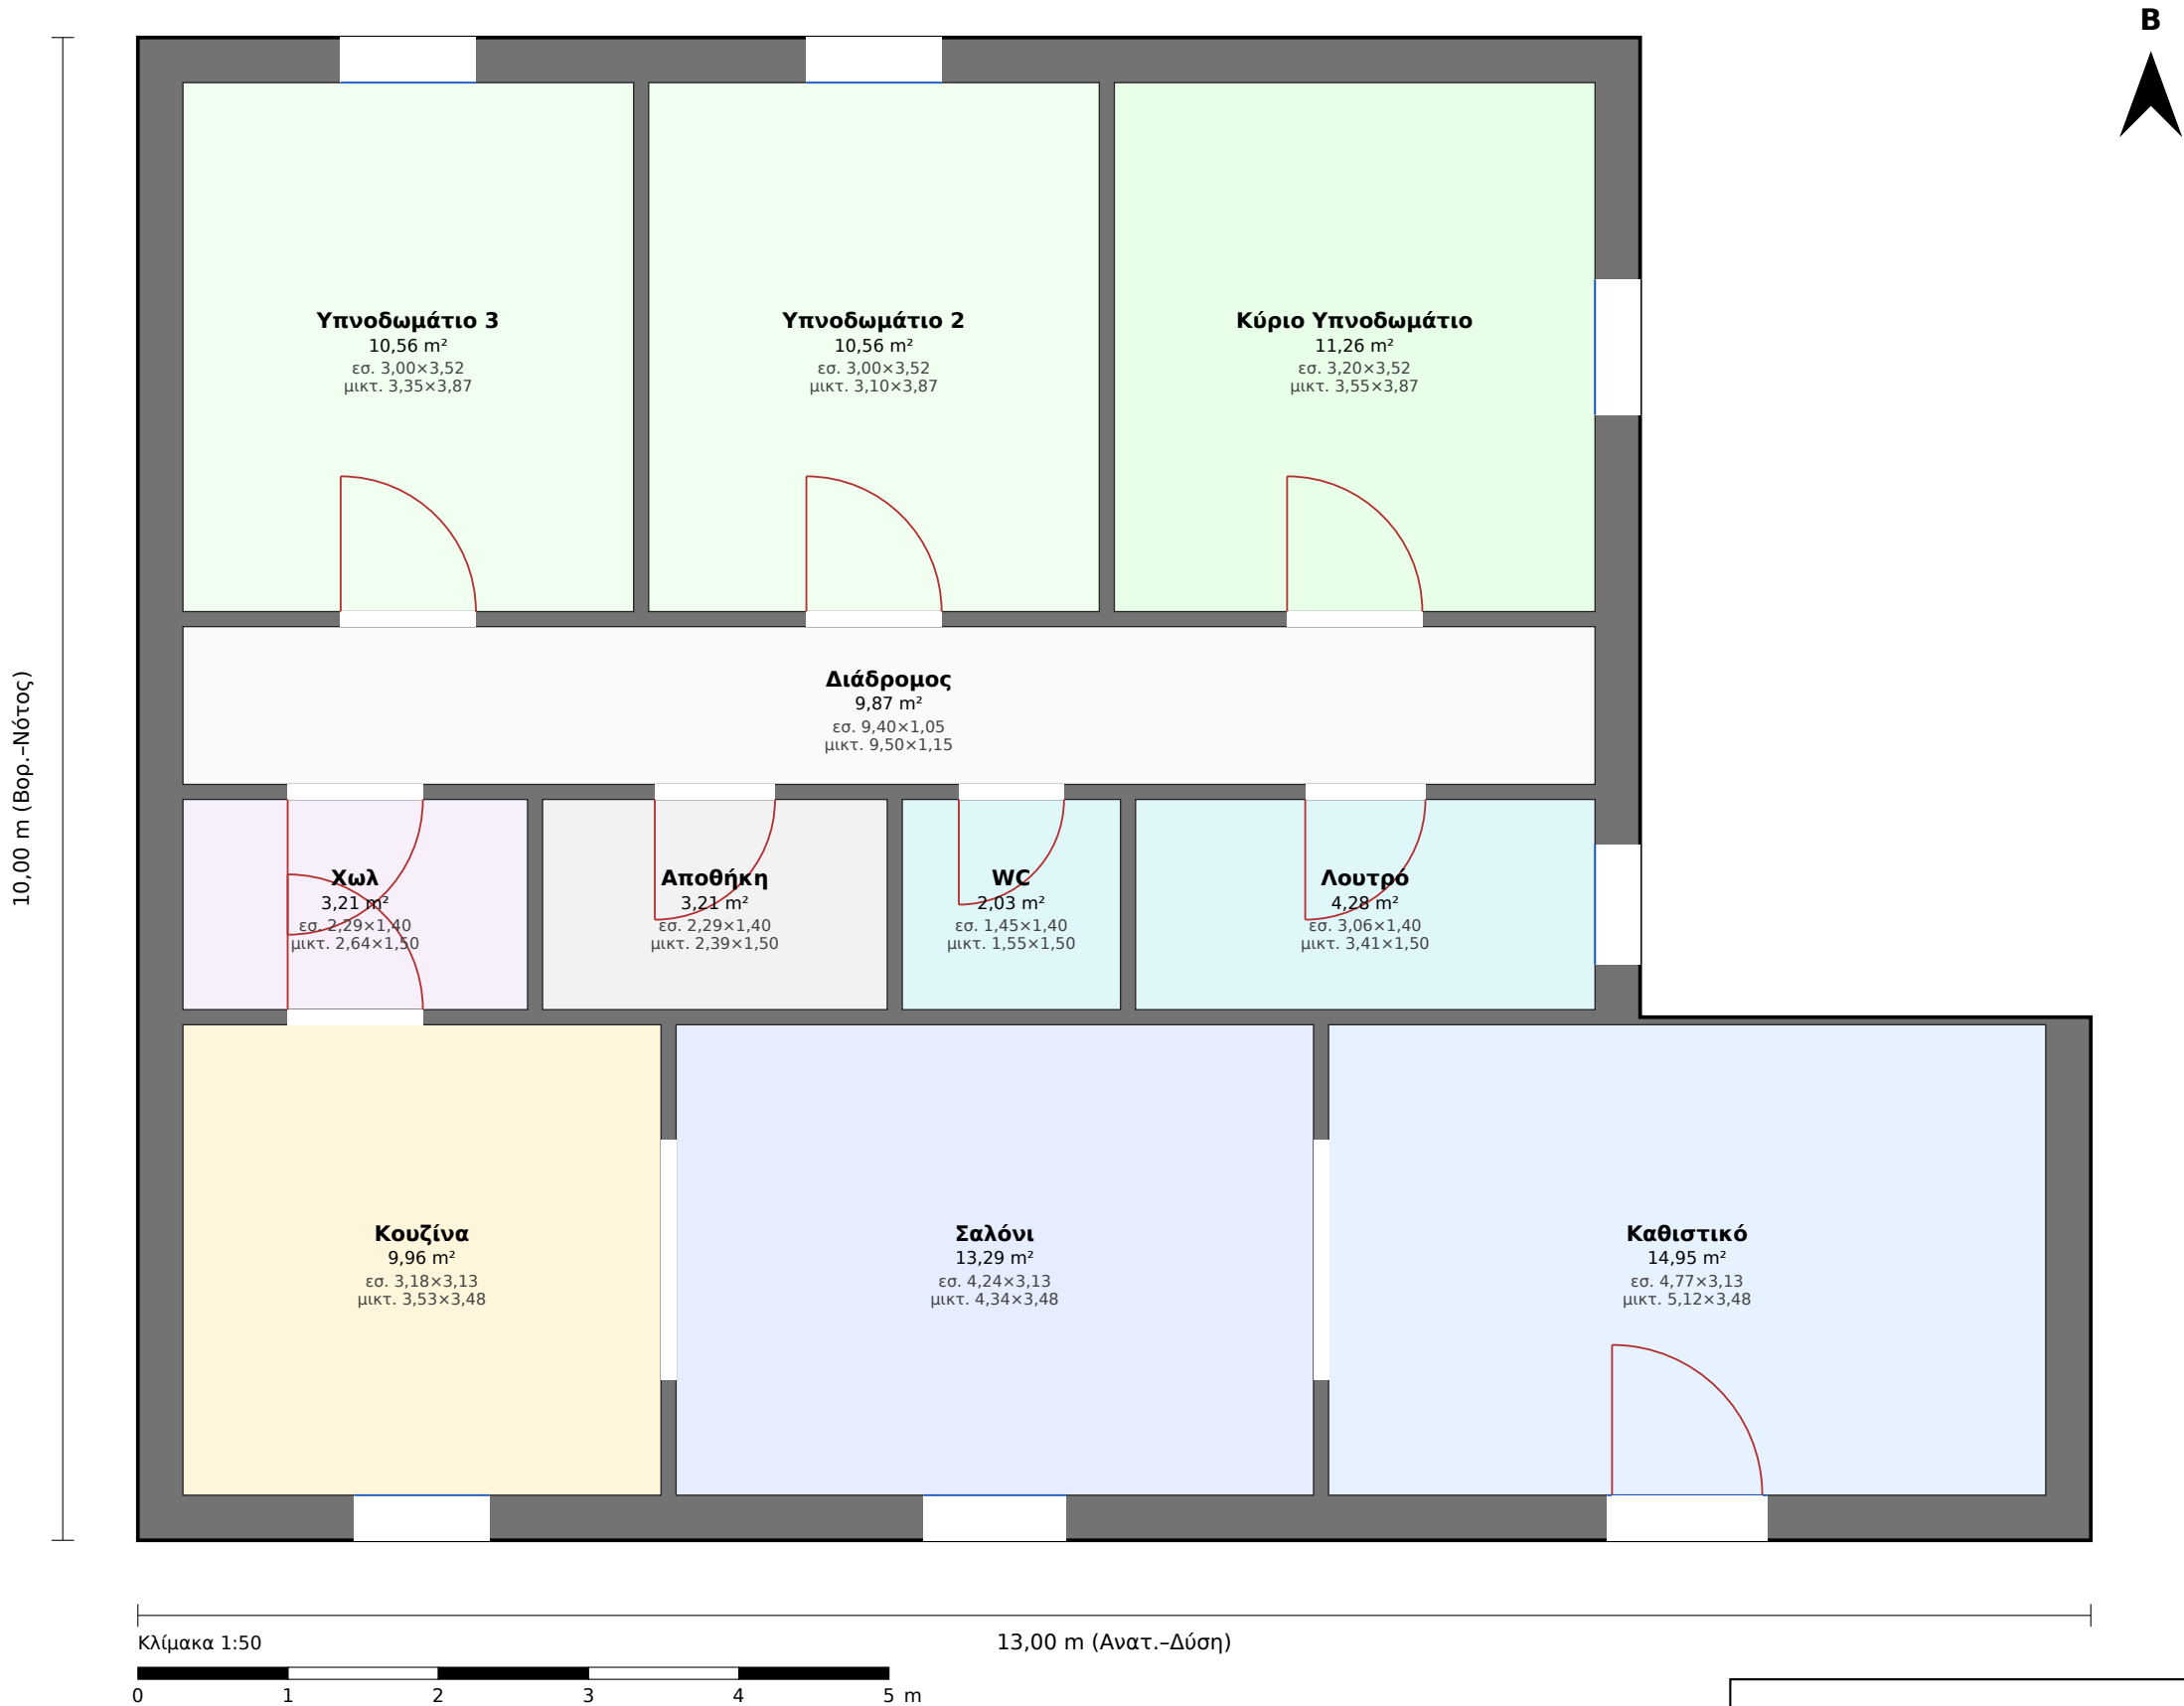

Τεχνικό Γραφείο Μελετών — Γεωργακόπουλος Χρ. / Φουντάς Αθ.
Έργο: Μονοκατοικία Αμαλιάδας
Πρόταση 2 — Ισόγειο
Κλίμακα 1:50 · Μικτό εμβ.: 110,44 m²
Είσοδος: Νότος · Αμαλιάδα, Π.Ε. Ηλείας
Ημερομηνία: 15.08.2026 · Σχεδ.: Γεωργακόπουλος Χρ. (ΑΜ ΤΕΕ 101893)

Μονοκατοικία Αμαλιάδας — Πρόταση 2: Πίνακες χώρων & έλεγχοι

Διαστάσεις: «καθαρές» = εσωτερικές ελεύθερες · «μικτές» = με τοίχους (εξωτ. πλήρες πάχος, εσωτ. μισό). Βορράς: επάνω.

■ **Ισόγειο (μικτό 110,44 m², καθαρό 93,18 m²)**

#	Χώρος	Καθ. εμβ. (m²)	Καθ. Α×Β (m)	Μικτές Α×Β (m)	Ζώνη
1	Κουζίνα	9,96	3,18×3,13	3,53×3,48	κύρια
2	Σαλόνι	13,29	4,24×3,13	4,34×3,48	κύρια
3	Καθιστικό	14,95	4,77×3,13	5,12×3,48	κύρια
4	Υπνοδωμάτιο 3	10,56	3,00×3,52	3,35×3,87	κύρια
5	Υπνοδωμάτιο 2	10,56	3,00×3,52	3,10×3,87	κύρια
6	Κύριο Υπνοδωμάτιο	11,26	3,20×3,52	3,55×3,87	κύρια
7	Χωλ	3,21	2,29×1,40	2,64×1,50	βοηθ.
8	Αποθήκη	3,21	2,29×1,40	2,39×1,50	βοηθ.
9	WC	2,03	1,45×1,40	1,55×1,50	βοηθ.
10	Λουτρό	4,28	3,06×1,40	3,41×1,50	βοηθ.
11	Διάδρομος	9,87	9,40×1,05	9,50×1,15	βοηθ.

Έλεγχος φωτισμού & αερισμού (Κ.Κ. αρ. 20 §5.1.2 / αρ. 21 §5.2)

Χώρος	Εμβ.	Φως≥10%	Υαλοπ.	Αερ.≥5%	Ανοιγ.	Φως	Αερ.
Κουζίνα	10,0	1,00	1,26	0,50	0,63	✓	✓
Σαλόνι	13,3	1,33	1,33	0,66	0,66	✓	✓
Καθιστικό	14,9	1,49	1,49	0,75	0,75	✓	✓
Υπνοδωμάτιο 3	10,6	1,06	1,26	0,53	0,63	✓	✓
Υπνοδωμάτιο 2	10,6	1,06	1,26	0,53	0,63	✓	✓
Κύριο Υπνοδωμάτιο	11,3	1,13	1,26	0,56	0,63	✓	✓
Χωλ	3,2	0,32	0,00	0,16	0,00	✓	✓
Αποθήκη	3,2	0,32	0,00	0,16	0,00	✓	✓
WC	2,0	0,20	0,00	0,10	0,00	✓	✓
Λουτρό	4,3	0,43	1,12	0,21	0,56	✓	✓

→ Όλοι οι χώροι κύριας χρήσης πληρούν φωτισμό ≥10% & αερισμό ≥5%.