


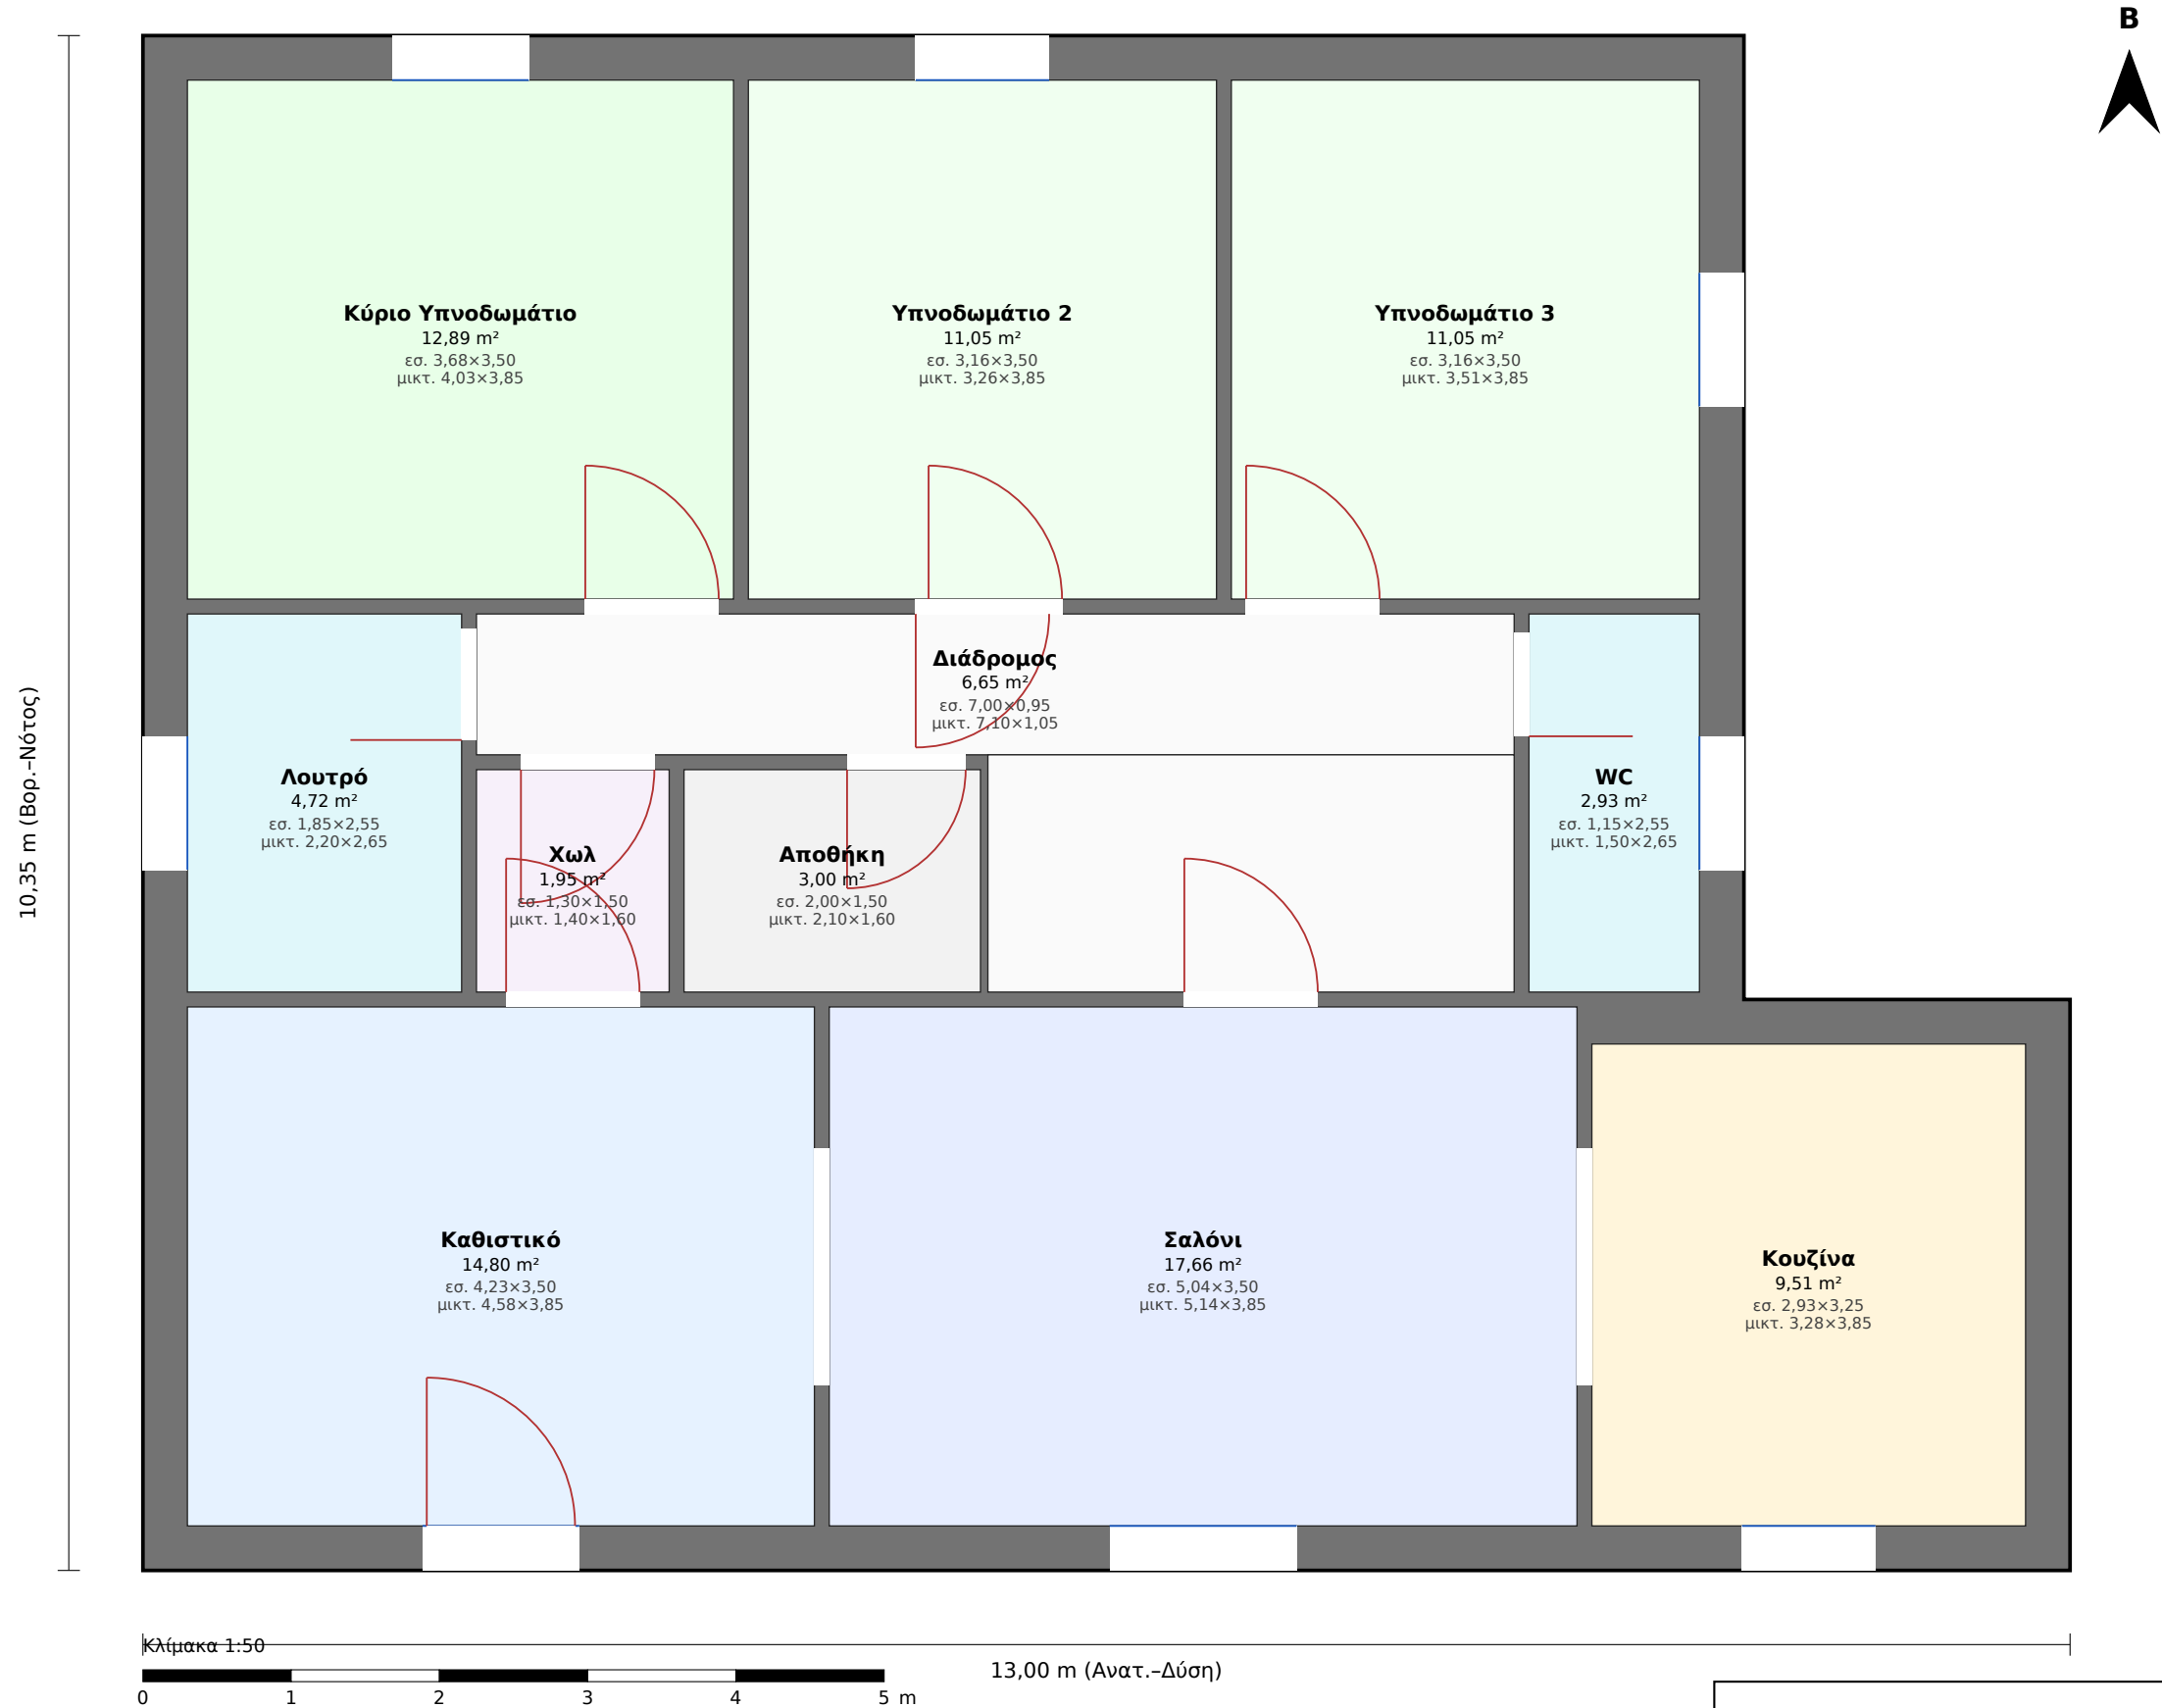

Τεχνικό Γραφείο Μελετών — Γεωργακόπουλος Χρ. / Φουντάς Αθ.
Έργο: Μονοκατοικία Αμαλιάδας
Πρόταση 1 — Ισόγειο
Κλίμακα 1:50 · Μικτό εμβ.: 120,25 m²
Είσοδος: Νότος · Αμαλιάδα, Π.Ε. Ηλείας
Ημερομηνία: 17.08.2026 · Σχεδ.: Γεωργακόπουλος Χρ. (AM TEE 101893)

Μονοκατοικία Αμαλιάδας — Πρόταση 1: Πίνακες χώρων & έλεγχοι

Διαστάσεις: «καθαρές» = εσωτερικές ελεύθερες · «μικτές» = με τοίχους (εξωτ. πλήρες πάχος, εσωτ. μισό). Βορράς: επάνω.



■ Ισόγειο (μικτό 120,25 m², καθαρό 101,90 m²)

#	Χώρος	Καθ. εμβ. (m²)	Καθ. Α×Β (m)	Μικτές Α×Β (m)	Ζώνη
1	Καθιστικό	14,80	4,23×3,50	4,58×3,85	κύρια
2	Σαλόνι	17,66	5,04×3,50	5,14×3,85	κύρια
3	Κουζίνα	9,51	2,93×3,25	3,28×3,85	κύρια
4	Κύριο Υπνοδωμάτιο	12,89	3,68×3,50	4,03×3,85	κύρια
5	Υπνοδωμάτιο 2	11,05	3,16×3,50	3,26×3,85	κύρια
6	Υπνοδωμάτιο 3	11,05	3,16×3,50	3,51×3,85	κύρια
7	Λουτρό	4,72	1,85×2,55	2,20×2,65	βοηθ.
8	Χωλ	1,95	1,30×1,50	1,40×1,60	βοηθ.
9	Αποθήκη	3,00	2,00×1,50	2,10×1,60	βοηθ.
10	WC	2,93	1,15×2,55	1,50×2,65	βοηθ.
11	Διάδρομος	6,65	7,00×0,95	7,10×1,05	βοηθ.
12		5,68	3,55×1,60	3,65×1,70	βοηθ.

Έλεγχος φωτισμού & αερισμού (Κ.Κ. αρ. 20 §5.1.2 / αρ. 21 §5.2)

Χώρος	Εμβ.	Φως≥10%	Υαλοπ.	Αερ.≥5%	Ανοιγ.	Φως	Αερ.
Καθιστικό	14,8	1,48	1,48	0,74	0,74	✓	✓
Σαλόνι	17,7	1,77	1,77	0,88	0,88	✓	✓
Κουζίνα	9,5	0,95	1,26	0,48	0,63	✓	✓
Κύριο Υπνοδωμάτιο	12,9	1,29	1,29	0,64	0,64	✓	✓
Υπνοδωμάτιο 2	11,1	1,11	1,26	0,55	0,63	✓	✓
Υπνοδωμάτιο 3	11,1	1,11	1,26	0,55	0,63	✓	✓
Λουτρό	4,7	0,47	1,26	0,24	0,63	✓	✓
Χωλ	2,0	0,20	0,00	0,10	0,00	✓	✓
Αποθήκη	3,0	0,30	0,00	0,15	0,00	✓	✓
WC	2,9	0,29	1,26	0,15	0,63	✓	✓

→ Όλοι οι χώροι κύριας χρήσης πληρούν φωτισμό ≥10% & αερισμό ≥5%.

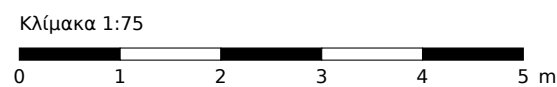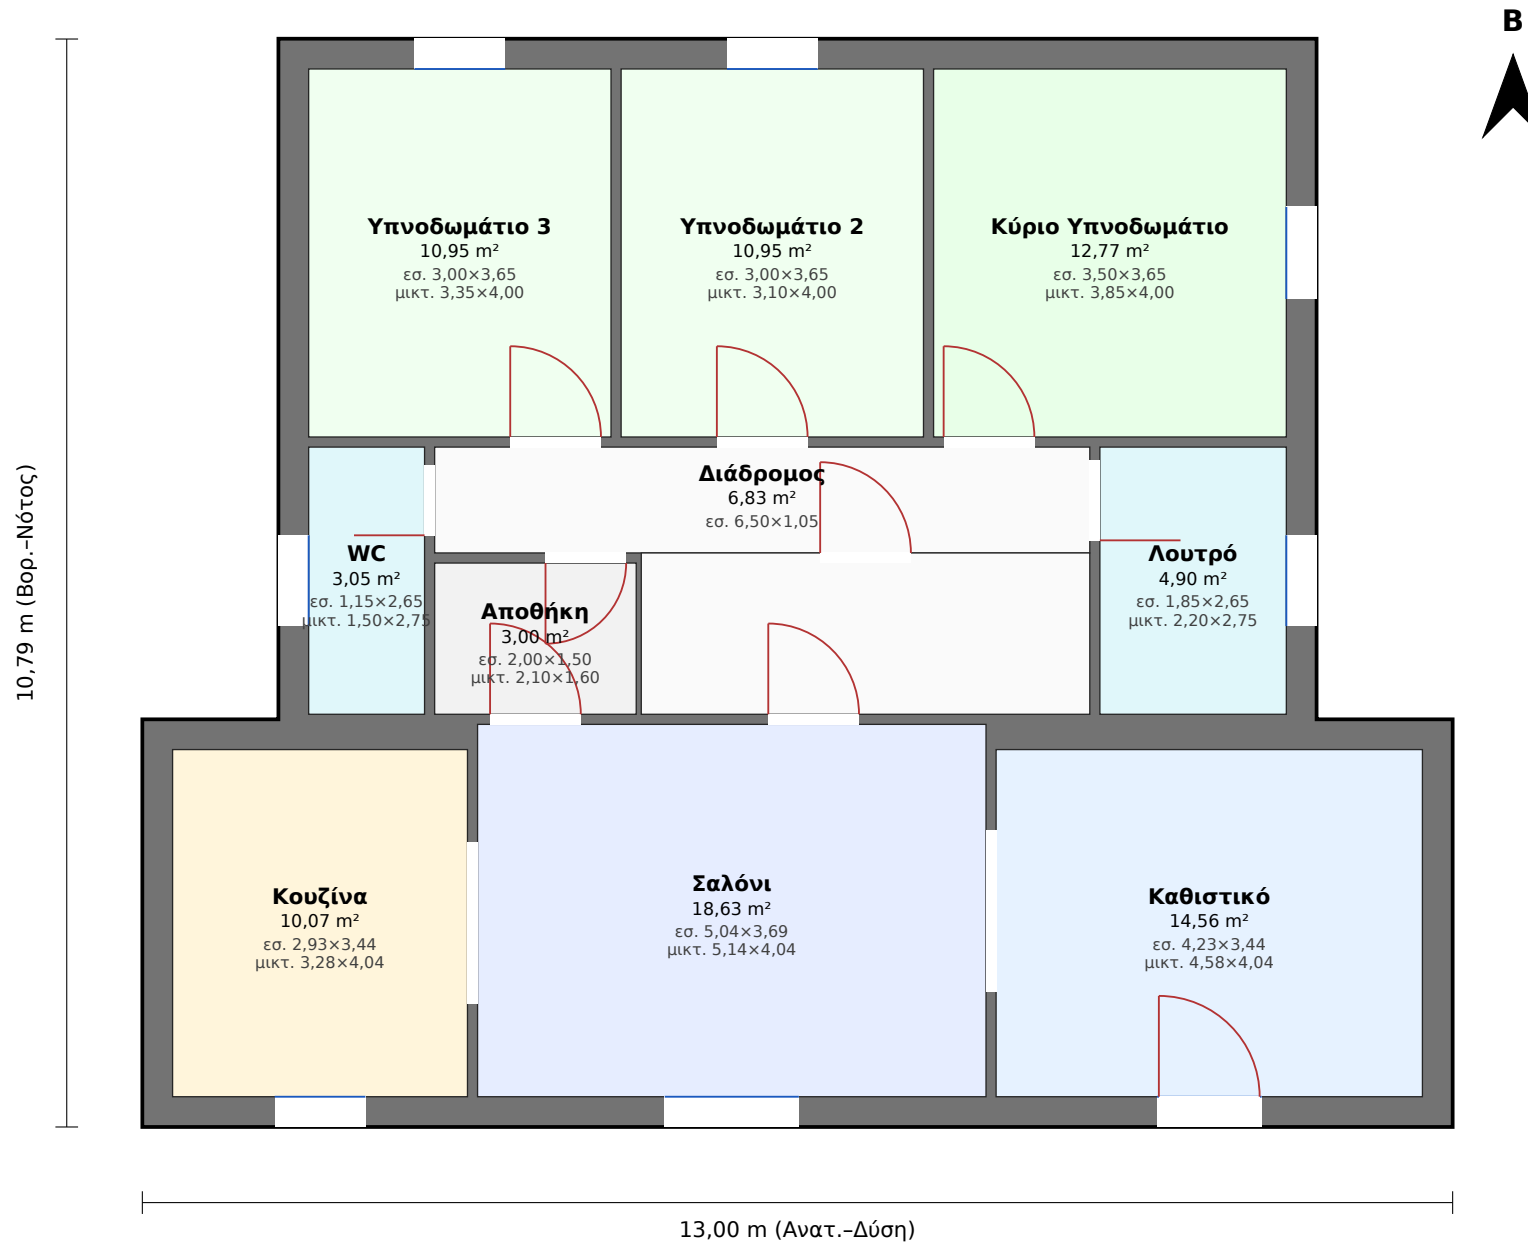

Τεχνικό Γραφείο Μελετών — Γεωργακόπουλος Χρ. / Φουντάς Αθ.
Έργο: Μονοκατοικία Αμαλιάδας
Πρόταση 2 — Ισόγειο
Κλίμακα 1:75 · Μικτό εμβ.: 122,08 m²
Είσοδος: Νότος · Αμαλιάδα, Π.Ε. Ηλείας
Ημερομηνία: 17.08.2026 · Σχεδ.: Γεωργακόπουλος Χρ. (ΑΜ ΤΕΕ 101893)

Μονοκατοικία Αμαλιάδας — Πρόταση 2: Πίνακες χώρων & έλεγχοι

Διαστάσεις: «καθαρές» = εσωτερικές ελεύθερες · «μικτές» = με τοίχους (εξωτ. πλήρες πάχος, εσωτ. μισό). Βορράς: επάνω.

■ **Ισόγειο** (μικτό 122,08 m², καθαρό 102,84 m²)

#	Χώρος	Καθ. εμβ. (m²)	Καθ. Α×Β (m)	Μικτές Α×Β (m)	Ζώνη
1	Κουζίνα	10,07	2,93×3,44	3,28×4,04	κύρια
2	Σαλόνι	18,63	5,04×3,69	5,14×4,04	κύρια
3	Καθιστικό	14,56	4,23×3,44	4,58×4,04	κύρια
4	Υπνοδωμάτιο 3	10,95	3,00×3,65	3,35×4,00	κύρια
5	Υπνοδωμάτιο 2	10,95	3,00×3,65	3,10×4,00	κύρια
6	Κύριο Υπνοδωμάτιο	12,77	3,50×3,65	3,85×4,00	κύρια
7	WC	3,05	1,15×2,65	1,50×2,75	βοηθ.
8	Αποθήκη	3,00	2,00×1,50	2,10×1,60	βοηθ.
9	Λουτρό	4,90	1,85×2,65	2,20×2,75	βοηθ.
10	Διάδρομος	6,83	6,50×1,05	6,60×1,15	βοηθ.
11		7,12	4,45×1,60	4,55×1,70	βοηθ.

Έλεγχος φωτισμού & αερισμού (Κ.Κ. αρ. 20 §5.1.2 / αρ. 21 §5.2)

Χώρος	Εμβ.	Φως≥10%	Υαλοπ.	Αερ.≥5%	Ανοιγ.	Φως	Αερ.
Κουζίνα	10,1	1,01	1,26	0,50	0,63	✓	✓
Σαλόνι	18,6	1,86	1,86	0,93	0,93	✓	✓
Καθιστικό	14,6	1,46	1,46	0,73	0,73	✓	✓
Υπνοδωμάτιο 3	10,9	1,09	1,26	0,55	0,63	✓	✓
Υπνοδωμάτιο 2	10,9	1,09	1,26	0,55	0,63	✓	✓
Κύριο Υπνοδωμάτιο	12,8	1,28	1,28	0,64	0,64	✓	✓
WC	3,0	0,30	1,26	0,15	0,63	✓	✓
Αποθήκη	3,0	0,30	0,00	0,15	0,00	✓	✓
Λουτρό	4,9	0,49	1,26	0,25	0,63	✓	✓

→ Όλοι οι χώροι κύριας χρήσης πληρούν φωτισμό ≥10% & αερισμό ≥5%.



Τεχνικό Γραφείο Μελετών — Γεωργακόπουλος Χρ. / Φουντάς Αθ.
Έργο: Μονοκατοικία Αμαλιάδας
Πρόταση 3 — Ισόγειο
Κλίμακα 1:50 · Μικτό εμβ.: 117,94 m²
Είσοδος: Νότος · Αμαλιάδα, Π.Ε. Ηλείας
Ημερομηνία: 17.08.2026 · Σχεδ.: Γεωργακόπουλος Χρ. (AM TEE 101893)

Μονοκατοικία Αμαλιάδας — Πρόταση 3: Πίνακες χώρων & έλεγχοι

Διαστάσεις: «καθαρές» = εσωτερικές ελεύθερες · «μικτές» = με τοίχους (εξωτ. πλήρες πάχος, εσωτ. μισό). Βορράς: επάνω.

■ Ισόγειο (μικτό 117,94 m², καθαρό 99,44 m²)

#	Χώρος	Καθ. εμβ. (m²)	Καθ. Α×Β (m)	Μικτές Α×Β (m)	Ζώνη
1	Καθιστικό	12,59	3,60×3,50	3,95×3,85	κύρια
2	Σαλόνι	14,33	4,09×3,50	4,19×3,85	κύρια
3	Κουζίνα	9,26	2,85×3,25	3,20×3,85	κύρια
4	Κύριο Υπνοδωμάτιο	13,59	3,88×3,50	4,23×3,85	κύρια
5	Υπνοδωμάτιο 2	11,65	3,33×3,50	3,43×3,85	κύρια
6	Υπνοδωμάτιο 3	11,65	3,33×3,50	3,68×3,85	κύρια
7	Λουτρό	4,35	1,85×2,35	2,20×2,70	βοηθ.
8	Χωλ	1,95	1,30×1,50	1,40×1,60	βοηθ.
9	Αποθήκη	3,00	2,00×1,50	2,10×1,60	βοηθ.
10	WC	2,99	1,15×2,60	1,50×2,70	βοηθ.
11	Διάδρομος	7,54	7,54×1,00	7,64×1,10	βοηθ.
12		6,54	4,09×1,60	4,19×1,70	βοηθ.

Έλεγχος φωτισμού & αερισμού (Κ.Κ. αρ. 20 §5.1.2 / αρ. 21 §5.2)

Χώρος	Εμβ.	Φως≥10%	Υαλοπ.	Αερ.≥5%	Ανοιγ.	Φως	Αερ.
Καθιστικό	12,6	1,26	1,26	0,63	0,63	✓	✓
Σαλόνι	14,3	1,43	1,43	0,72	0,72	✓	✓
Κουζίνα	9,3	0,93	1,26	0,46	0,63	✓	✓
Κύριο Υπνοδωμάτιο	13,6	1,36	1,36	0,68	0,68	✓	✓
Υπνοδωμάτιο 2	11,6	1,16	1,26	0,58	0,63	✓	✓
Υπνοδωμάτιο 3	11,6	1,16	1,26	0,58	0,63	✓	✓
Λουτρό	4,3	0,43	1,26	0,22	0,63	✓	✓
Χωλ	2,0	0,20	0,00	0,10	0,00	✓	✓
Αποθήκη	3,0	0,30	0,00	0,15	0,00	✓	✓
WC	3,0	0,30	1,26	0,15	0,63	✓	✓

→ Όλοι οι χώροι κύριας χρήσης πληρούν φωτισμό ≥10% & αερισμό ≥5%.