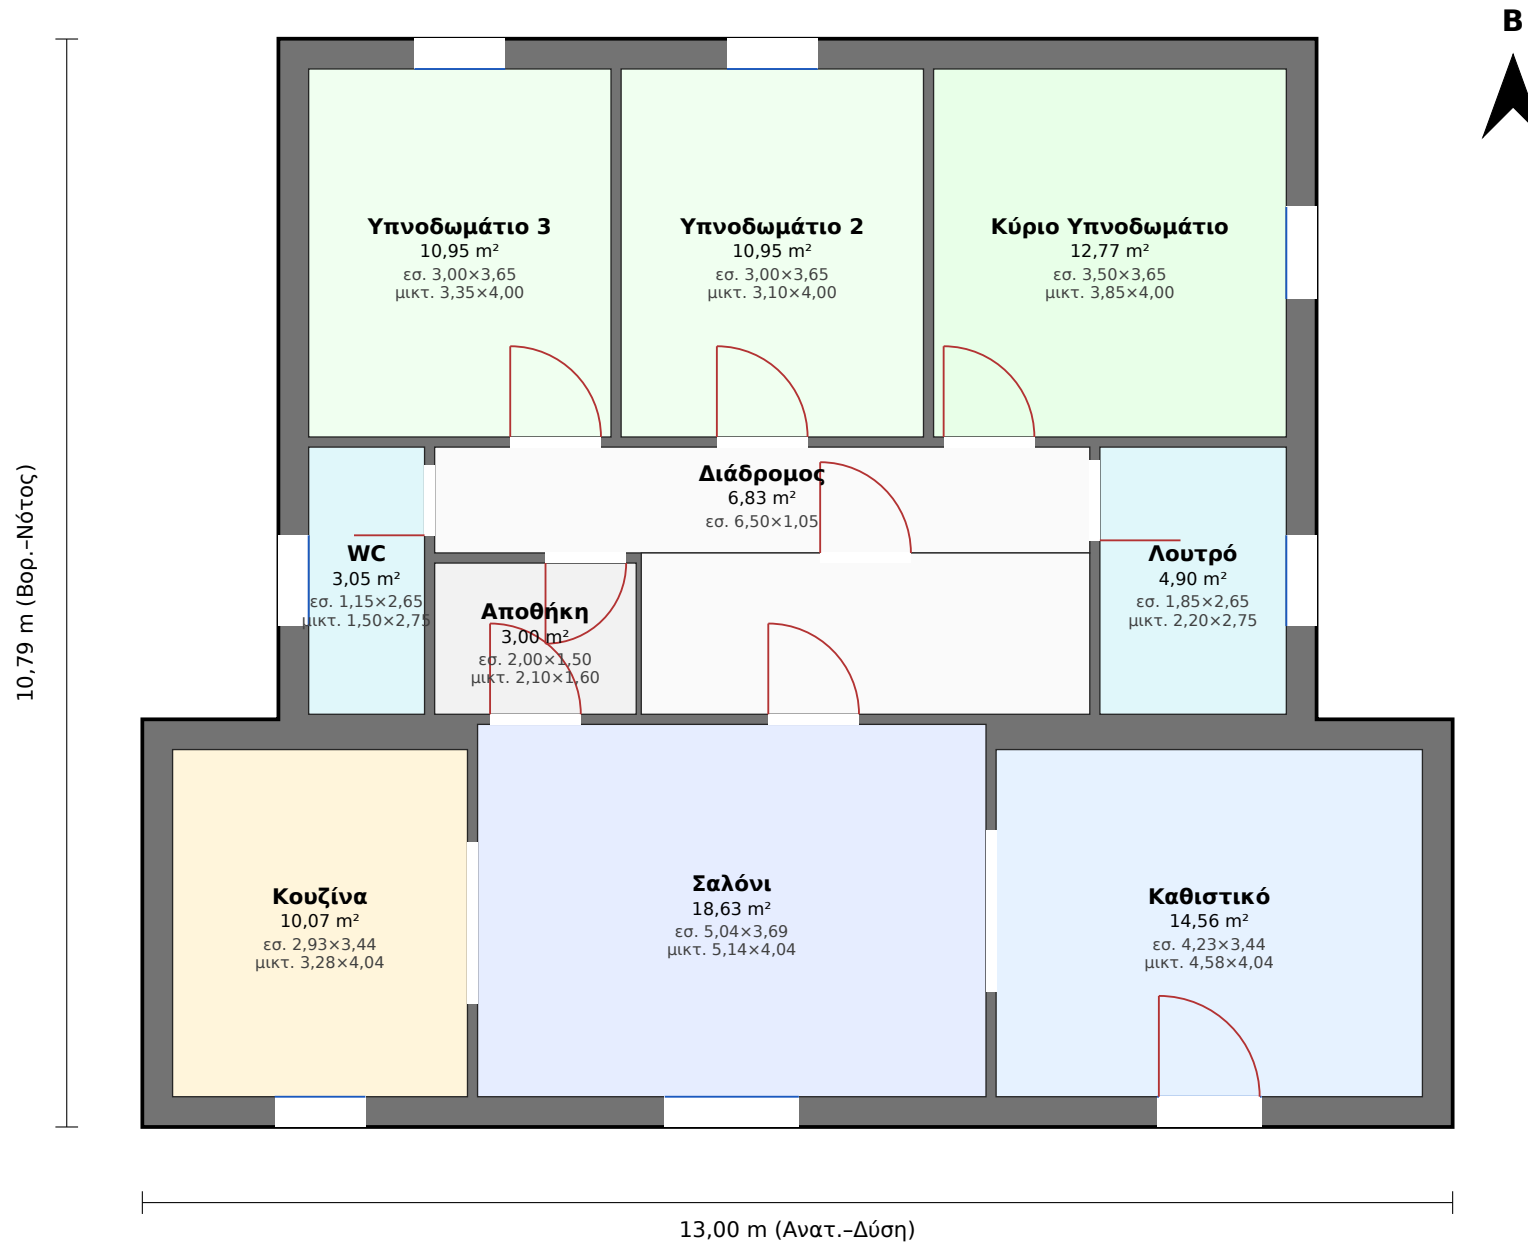


**Τεχνικό Γραφείο Μελετών — Γεωργακόπουλος Χρ. / Φουντάς Αθ.**  
Έργο: Μονοκατοικία Αμαλιάδας  
Πρόταση 2 — Ισόγειο  
Κλίμακα 1:75 · Μικτό εμβ.: 122,08 m<sup>2</sup>  
Είσοδος: Νότος · Αμαλιάδα, Π.Ε. Ηλείας  
Ημερομηνία: 17.08.2026 · Σχεδ.: Γεωργακόπουλος Χρ. (ΑΜ ΤΕΕ 101893)

## Μονοκατοικία Αμαλιάδας — Πρόταση 2: Πίνακες χώρων & έλεγχοι

Διαστάσεις: «καθαρές» = εσωτερικές ελεύθερες · «μικτές» = με τοίχους (εξωτ. πλήρες πάχος, εσωτ. μισό). Βορράς: επάνω.

■ **Ισόγειο** (μικτό 122,08 m², καθαρό 102,84 m²)

| #  | Χώρος             | Καθ. εμβ. (m²) | Καθ. Α×Β (m) | Μικτές Α×Β (m) | Ζώνη  |
|----|-------------------|----------------|--------------|----------------|-------|
| 1  | Κουζίνα           | 10,07          | 2,93×3,44    | 3,28×4,04      | κύρια |
| 2  | Σαλόνι            | 18,63          | 5,04×3,69    | 5,14×4,04      | κύρια |
| 3  | Καθιστικό         | 14,56          | 4,23×3,44    | 4,58×4,04      | κύρια |
| 4  | Υπνοδωμάτιο 3     | 10,95          | 3,00×3,65    | 3,35×4,00      | κύρια |
| 5  | Υπνοδωμάτιο 2     | 10,95          | 3,00×3,65    | 3,10×4,00      | κύρια |
| 6  | Κύριο Υπνοδωμάτιο | 12,77          | 3,50×3,65    | 3,85×4,00      | κύρια |
| 7  | WC                | 3,05           | 1,15×2,65    | 1,50×2,75      | βοηθ. |
| 8  | Αποθήκη           | 3,00           | 2,00×1,50    | 2,10×1,60      | βοηθ. |
| 9  | Λουτρό            | 4,90           | 1,85×2,65    | 2,20×2,75      | βοηθ. |
| 10 | Διάδρομος         | 6,83           | 6,50×1,05    | 6,60×1,15      | βοηθ. |
| 11 |                   | 7,12           | 4,45×1,60    | 4,55×1,70      | βοηθ. |

### Έλεγχος φωτισμού & αερισμού (Κ.Κ. αρ. 20 §5.1.2 / αρ. 21 §5.2)

| Χώρος             | Εμβ. | Φως≥10% | Υαλοπ. | Αερ.≥5% | Ανοιγ. | Φως | Αερ. |
|-------------------|------|---------|--------|---------|--------|-----|------|
| Κουζίνα           | 10,1 | 1,01    | 1,26   | 0,50    | 0,63   | ✓   | ✓    |
| Σαλόνι            | 18,6 | 1,86    | 1,86   | 0,93    | 0,93   | ✓   | ✓    |
| Καθιστικό         | 14,6 | 1,46    | 1,46   | 0,73    | 0,73   | ✓   | ✓    |
| Υπνοδωμάτιο 3     | 10,9 | 1,09    | 1,26   | 0,55    | 0,63   | ✓   | ✓    |
| Υπνοδωμάτιο 2     | 10,9 | 1,09    | 1,26   | 0,55    | 0,63   | ✓   | ✓    |
| Κύριο Υπνοδωμάτιο | 12,8 | 1,28    | 1,28   | 0,64    | 0,64   | ✓   | ✓    |
| WC                | 3,0  | 0,30    | 1,26   | 0,15    | 0,63   | ✓   | ✓    |
| Αποθήκη           | 3,0  | 0,30    | 0,00   | 0,15    | 0,00   | ✓   | ✓    |
| Λουτρό            | 4,9  | 0,49    | 1,26   | 0,25    | 0,63   | ✓   | ✓    |

→ Όλοι οι χώροι κύριας χρήσης πληρούν φωτισμό ≥10% & αερισμό ≥5%.