


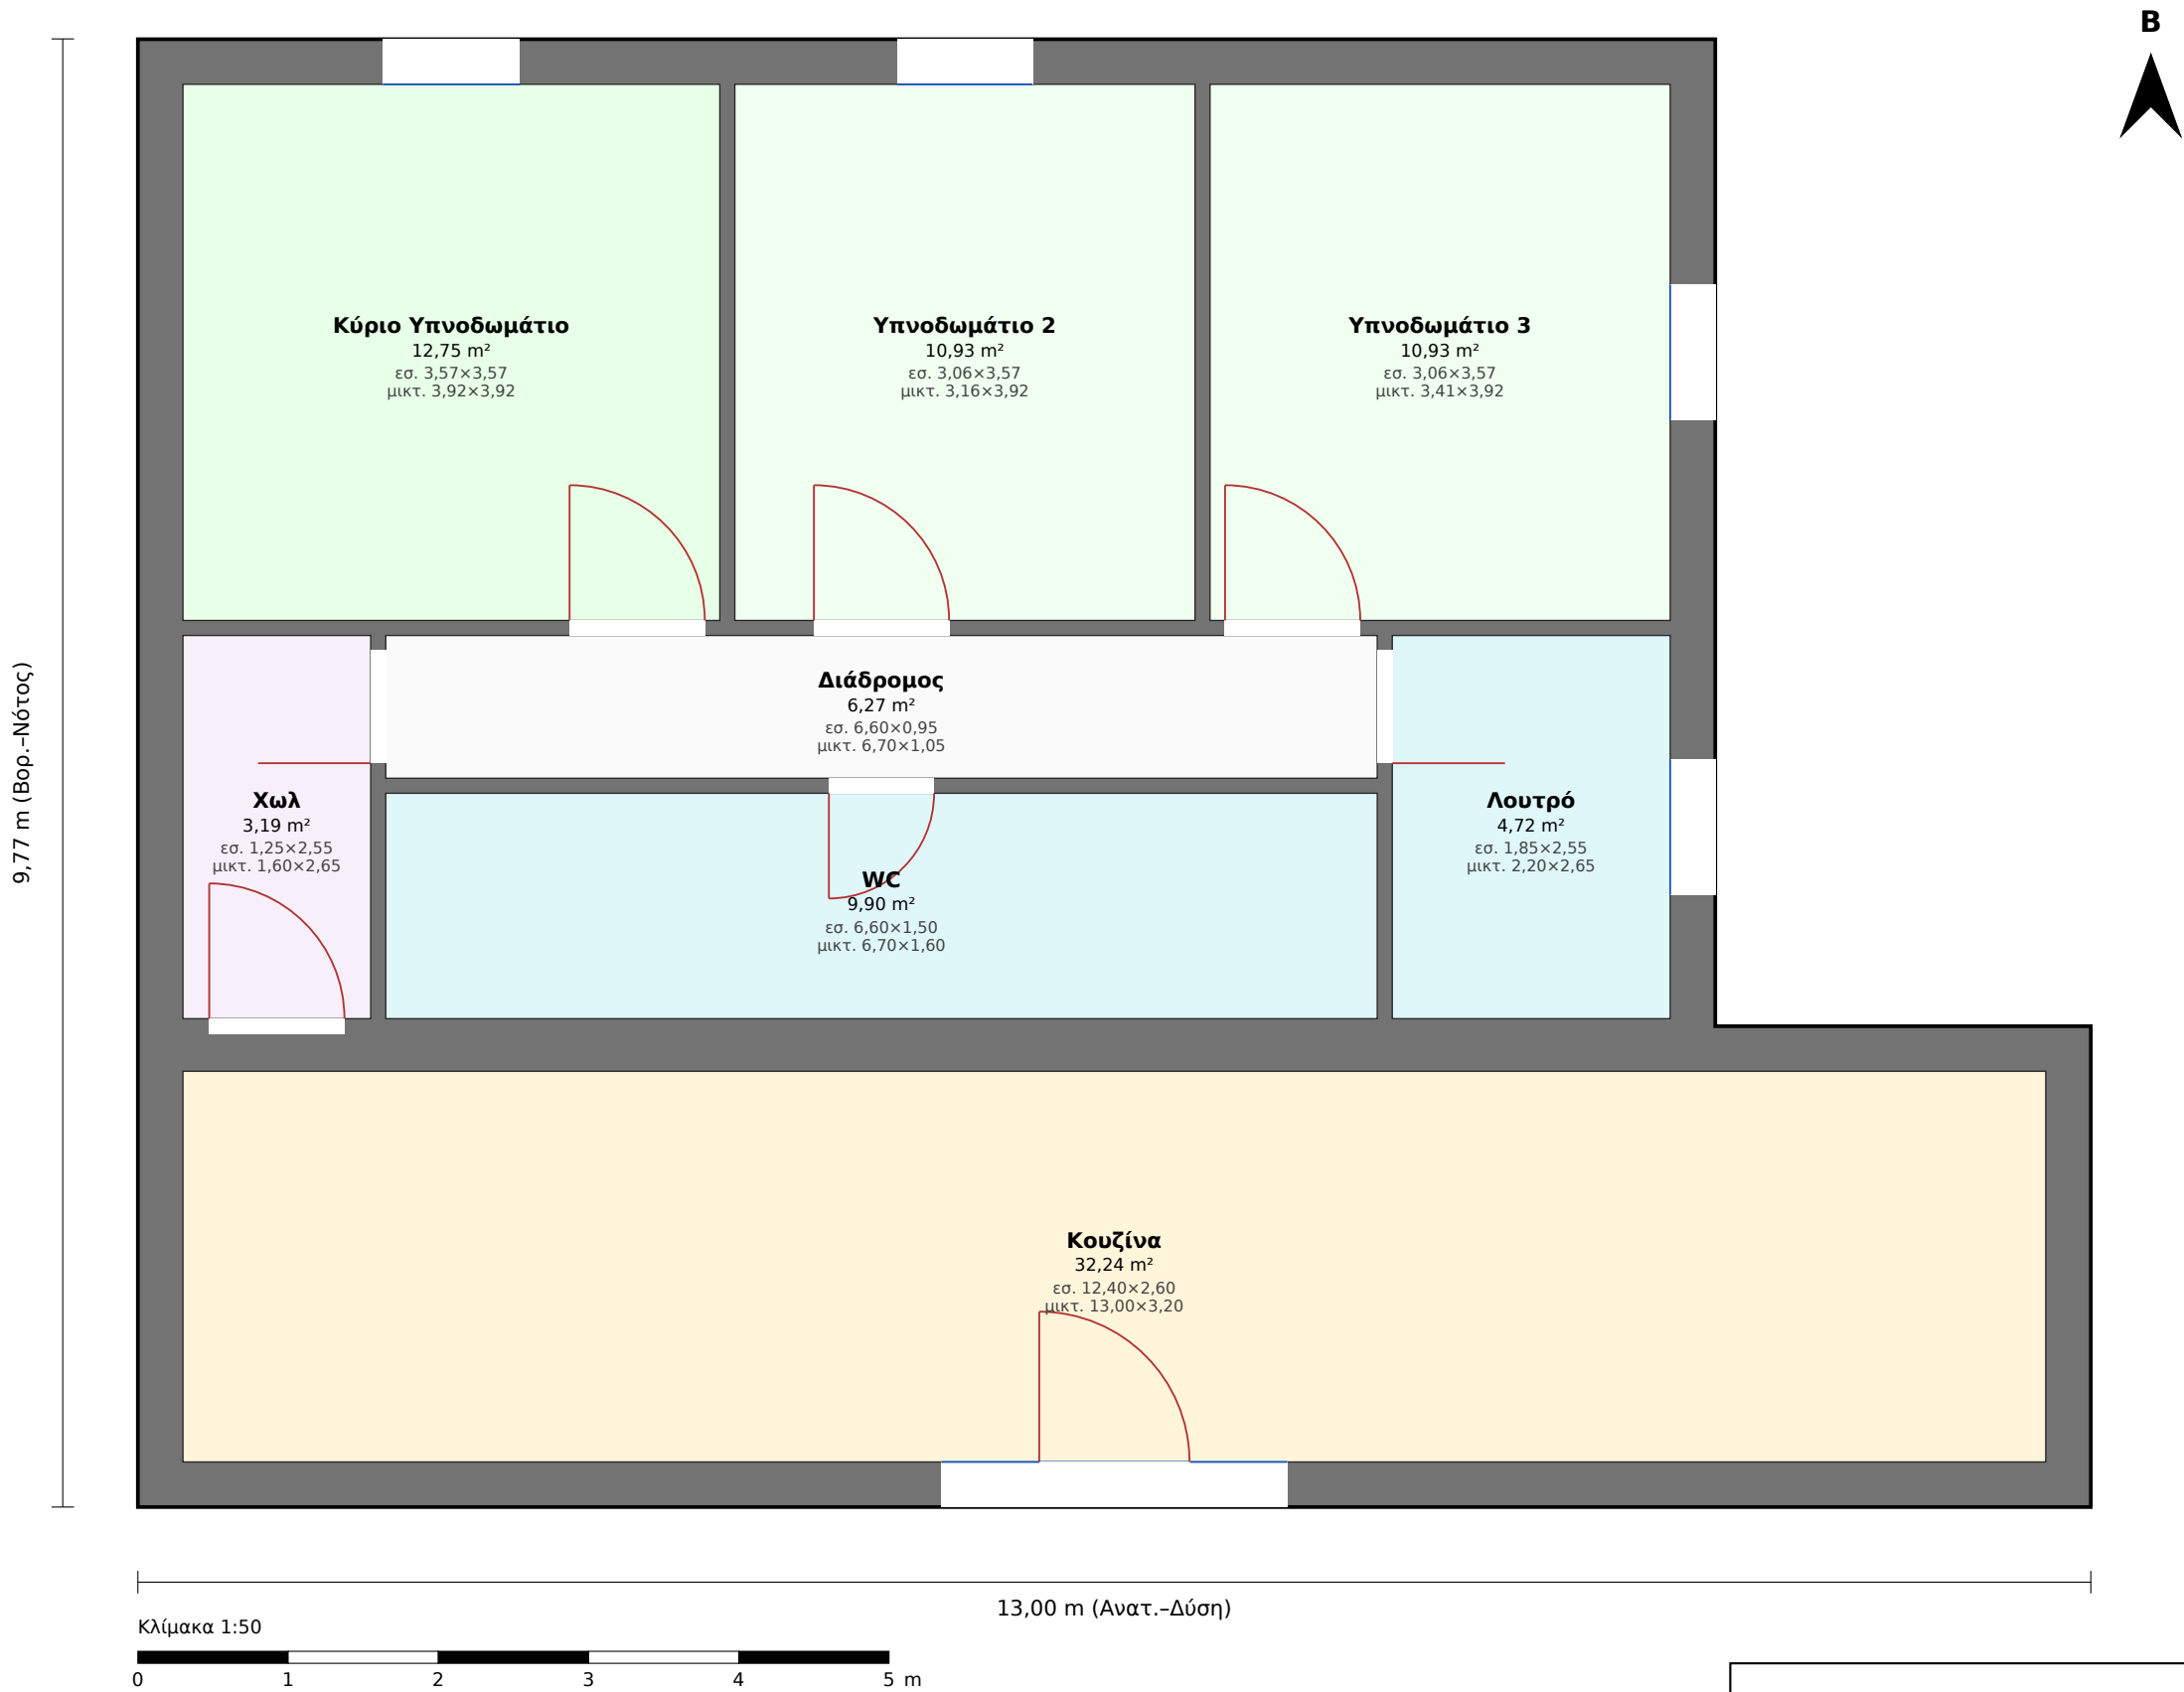

Τεχνικό Γραφείο Μελετών — Γεωργακόπουλος Χρ. / Φουντάς Αθ.
Έργο: Κατοικία
Πρόταση 1 — Ισόγειο
Κλίμακα 1:50 · Μικτό εμβ.: 110,56 m²
Είσοδος: Νότος · Αμαλιάδα, Π.Ε. Ηλείας
Ημερομηνία: 16.08.2026 · Σχεδ.: Γεωργακόπουλος Χρ. (ΑΜ ΤΕΕ 101893)

Κατοικία — Πρόταση 1: Πίνακες χώρων & έλεγχοι

Διαστάσεις: «καθαρές» = εσωτερικές ελεύθερες · «μικτές» = με τοίχους (εξωτ. πλήρες πάχος, εσωτ. μισό). Βορράς: επάνω.


■ Ισόγειο (μικτό 110,56 m², καθαρό 90,92 m²)

#	Χώρος	Καθ. εμβ. (m²)	Καθ. Α×Β (m)	Μικτές Α×Β (m)	Ζώνη
1	Κουζίνα	32,24	12,40×2,60	13,00×3,20	κύρια
2	Κύριο Υπνοδωμάτιο	12,75	3,57×3,57	3,92×3,92	κύρια
3	Υπνοδωμάτιο 2	10,93	3,06×3,57	3,16×3,92	κύρια
4	Υπνοδωμάτιο 3	10,93	3,06×3,57	3,41×3,92	κύρια
5	Χωλ	3,19	1,25×2,55	1,60×2,65	βοηθ.
6	WC	9,90	6,60×1,50	6,70×1,60	βοηθ.
7	Λουτρό	4,72	1,85×2,55	2,20×2,65	βοηθ.
8	Διάδρομος	6,27	6,60×0,95	6,70×1,05	βοηθ.

Έλεγχος φωτισμού & αερισμού (Κ.Κ. αρ. 20 §5.1.2 / αρ. 21 §5.2)

Χώρος	Εμβ.	Φως≥10%	Υαλοπ.	Αερ.≥5%	Ανοιγ.	Φως	Αερ.
Κουζίνα	32,2	3,22	3,22	1,61	1,61	✓	✓
Κύριο Υπνοδωμάτιο	12,8	1,28	1,28	0,64	0,64	✓	✓
Υπνοδωμάτιο 2	10,9	1,09	1,26	0,55	0,63	✓	✓
Υπνοδωμάτιο 3	10,9	1,09	1,26	0,55	0,63	✓	✓
Χωλ	3,2	0,32	0,00	0,16	0,00	✓	✓
WC	9,9	0,99	0,00	0,50	0,00	✓	✓
Λουτρό	4,7	0,47	1,26	0,24	0,63	✓	✓

→ Όλοι οι χώροι κύριας χρήσης πληρούν φωτισμό ≥10% & αερισμό ≥5%.

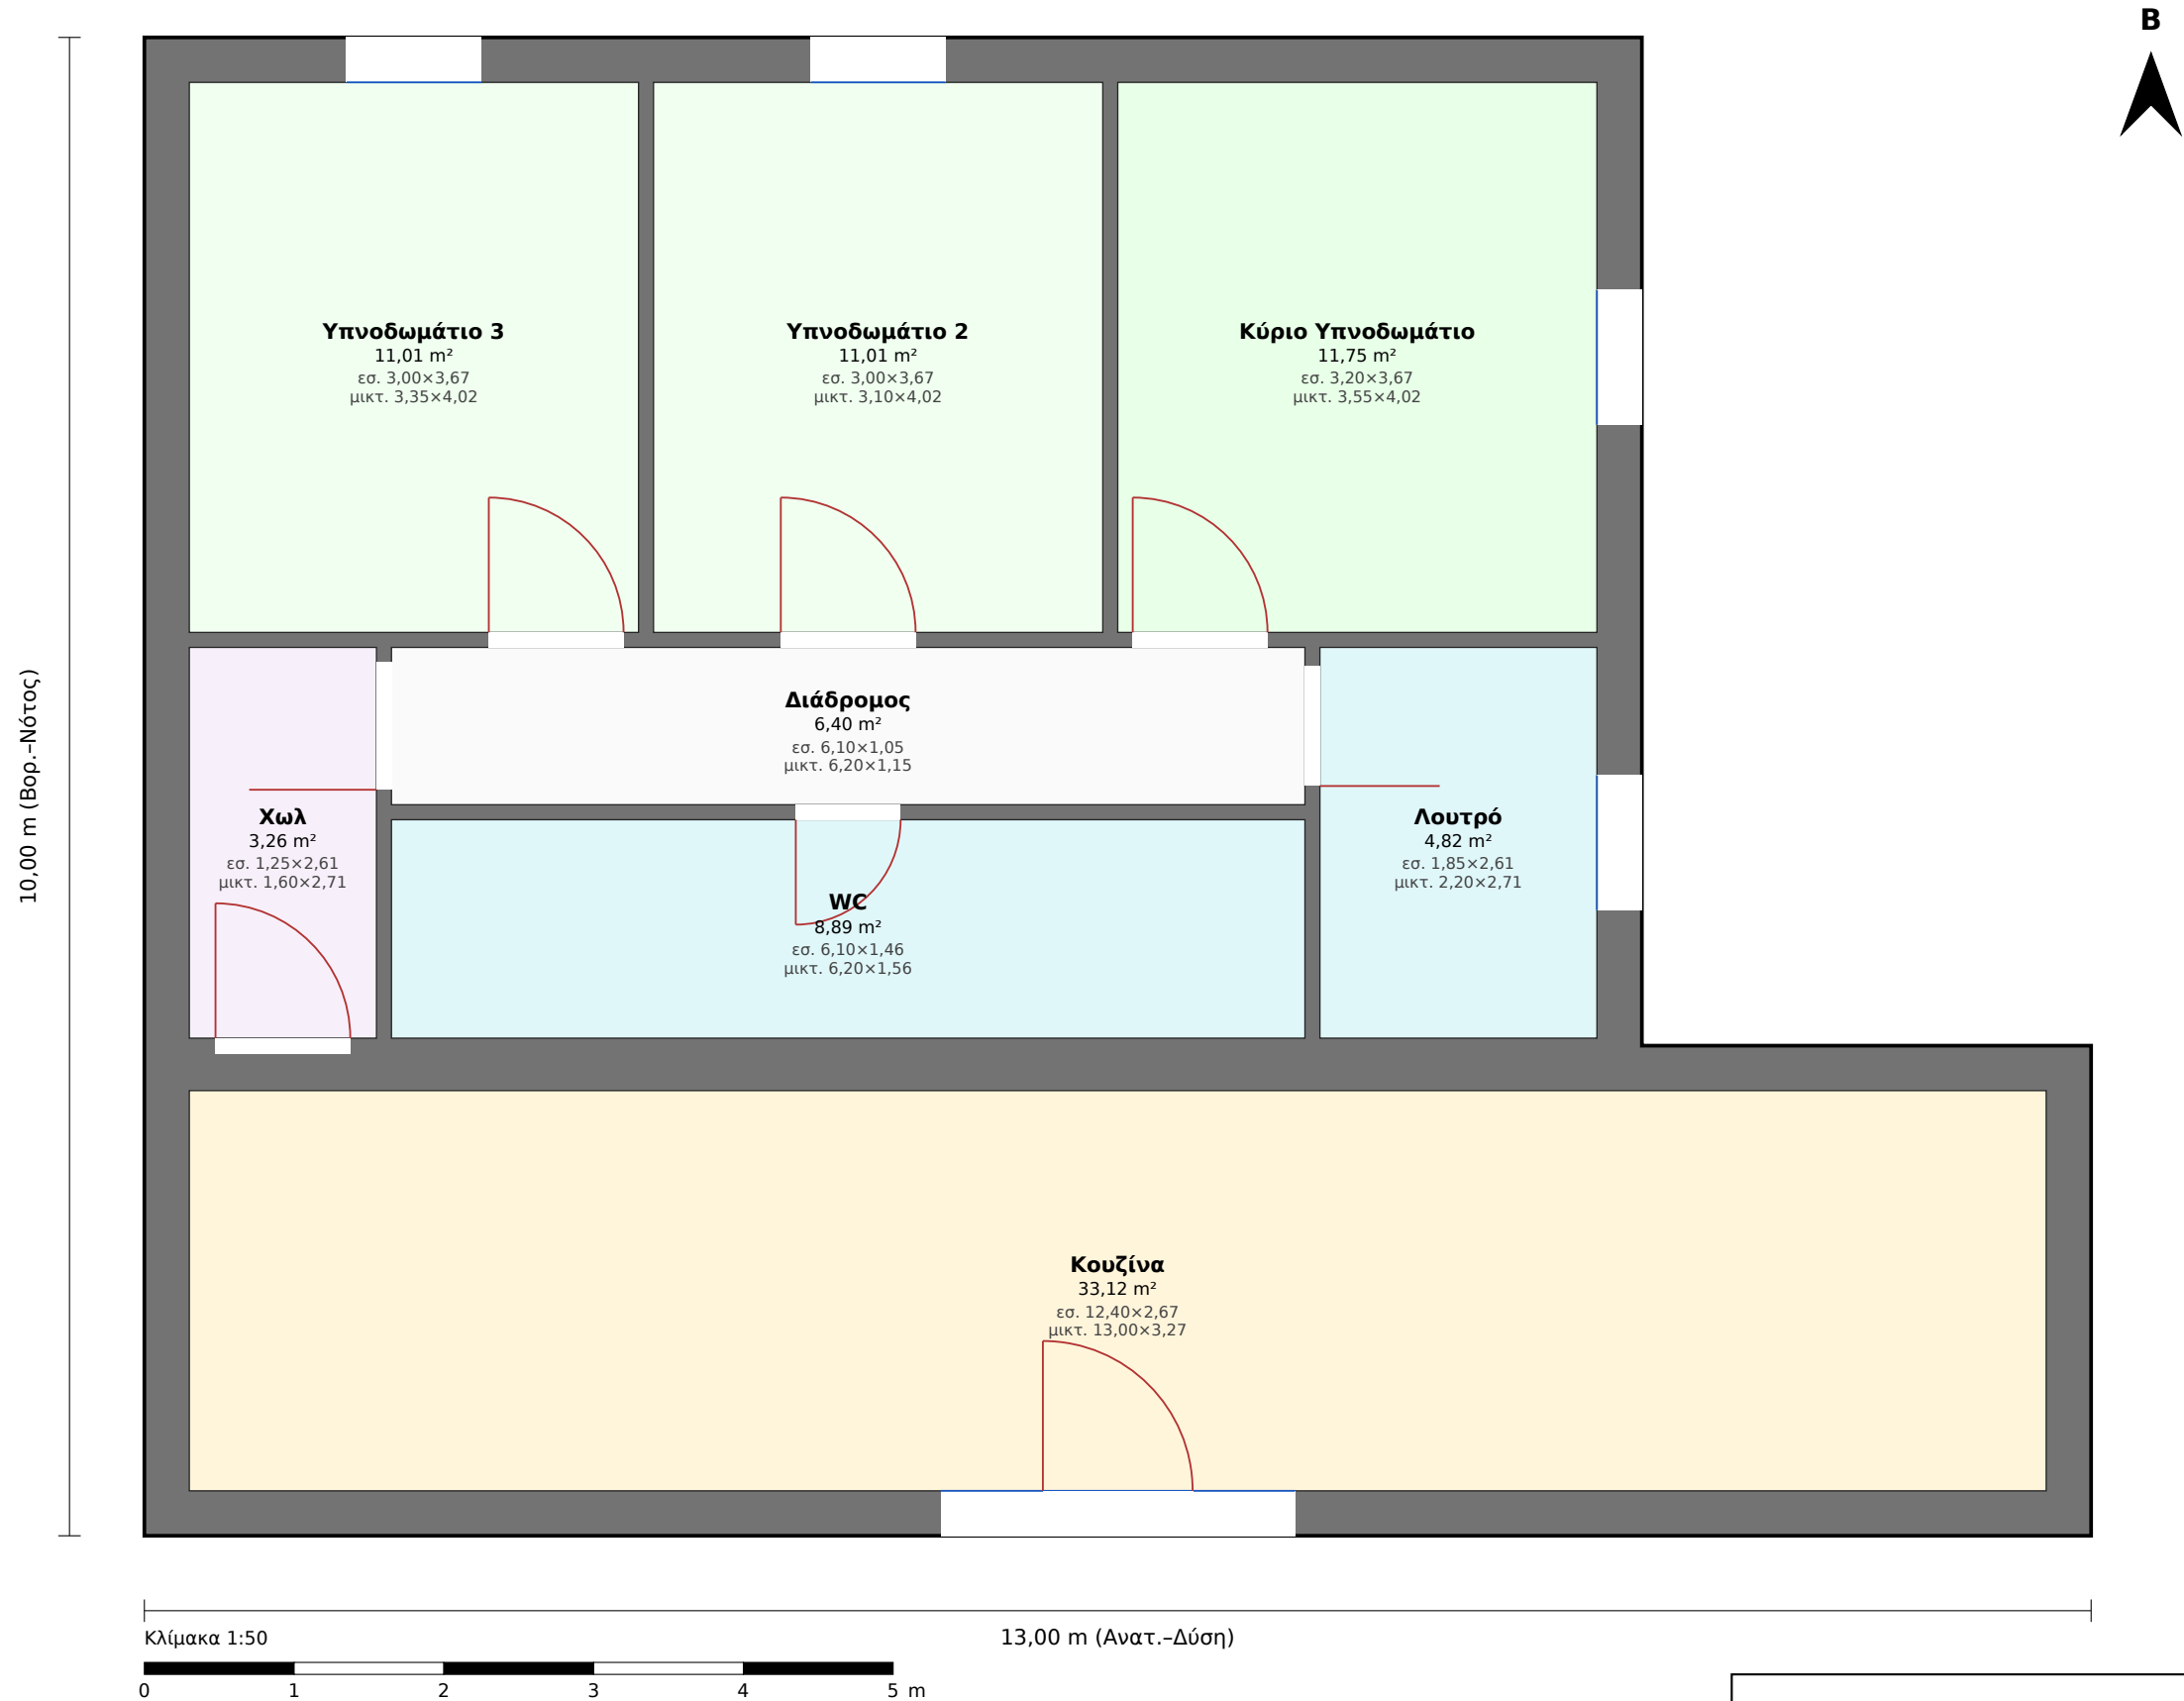

Τεχνικό Γραφείο Μελετών — Γεωργακόπουλος Χρ. / Φουντάς Αθ.
Έργο: Κατοικία
Πρόταση 2 — Ισόγειο
Κλίμακα 1:50 · Μικτό εμβ.: 109,81 m²
Είσοδος: Νότος · Αμαλιάδα, Π.Ε. Ηλείας
Ημερομηνία: 16.08.2026 · Σχεδ.: Γεωργακόπουλος Χρ. (ΑΜ ΤΕΕ 101893)

Κατοικία — Πρόταση 2: Πίνακες χώρων & έλεγχοι

Διαστάσεις: «καθαρές» = εσωτερικές ελεύθερες · «μικτές» = με τοίχους (εξωτ. πλήρες πάχος, εσωτ. μισό). Βορράς: επάνω.


■ Ισόγειο (μικτό 109,81 m², καθαρό 90,28 m²)

#	Χώρος	Καθ. εμβ. (m²)	Καθ. Α×Β (m)	Μικτές Α×Β (m)	Ζώνη
1	Κουζίνα	33,12	12,40×2,67	13,00×3,27	κύρια
2	Υπνοδωμάτιο 3	11,01	3,00×3,67	3,35×4,02	κύρια
3	Υπνοδωμάτιο 2	11,01	3,00×3,67	3,10×4,02	κύρια
4	Κύριο Υπνοδωμάτιο	11,75	3,20×3,67	3,55×4,02	κύρια
5	Χωλ	3,26	1,25×2,61	1,60×2,71	βοηθ.
6	WC	8,89	6,10×1,46	6,20×1,56	βοηθ.
7	Λουτρό	4,82	1,85×2,61	2,20×2,71	βοηθ.
8	Διάδρομος	6,40	6,10×1,05	6,20×1,15	βοηθ.

Έλεγχος φωτισμού & αερισμού (Κ.Κ. αρ. 20 §5.1.2 / αρ. 21 §5.2)

Χώρος	Εμβ.	Φως≥10%	Υαλοπ.	Αερ.≥5%	Ανοιγ.	Φως	Αερ.
Κουζίνα	33,1	3,31	3,31	1,66	1,66	✓	✓
Υπνοδωμάτιο 3	11,0	1,10	1,26	0,55	0,63	✓	✓
Υπνοδωμάτιο 2	11,0	1,10	1,26	0,55	0,63	✓	✓
Κύριο Υπνοδωμάτιο	11,7	1,17	1,26	0,59	0,63	✓	✓
Χωλ	3,3	0,33	0,00	0,16	0,00	✓	✓
WC	8,9	0,89	0,00	0,44	0,00	✓	✓
Λουτρό	4,8	0,48	1,26	0,24	0,63	✓	✓

→ Όλοι οι χώροι κύριας χρήσης πληρούν φωτισμό ≥10% & αερισμό ≥5%.

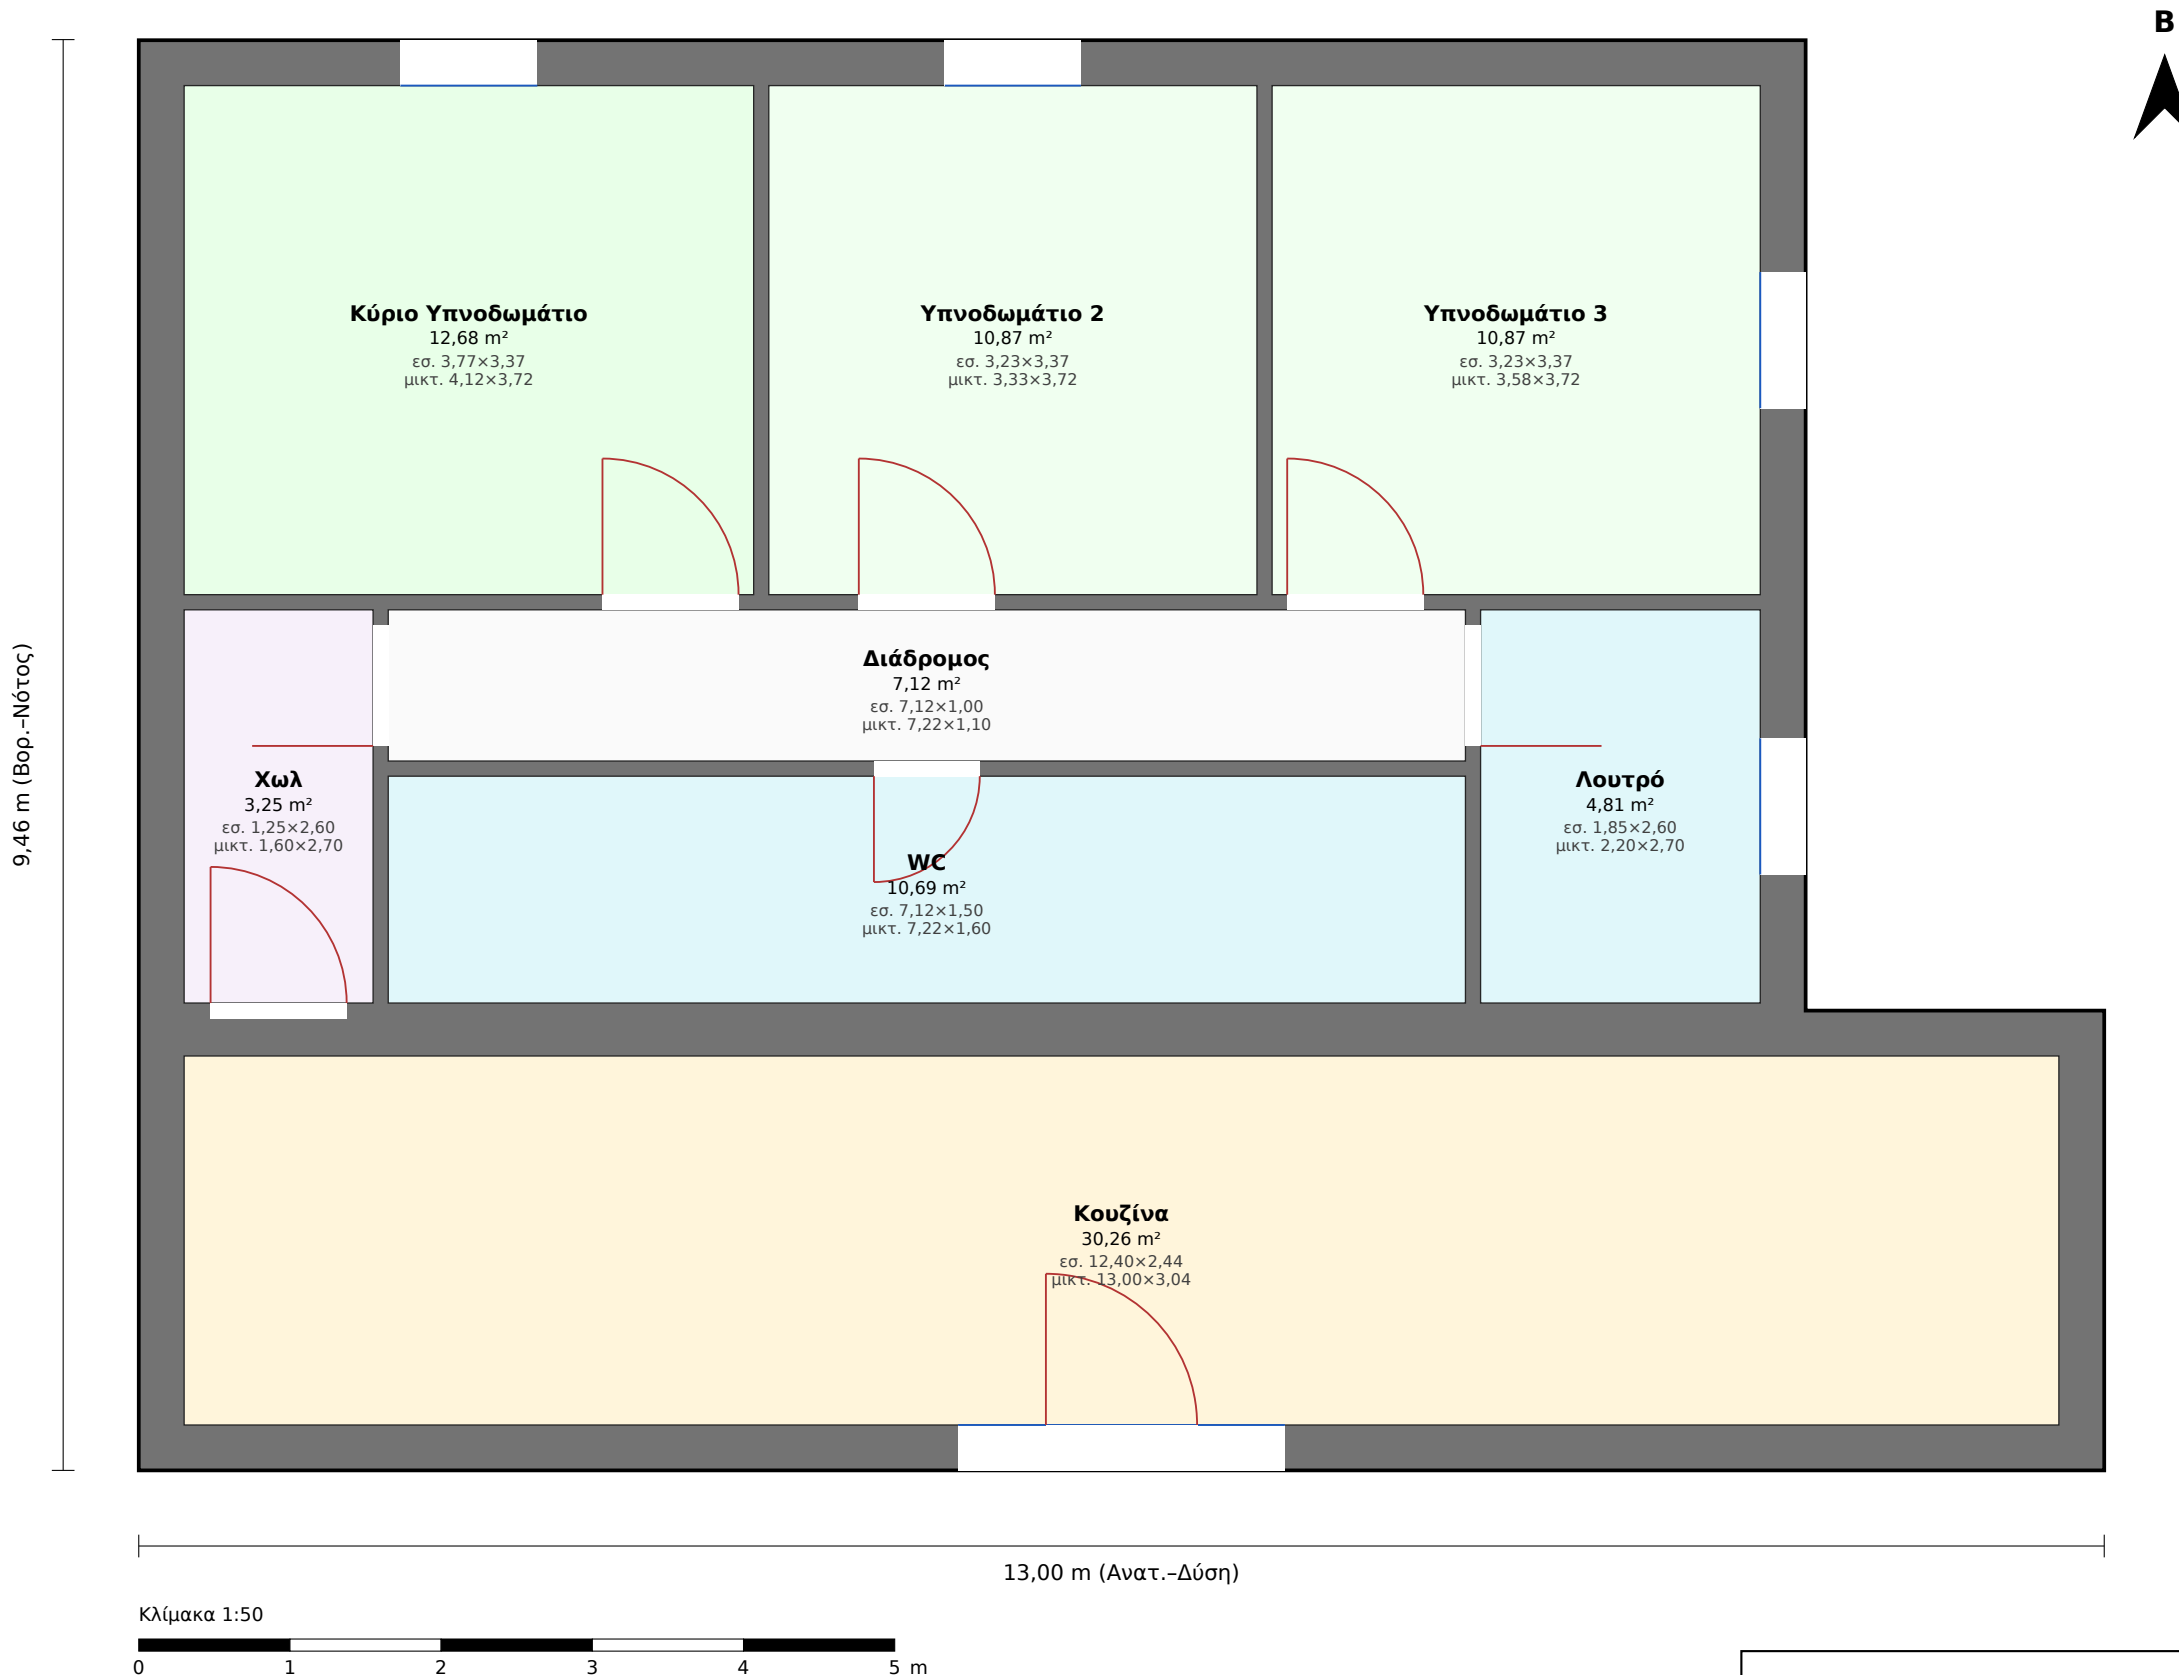

Τεχνικό Γραφείο Μελετών — Γεωργακόπουλος Χρ. / Φουντάς Αθ.
Έργο: Κατοικία
Πρόταση 3 — Ισόγειο
Κλίμακα 1:50 · Μικτό εμβ.: 110,26 m²
Είσοδος: Νότος · Αμαλιάδα, Π.Ε. Ηλείας
Ημερομηνία: 16.08.2026 · Σχεδ.: Γεωργακόπουλος Χρ. (AM TEE 101893)

Κατοικία — Πρόταση 3: Πίνακες χώρων & έλεγχοι

Διαστάσεις: «καθαρές» = εσωτερικές ελεύθερες · «μικτές» = με τοίχους (εξωτ. πλήρες πάχος, εσωτ. μισό). Βορράς: επάνω.

■ **Ισόγειο** (μικτό 110,26 m², καθαρό 90,55 m²)

#	Χώρος	Καθ. εμβ. (m²)	Καθ. Α×Β (m)	Μικτές Α×Β (m)	Ζώνη
1	Κουζίνα	30,26	12,40×2,44	13,00×3,04	κύρια
2	Κύριο Υπνοδωμάτιο	12,68	3,77×3,37	4,12×3,72	κύρια
3	Υπνοδωμάτιο 2	10,87	3,23×3,37	3,33×3,72	κύρια
4	Υπνοδωμάτιο 3	10,87	3,23×3,37	3,58×3,72	κύρια
5	Χωλ	3,25	1,25×2,60	1,60×2,70	βοηθ.
6	WC	10,69	7,12×1,50	7,22×1,60	βοηθ.
7	Λουτρό	4,81	1,85×2,60	2,20×2,70	βοηθ.
8	Διάδρομος	7,12	7,12×1,00	7,22×1,10	βοηθ.

Έλεγχος φωτισμού & αερισμού (Κ.Κ. αρ. 20 §5.1.2 / αρ. 21 §5.2)

Χώρος	Εμβ.	Φως≥10%	Υαλοπ.	Αερ.≥5%	Ανοιγ.	Φως	Αερ.
Κουζίνα	30,3	3,03	3,03	1,51	1,51	✓	✓
Κύριο Υπνοδωμάτιο	12,7	1,27	1,27	0,63	0,63	✓	✓
Υπνοδωμάτιο 2	10,9	1,09	1,26	0,54	0,63	✓	✓
Υπνοδωμάτιο 3	10,9	1,09	1,26	0,54	0,63	✓	✓
Χωλ	3,3	0,33	0,00	0,16	0,00	✓	✓
WC	10,7	1,07	0,00	0,53	0,00	✓	✓
Λουτρό	4,8	0,48	1,26	0,24	0,63	✓	✓

→ Όλοι οι χώροι κύριας χρήσης πληρούν φωτισμό ≥10% & αερισμό ≥5%.