


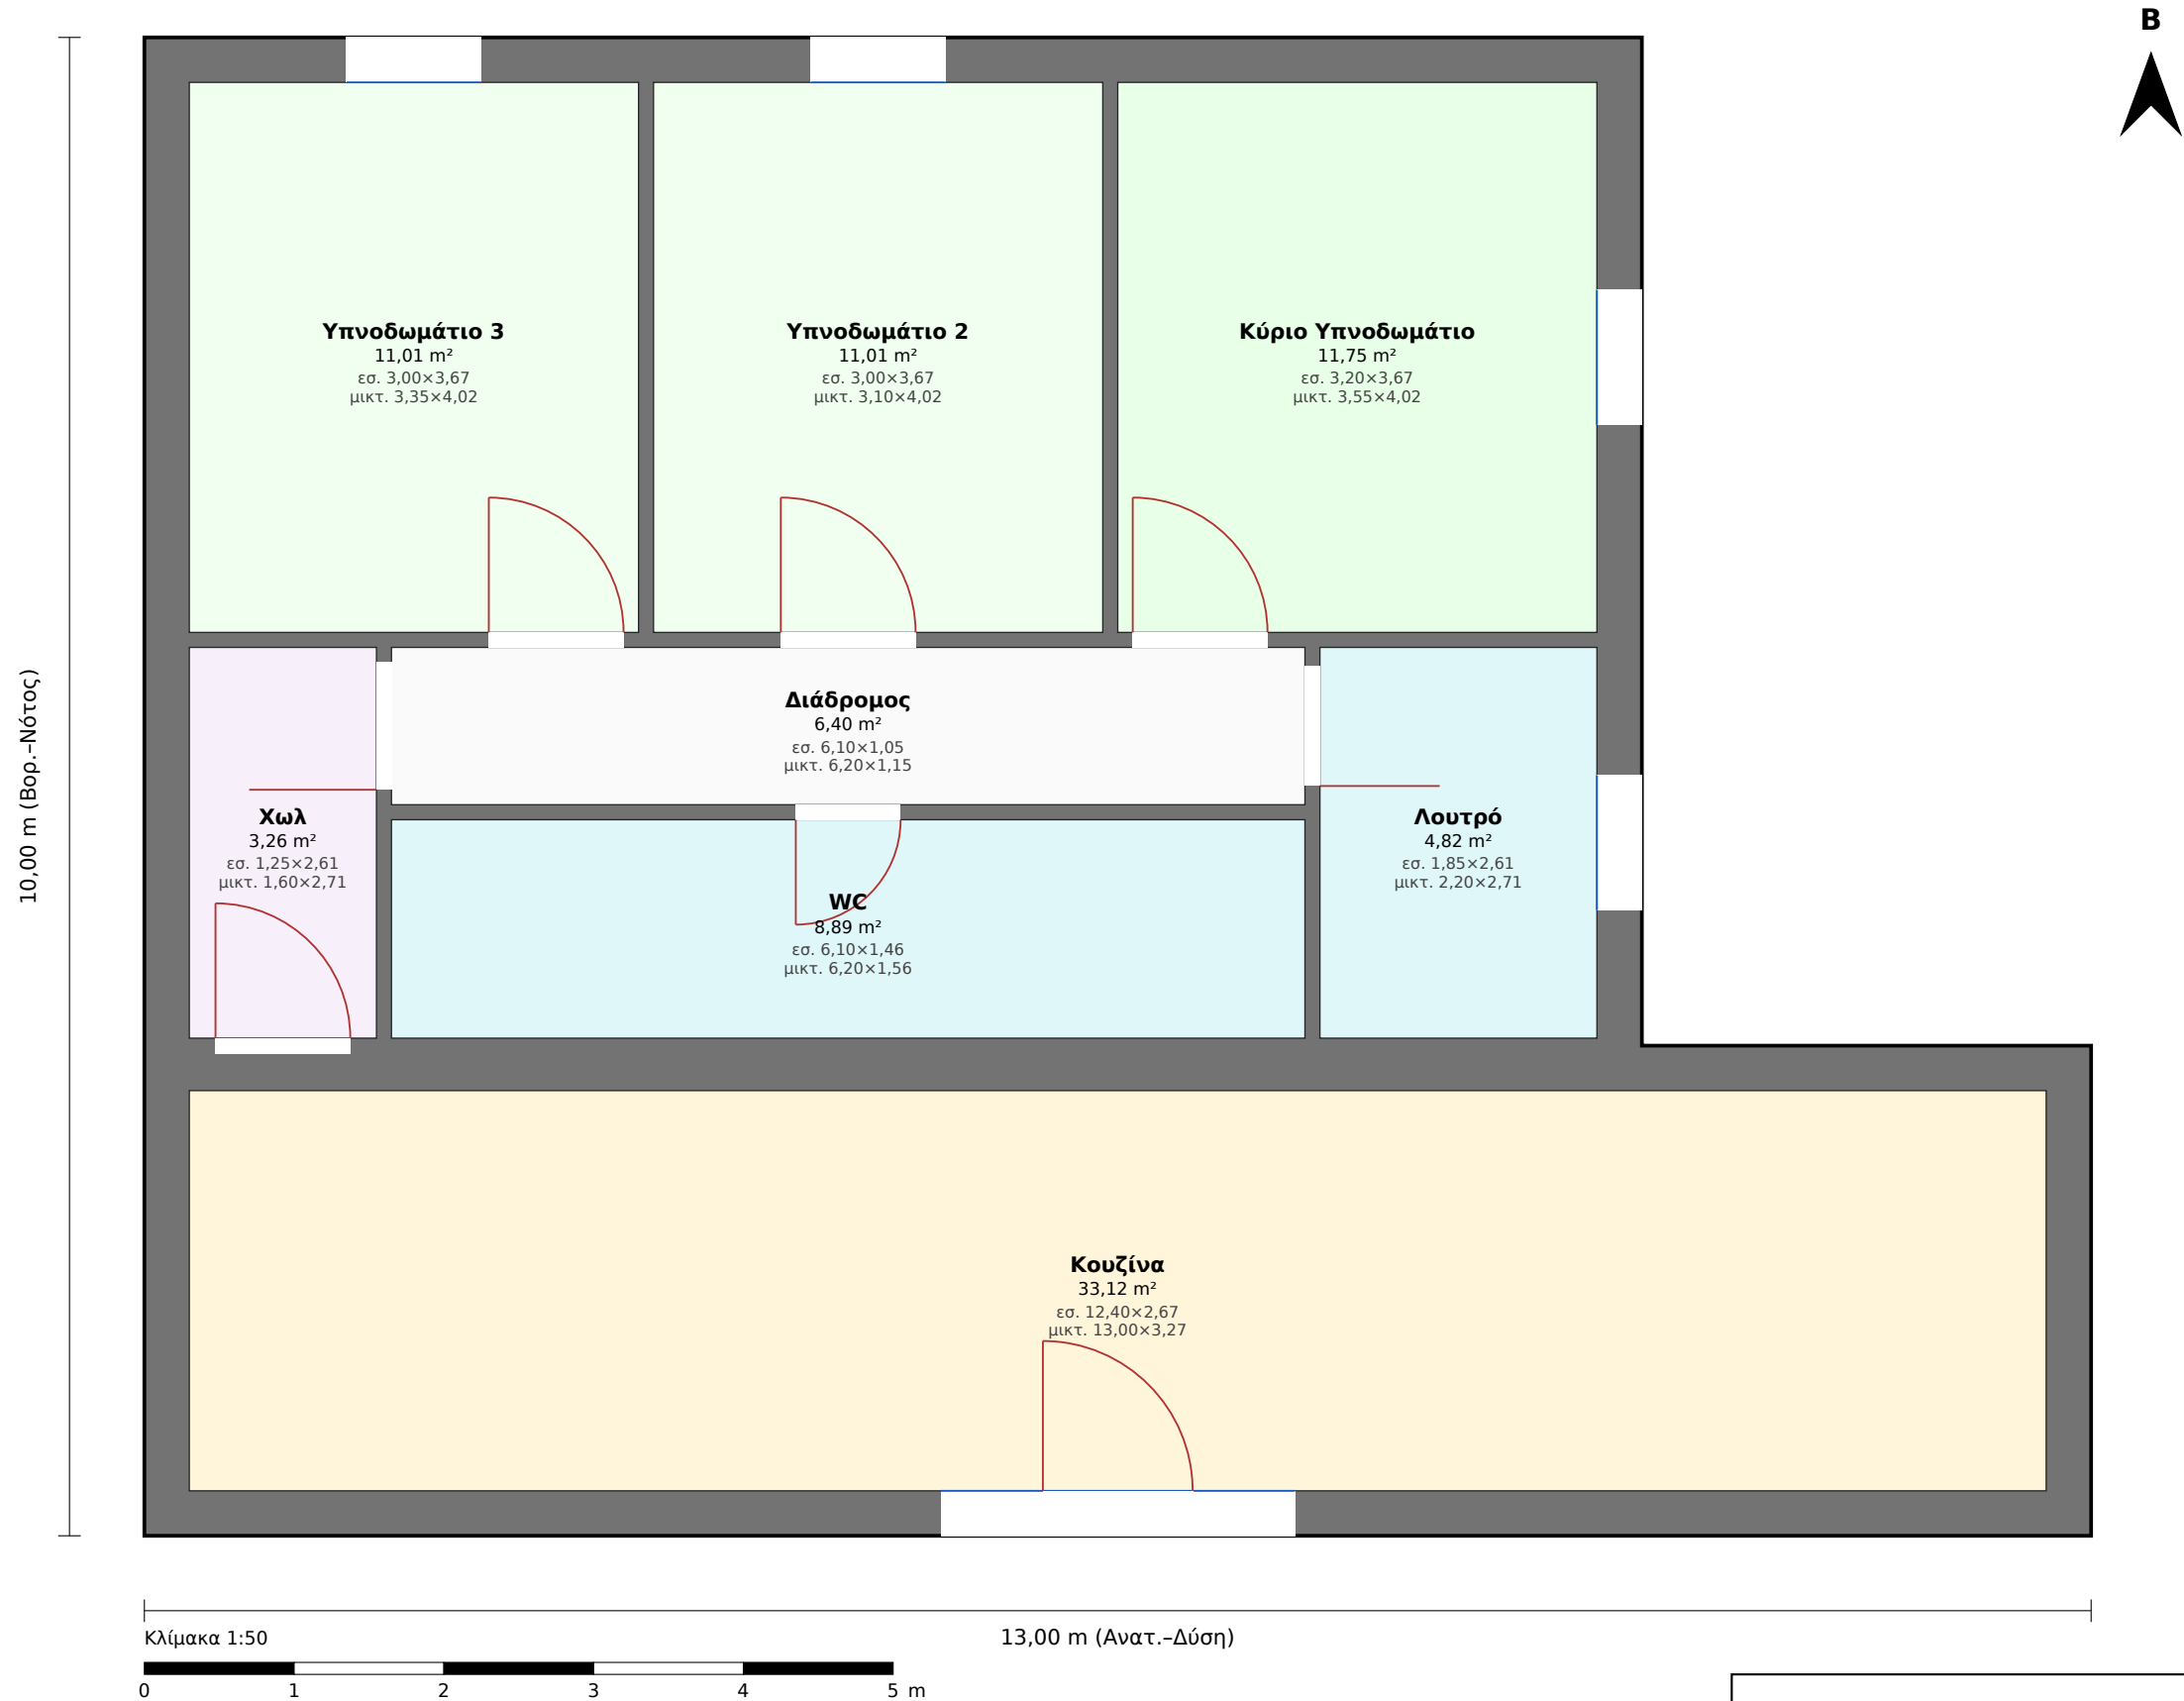

Τεχνικό Γραφείο Μελετών — Γεωργακόπουλος Χρ. / Φουντάς Αθ.
Έργο: Κατοικία
Πρόταση 2 — Ισόγειο
Κλίμακα 1:50 · Μικτό εμβ.: 109,81 m²
Είσοδος: Νότος · Αμαλιάδα, Π.Ε. Ηλείας
Ημερομηνία: 16.08.2026 · Σχεδ.: Γεωργακόπουλος Χρ. (ΑΜ ΤΕΕ 101893)

Κατοικία — Πρόταση 2: Πίνακες χώρων & έλεγχοι

Διαστάσεις: «καθαρές» = εσωτερικές ελεύθερες · «μικτές» = με τοίχους (εξωτ. πλήρες πάχος, εσωτ. μισό). Βορράς: επάνω.

■ Ισόγειο (μικτό 109,81 m², καθαρό 90,28 m²)

#	Χώρος	Καθ. εμβ. (m²)	Καθ. Α×Β (m)	Μικτές Α×Β (m)	Ζώνη
1	Κουζίνα	33,12	12,40×2,67	13,00×3,27	κύρια
2	Υπνοδωμάτιο 3	11,01	3,00×3,67	3,35×4,02	κύρια
3	Υπνοδωμάτιο 2	11,01	3,00×3,67	3,10×4,02	κύρια
4	Κύριο Υπνοδωμάτιο	11,75	3,20×3,67	3,55×4,02	κύρια
5	Χωλ	3,26	1,25×2,61	1,60×2,71	βοηθ.
6	WC	8,89	6,10×1,46	6,20×1,56	βοηθ.
7	Λουτρό	4,82	1,85×2,61	2,20×2,71	βοηθ.
8	Διάδρομος	6,40	6,10×1,05	6,20×1,15	βοηθ.

Έλεγχος φωτισμού & αερισμού (Κ.Κ. αρ. 20 §5.1.2 / αρ. 21 §5.2)

Χώρος	Εμβ.	Φως≥10%	Υαλοπ.	Αερ.≥5%	Ανοιγ.	Φως	Αερ.
Κουζίνα	33,1	3,31	3,31	1,66	1,66	✓	✓
Υπνοδωμάτιο 3	11,0	1,10	1,26	0,55	0,63	✓	✓
Υπνοδωμάτιο 2	11,0	1,10	1,26	0,55	0,63	✓	✓
Κύριο Υπνοδωμάτιο	11,7	1,17	1,26	0,59	0,63	✓	✓
Χωλ	3,3	0,33	0,00	0,16	0,00	✓	✓
WC	8,9	0,89	0,00	0,44	0,00	✓	✓
Λουτρό	4,8	0,48	1,26	0,24	0,63	✓	✓

→ Όλοι οι χώροι κύριας χρήσης πληρούν φωτισμό ≥10% & αερισμό ≥5%.