



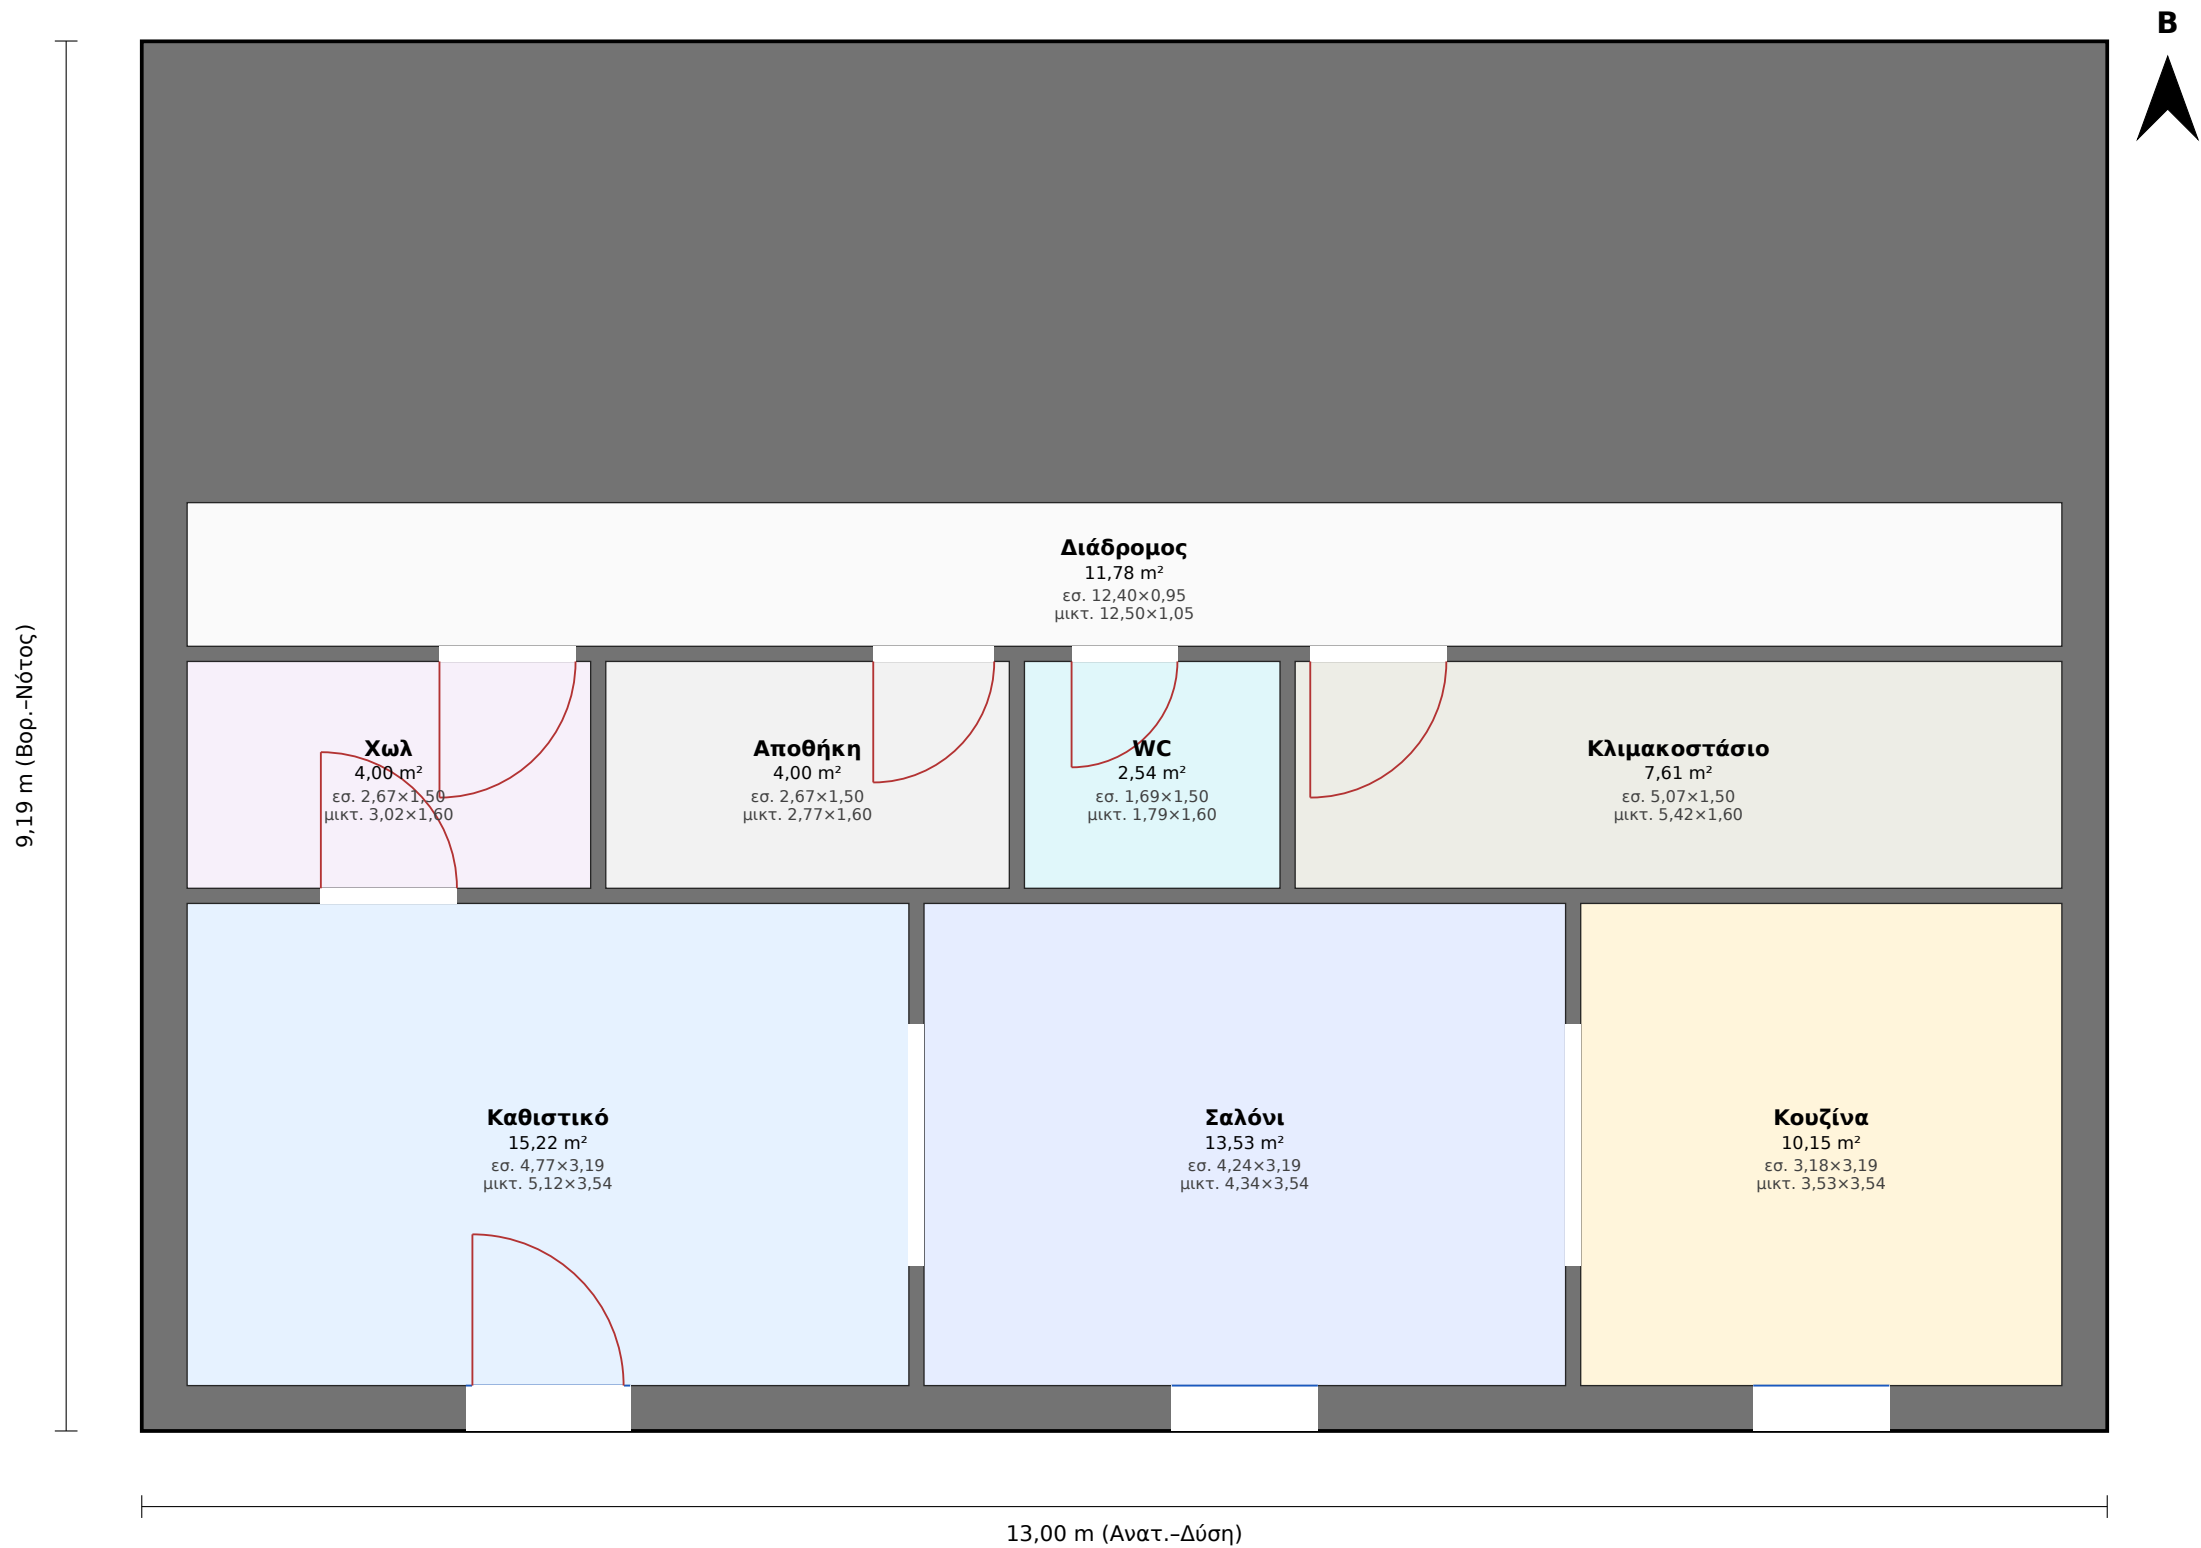

Τεχνικό Γραφείο Μελετών — Γεωργακόπουλος Χρ. / Φουντάς Αθ.
Έργο: Μονοκατοικία Αμαλιάδας
Πρόταση 1 — Ισόγειο
Κλίμακα 1:50 · Μικτό εμβ.: 119,44 m²
Είσοδος: Νότος · Αμαλιάδα, Π.Ε. Ηλείας
Ημερομηνία: 16.08.2026 · Σχεδ.: Γεωργακόπουλος Χρ. (ΑΜ ΤΕΕ 101893)

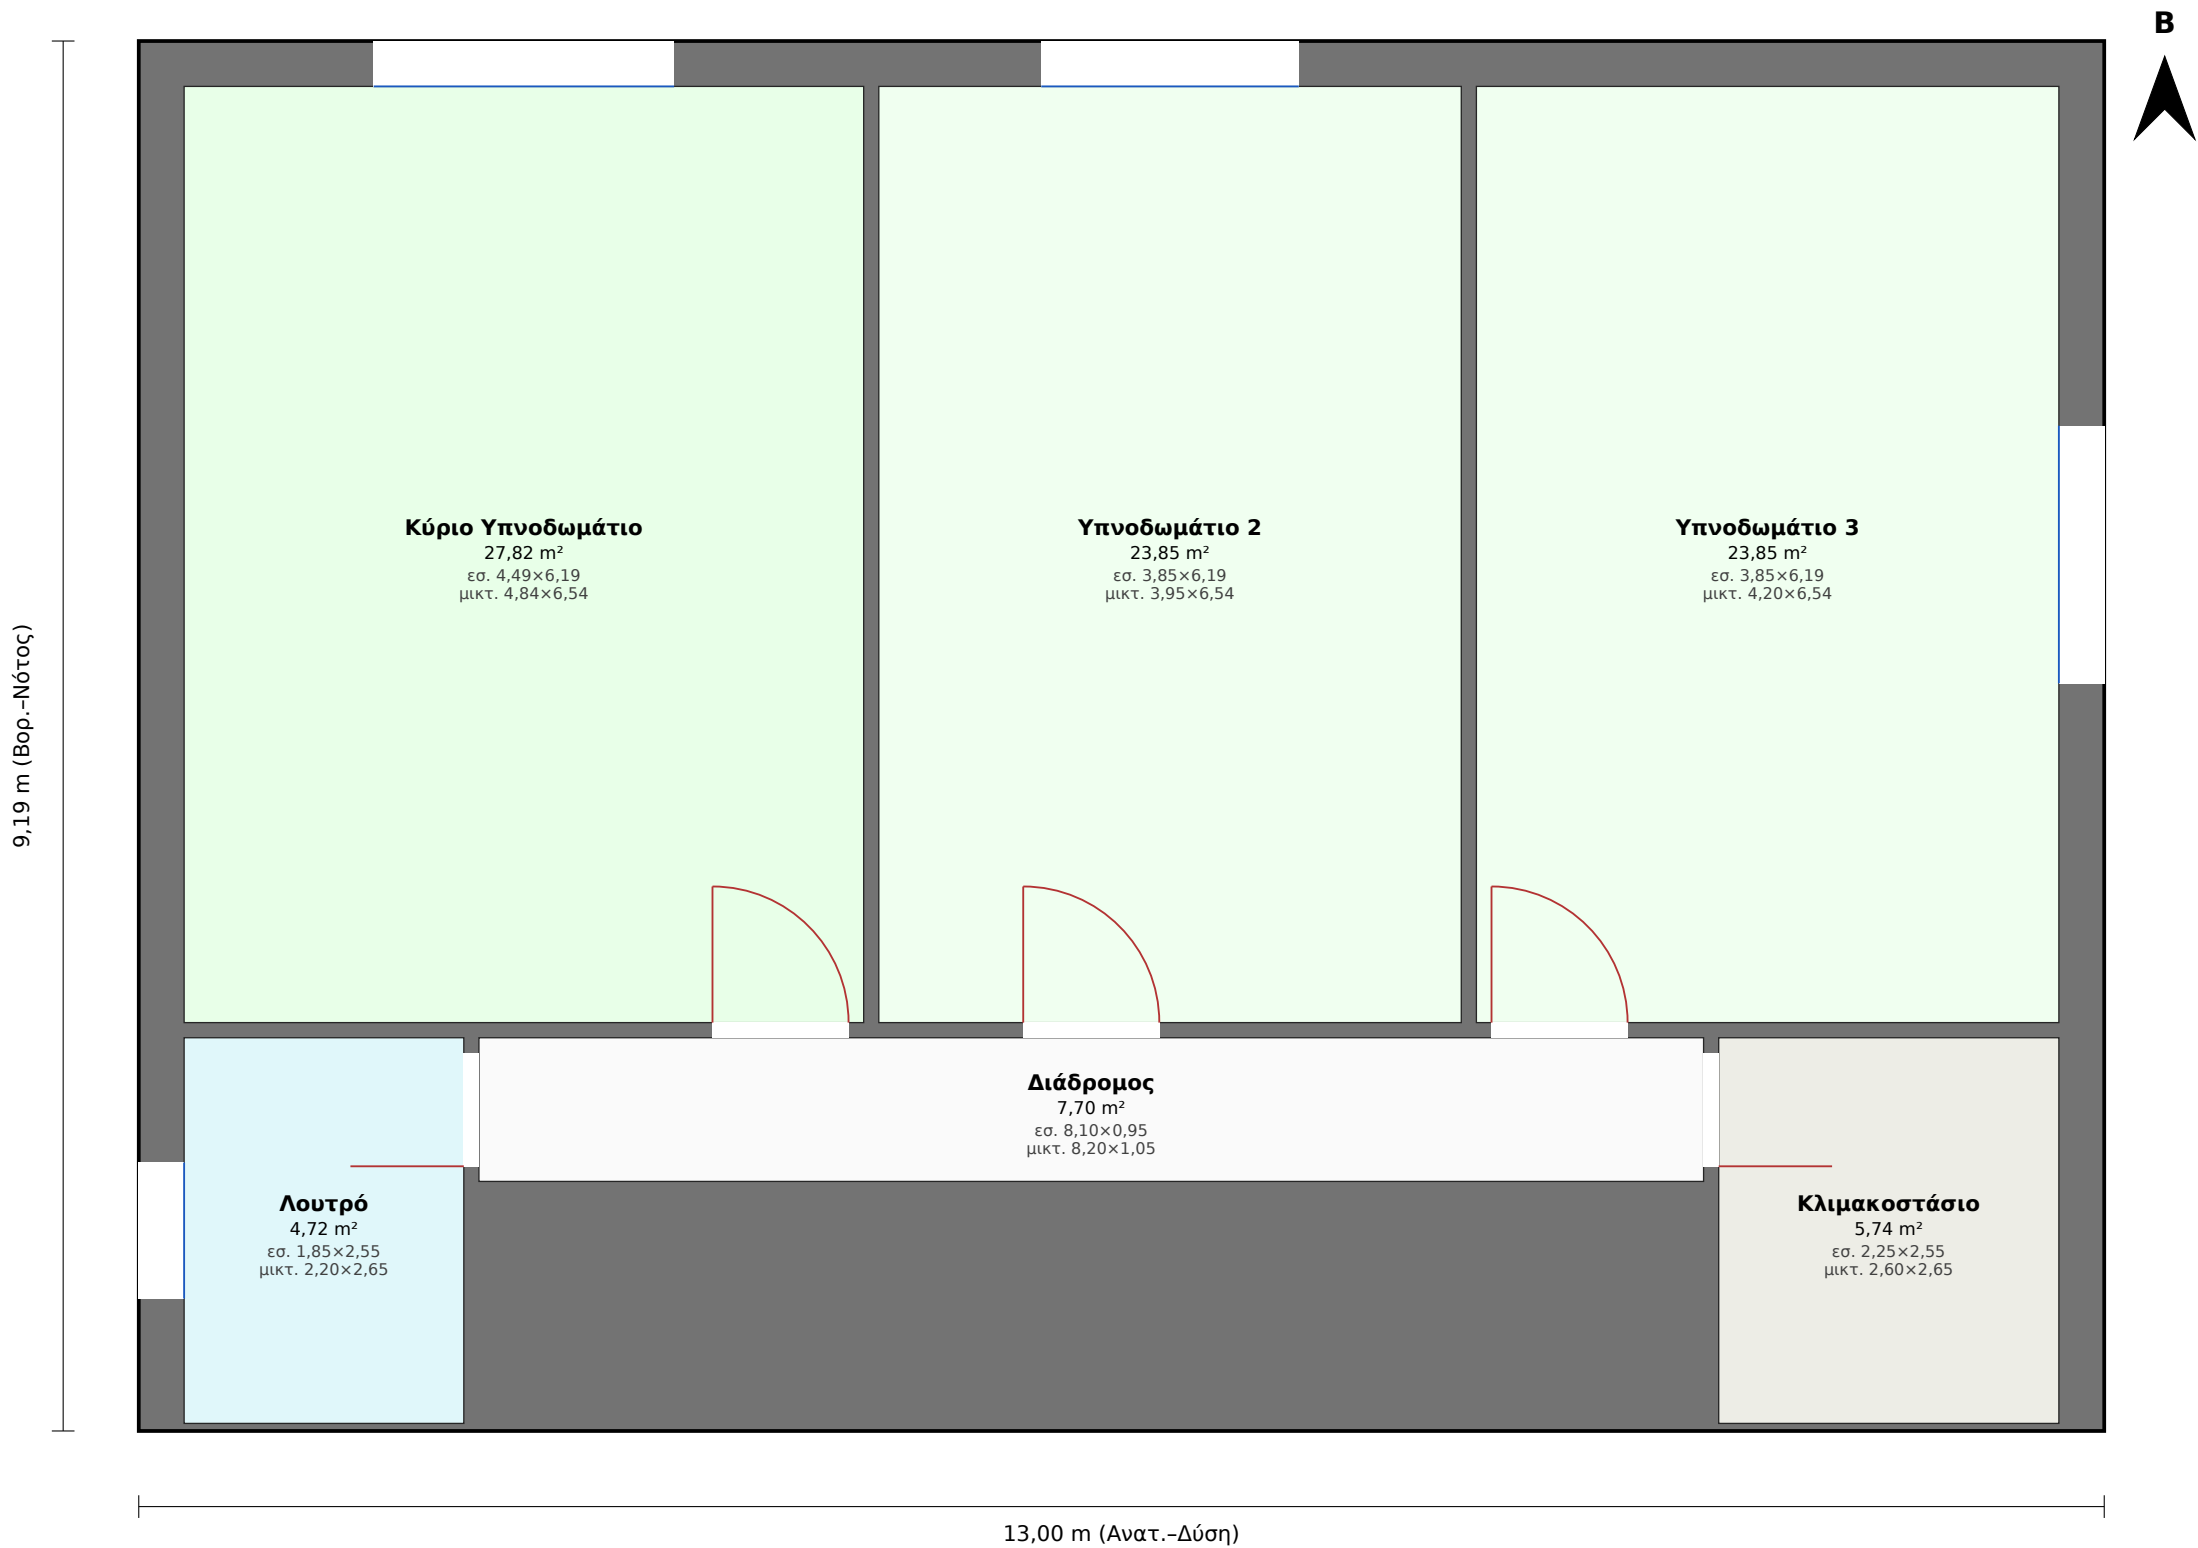

Τεχνικό Γραφείο Μελετών — Γεωργακόπουλος Χρ. / Φουντάς Αθ.
Έργο: Μονοκατοικία Αμαλιάδας
Πρόταση 1 — Α' Όροφος
Κλίμακα 1:50 · Μικτό εμβ.: 119,47 m²
Είσοδος: Νότος · Αμαλιάδα, Π.Ε. Ηλείας
Ημερομηνία: 16.08.2026 · Σχεδ.: Γεωργακόπουλος Χρ. (ΑΜ ΤΕΕ 101893)

Μονοκατοικία Αμαλιάδας — Πρόταση 1: Πίνακες χώρων & έλεγχοι

Διαστάσεις: «καθαρές» = εσωτερικές ελεύθερες · «μικτές» = με τοίχους (εξωτ. πλήρες πάχος, εσωτ. μισό). Βορράς: επάνω.

■ Ισόγειο (μικτό 119,44 m², καθαρό 68,82 m²)

#	Χώρος	Καθ. εμβ. (m²)	Καθ. Α×Β (m)	Μικτές Α×Β (m)	Ζώνη
1	Καθιστικό	15,22	4,77×3,19	5,12×3,54	κύρια
2	Σαλόνι	13,53	4,24×3,19	4,34×3,54	κύρια
3	Κουζίνα	10,15	3,18×3,19	3,53×3,54	κύρια
4	Χωλ	4,00	2,67×1,50	3,02×1,60	βοηθ.
5	Αποθήκη	4,00	2,67×1,50	2,77×1,60	βοηθ.
6	WC	2,54	1,69×1,50	1,79×1,60	βοηθ.
7	Κλιμακοστάσιο	7,61	5,07×1,50	5,42×1,60	βοηθ.
8	Διάδρομος	11,78	12,40×0,95	12,50×1,05	βοηθ.

Έλεγχος φωτισμού & αερισμού (Κ.Κ. αρ. 20 §5.1.2 / αρ. 21 §5.2)

Χώρος	Εμβ.	Φως≥10%	Υαλοπ.	Αερ.≥5%	Ανοιγ.	Φως	Αερ.
Καθιστικό	15,2	1,52	1,52	0,76	0,76	✓	✓
Σαλόνι	13,5	1,35	1,35	0,68	0,68	✓	✓
Κουζίνα	10,1	1,01	1,26	0,51	0,63	✓	✓
Χωλ	4,0	0,40	0,00	0,20	0,00	✓	✓
Αποθήκη	4,0	0,40	0,00	0,20	0,00	✓	✓
WC	2,5	0,25	0,00	0,13	0,00	✓	✓
Κλιμακοστάσιο	7,6	0,76	0,00	0,38	0,00	✓	✓

→ Όλοι οι χώροι κύριας χρήσης πληρούν φωτισμό ≥10% & αερισμό ≥5%.


■ Α' Όροφος (μικτό 119,47 m², καθαρό 93,67 m²)

#	Χώρος	Καθ. εμβ. (m²)	Καθ. Α×Β (m)	Μικτές Α×Β (m)	Ζώνη
1	Κύριο Υπνοδωμάτιο	27,82	4,49×6,19	4,84×6,54	κύρια
2	Υπνοδωμάτιο 2	23,85	3,85×6,19	3,95×6,54	κύρια
3	Υπνοδωμάτιο 3	23,85	3,85×6,19	4,20×6,54	κύρια
4	Λουτρό	4,72	1,85×2,55	2,20×2,65	βοηθ.
5	Κλιμακοστάσιο	5,74	2,25×2,55	2,60×2,65	βοηθ.
6	Διάδρομος	7,70	8,10×0,95	8,20×1,05	βοηθ.


Έλεγχος φωτισμού & αερισμού (Κ.Κ. αρ. 20 §5.1.2 / αρ. 21 §5.2)

Χώρος	Εμβ.	Φως≥10%	Υαλοπ.	Αερ.≥5%	Ανοιγ.	Φως	Αερ.
Κύριο Υπνοδωμάτιο	27,8	2,78	2,78	1,39	1,39	✓	✓
Υπνοδωμάτιο 2	23,8	2,38	2,38	1,19	1,19	✓	✓
Υπνοδωμάτιο 3	23,8	2,38	2,38	1,19	1,19	✓	✓
Λουτρό	4,7	0,47	1,26	0,24	0,63	✓	✓
Κλιμακοστάσιο	5,7	0,57	0,00	0,29	0,00	✓	✓

→ Όλοι οι χώροι κύριας χρήσης πληρούν φωτισμό ≥10% & αερισμό ≥5%.

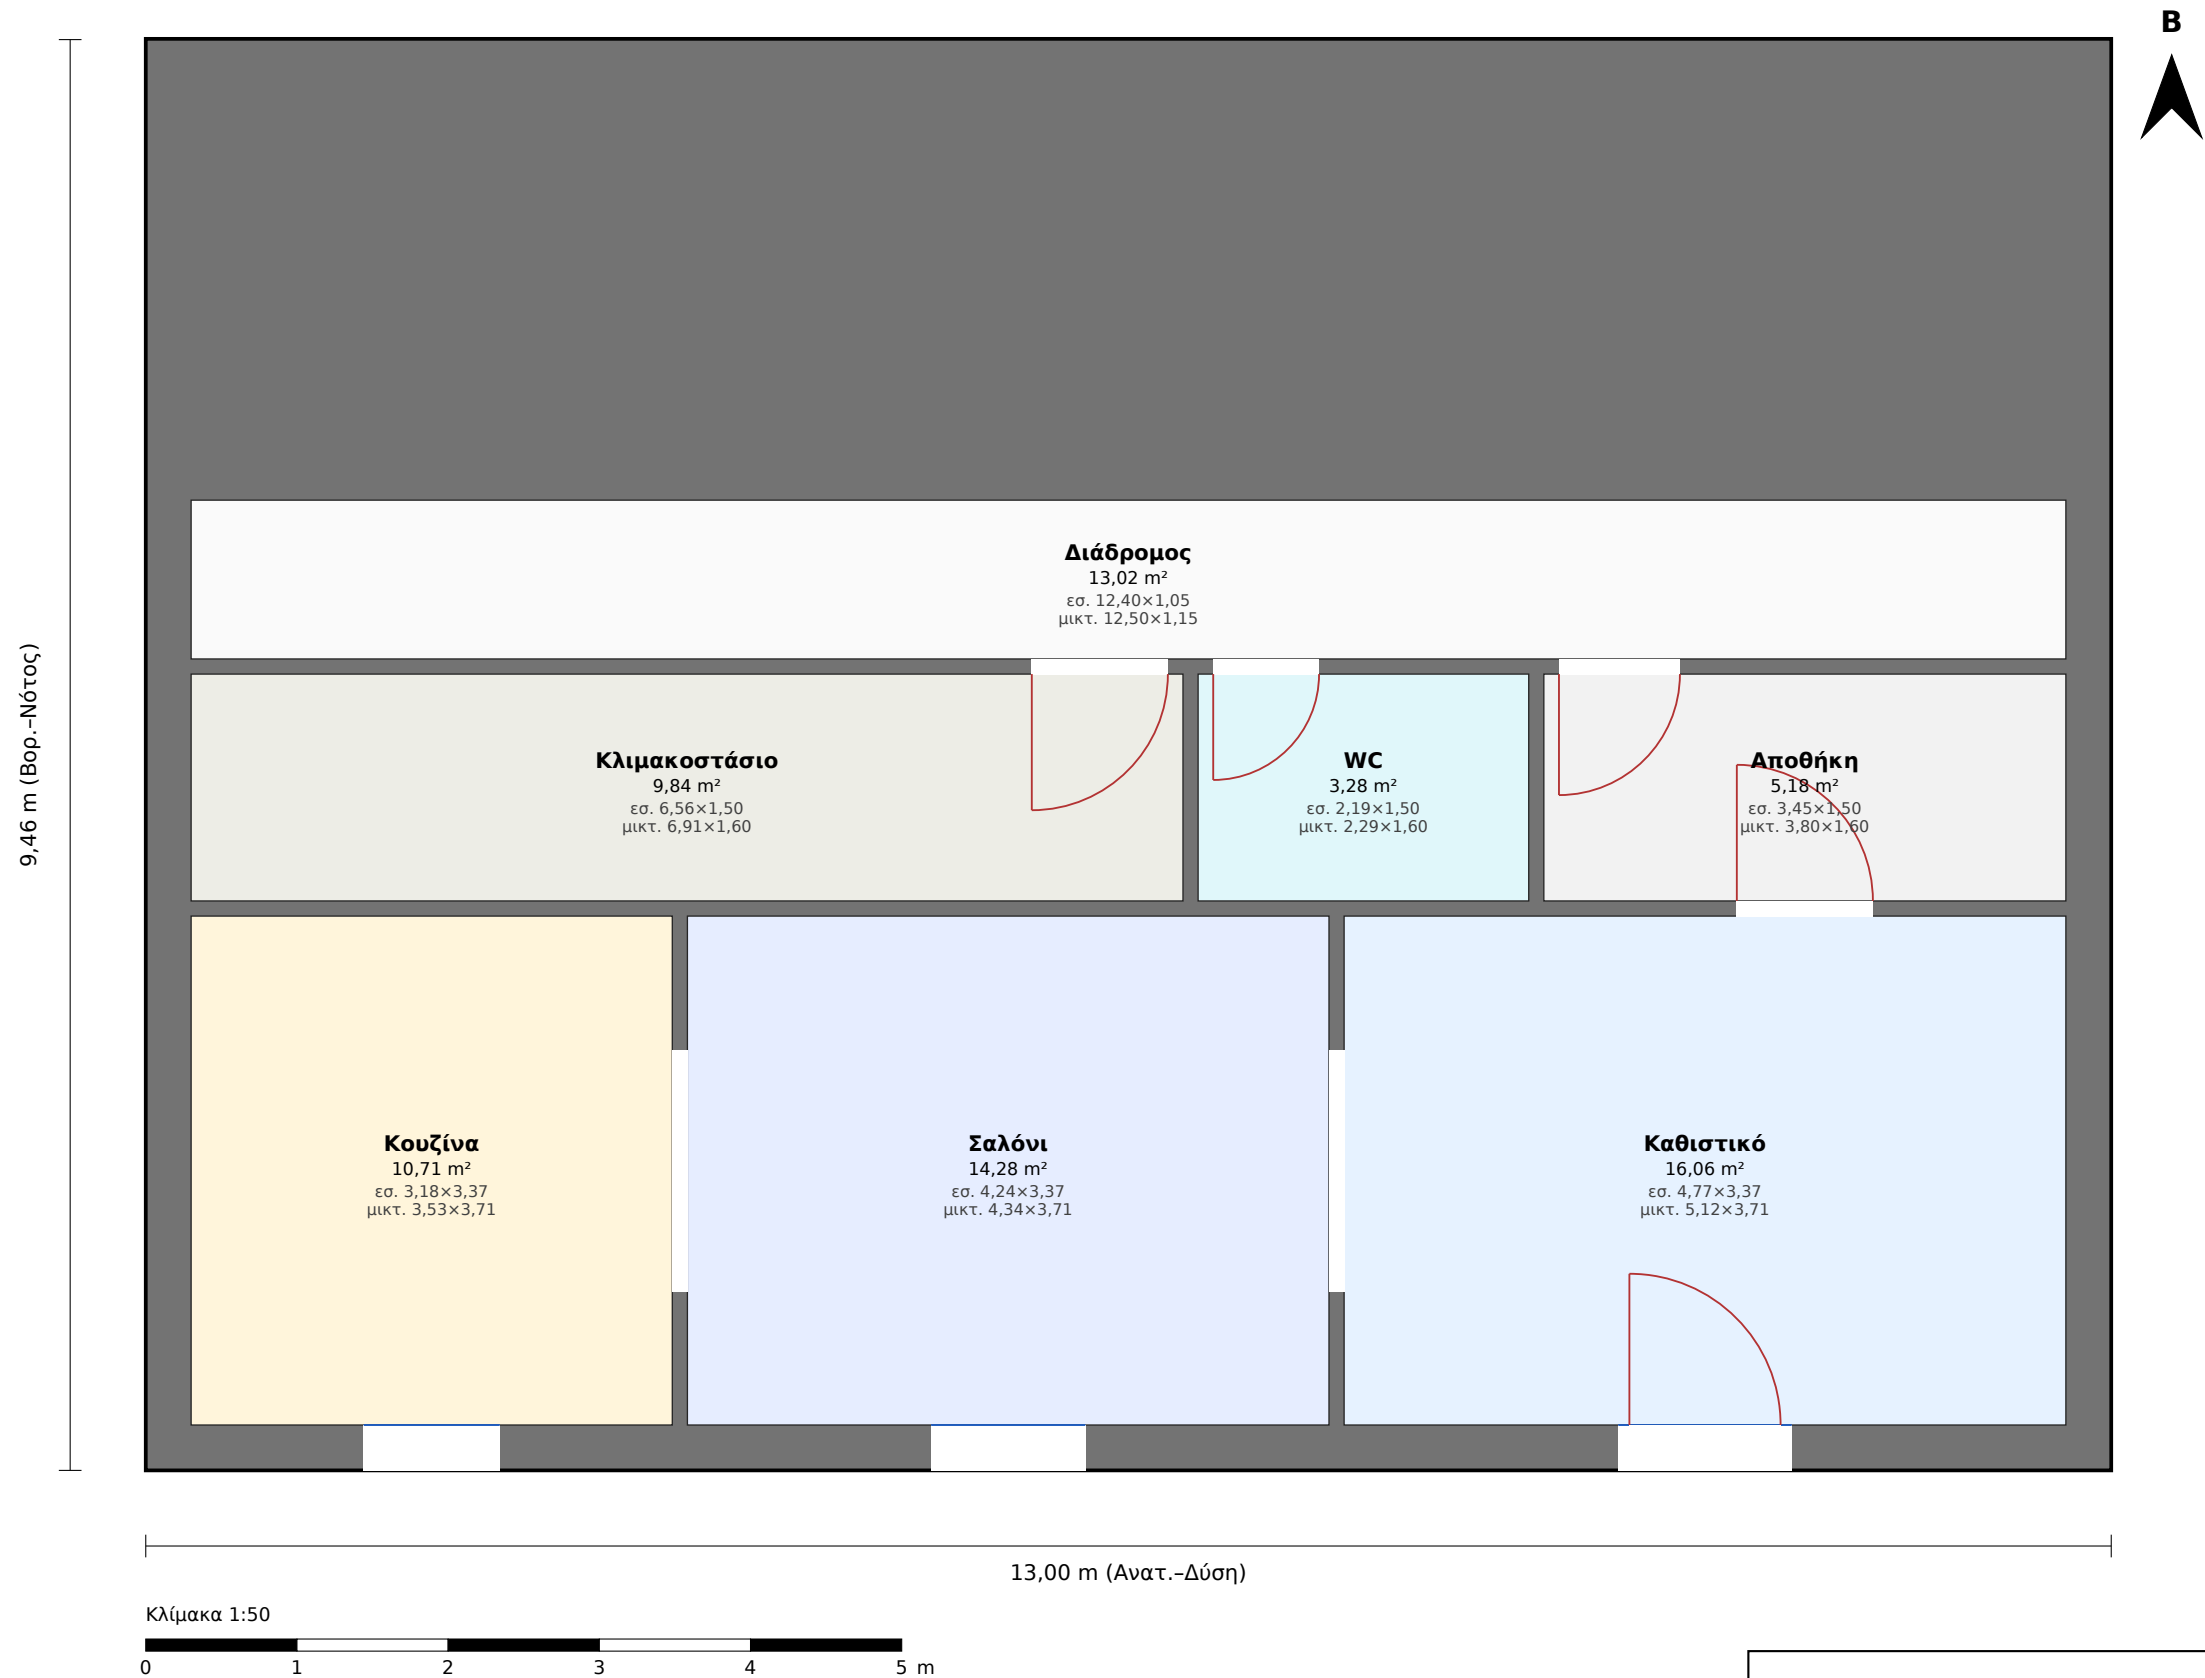

Τεχνικό Γραφείο Μελετών — Γεωργακόπουλος Χρ. / Φουντάς Αθ.
Έργο: Μονοκατοικία Αμαλιάδας
Πρόταση 2 — Ισόγειο
Κλίμακα 1:50 · Μικτό εμβ.: 123,05 m²
Είσοδος: Νότος · Αμαλιάδα, Π.Ε. Ηλείας
Ημερομηνία: 16.08.2026 · Σχεδ.: Γεωργακόπουλος Χρ. (ΑΜ ΤΕΕ 101893)

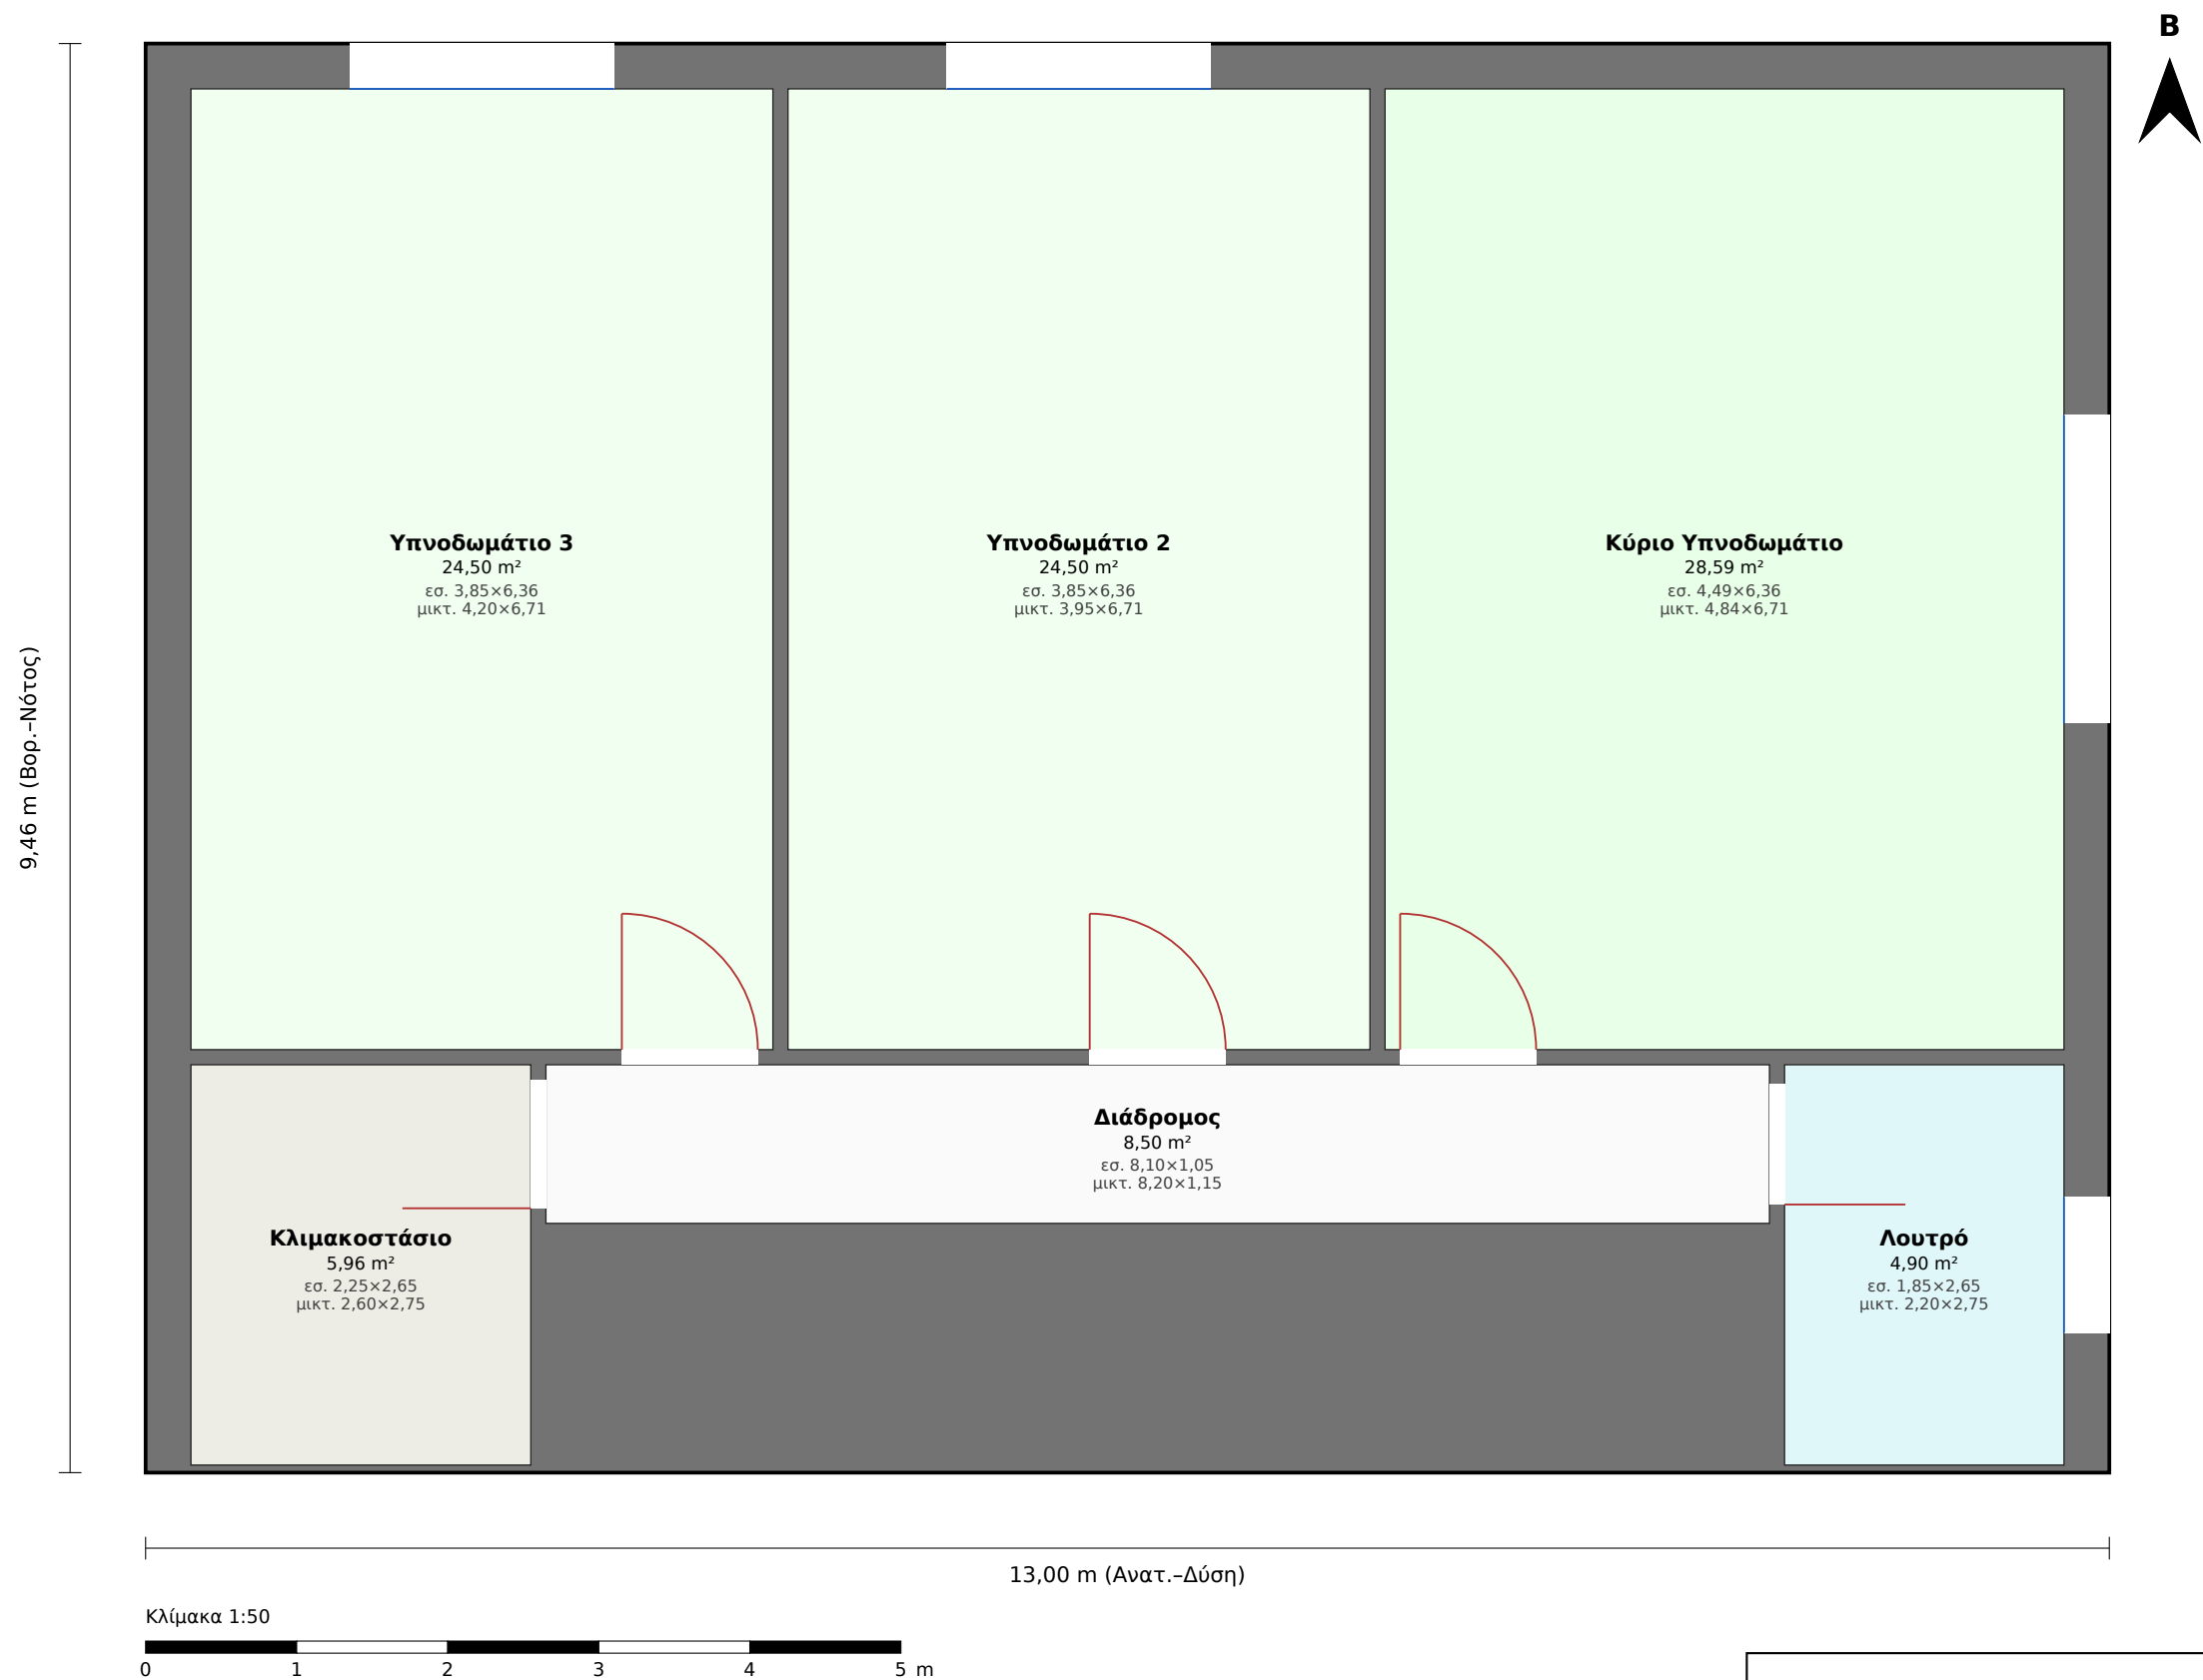

Τεχνικό Γραφείο Μελετών — Γεωργακόπουλος Χρ. / Φουντάς Αθ.
Έργο: Μονοκατοικία Αμαλιάδας
Πρόταση 2 — Α' Όροφος
Κλίμακα 1:50 · Μικτό εμβ.: 122,98 m²
Είσοδος: Νότος · Αμαλιάδα, Π.Ε. Ηλείας
Ημερομηνία: 16.08.2026 · Σχεδ.: Γεωργακόπουλος Χρ. (AM TEE 101893)

Μονοκατοικία Αμαλιάδας — Πρόταση 2: Πίνακες χώρων & έλεγχοι

Διαστάσεις: «καθαρές» = εσωτερικές ελεύθερες · «μικτές» = με τοίχους (εξωτ. πλήρες πάχος, εσωτ. μισό). Βορράς: επάνω.

■ Ισόγειο (μικτό 123,05 m², καθαρό 72,37 m²)

#	Χώρος	Καθ. εμβ. (m²)	Καθ. Α×Β (m)	Μικτές Α×Β (m)	Ζώνη
1	Κουζίνα	10,71	3,18×3,37	3,53×3,71	κύρια
2	Σαλόνι	14,28	4,24×3,37	4,34×3,71	κύρια
3	Καθιστικό	16,06	4,77×3,37	5,12×3,71	κύρια
4	Κλιμακοστάσιο	9,84	6,56×1,50	6,91×1,60	βοηθ.
5	WC	3,28	2,19×1,50	2,29×1,60	βοηθ.
6	Αποθήκη	5,18	3,45×1,50	3,80×1,60	βοηθ.
7	Διάδρομος	13,02	12,40×1,05	12,50×1,15	βοηθ.

Έλεγχος φωτισμού & αερισμού (Κ.Κ. αρ. 20 §5.1.2 / αρ. 21 §5.2)

Χώρος	Εμβ.	Φως≥10%	Υαλοπ.	Αερ.≥5%	Ανοιγ.	Φως	Αερ.
Κουζίνα	10,7	1,07	1,26	0,54	0,63	✓	✓
Σαλόνι	14,3	1,43	1,43	0,71	0,71	✓	✓
Καθιστικό	16,1	1,61	1,61	0,80	0,80	✓	✓
Κλιμακοστάσιο	9,8	0,98	0,00	0,49	0,00	✓	✓
WC	3,3	0,33	0,00	0,16	0,00	✓	✓
Αποθήκη	5,2	0,52	0,00	0,26	0,00	✓	✓

→ Όλοι οι χώροι κύριας χρήσης πληρούν φωτισμό ≥10% & αερισμό ≥5%.


■ Α' Όροφος (μικτό 122,98 m², καθαρό 96,96 m²)

#	Χώρος	Καθ. εμβ. (m²)	Καθ. Α×Β (m)	Μικτές Α×Β (m)	Ζώνη
1	Υπνοδωμάτιο 3	24,50	3,85×6,36	4,20×6,71	κύρια
2	Υπνοδωμάτιο 2	24,50	3,85×6,36	3,95×6,71	κύρια
3	Κύριο Υπνοδωμάτιο	28,59	4,49×6,36	4,84×6,71	κύρια
4	Κλιμακοστάσιο	5,96	2,25×2,65	2,60×2,75	βοηθ.
5	Λουτρό	4,90	1,85×2,65	2,20×2,75	βοηθ.
6	Διάδρομος	8,50	8,10×1,05	8,20×1,15	βοηθ.


Έλεγχος φωτισμού & αερισμού (Κ.Κ. αρ. 20 §5.1.2 / αρ. 21 §5.2)

Χώρος	Εμβ.	Φως≥10%	Υαλοπ.	Αερ.≥5%	Ανοιγ.	Φως	Αερ.
Υπνοδωμάτιο 3	24,5	2,45	2,45	1,23	1,23	✓	✓
Υπνοδωμάτιο 2	24,5	2,45	2,45	1,23	1,23	✓	✓
Κύριο Υπνοδωμάτιο	28,6	2,86	2,86	1,43	1,43	✓	✓
Κλιμακοστάσιο	6,0	0,60	0,00	0,30	0,00	✓	✓
Λουτρό	4,9	0,49	1,26	0,25	0,63	✓	✓

→ Όλοι οι χώροι κύριας χρήσης πληρούν φωτισμό ≥10% & αερισμό ≥5%.

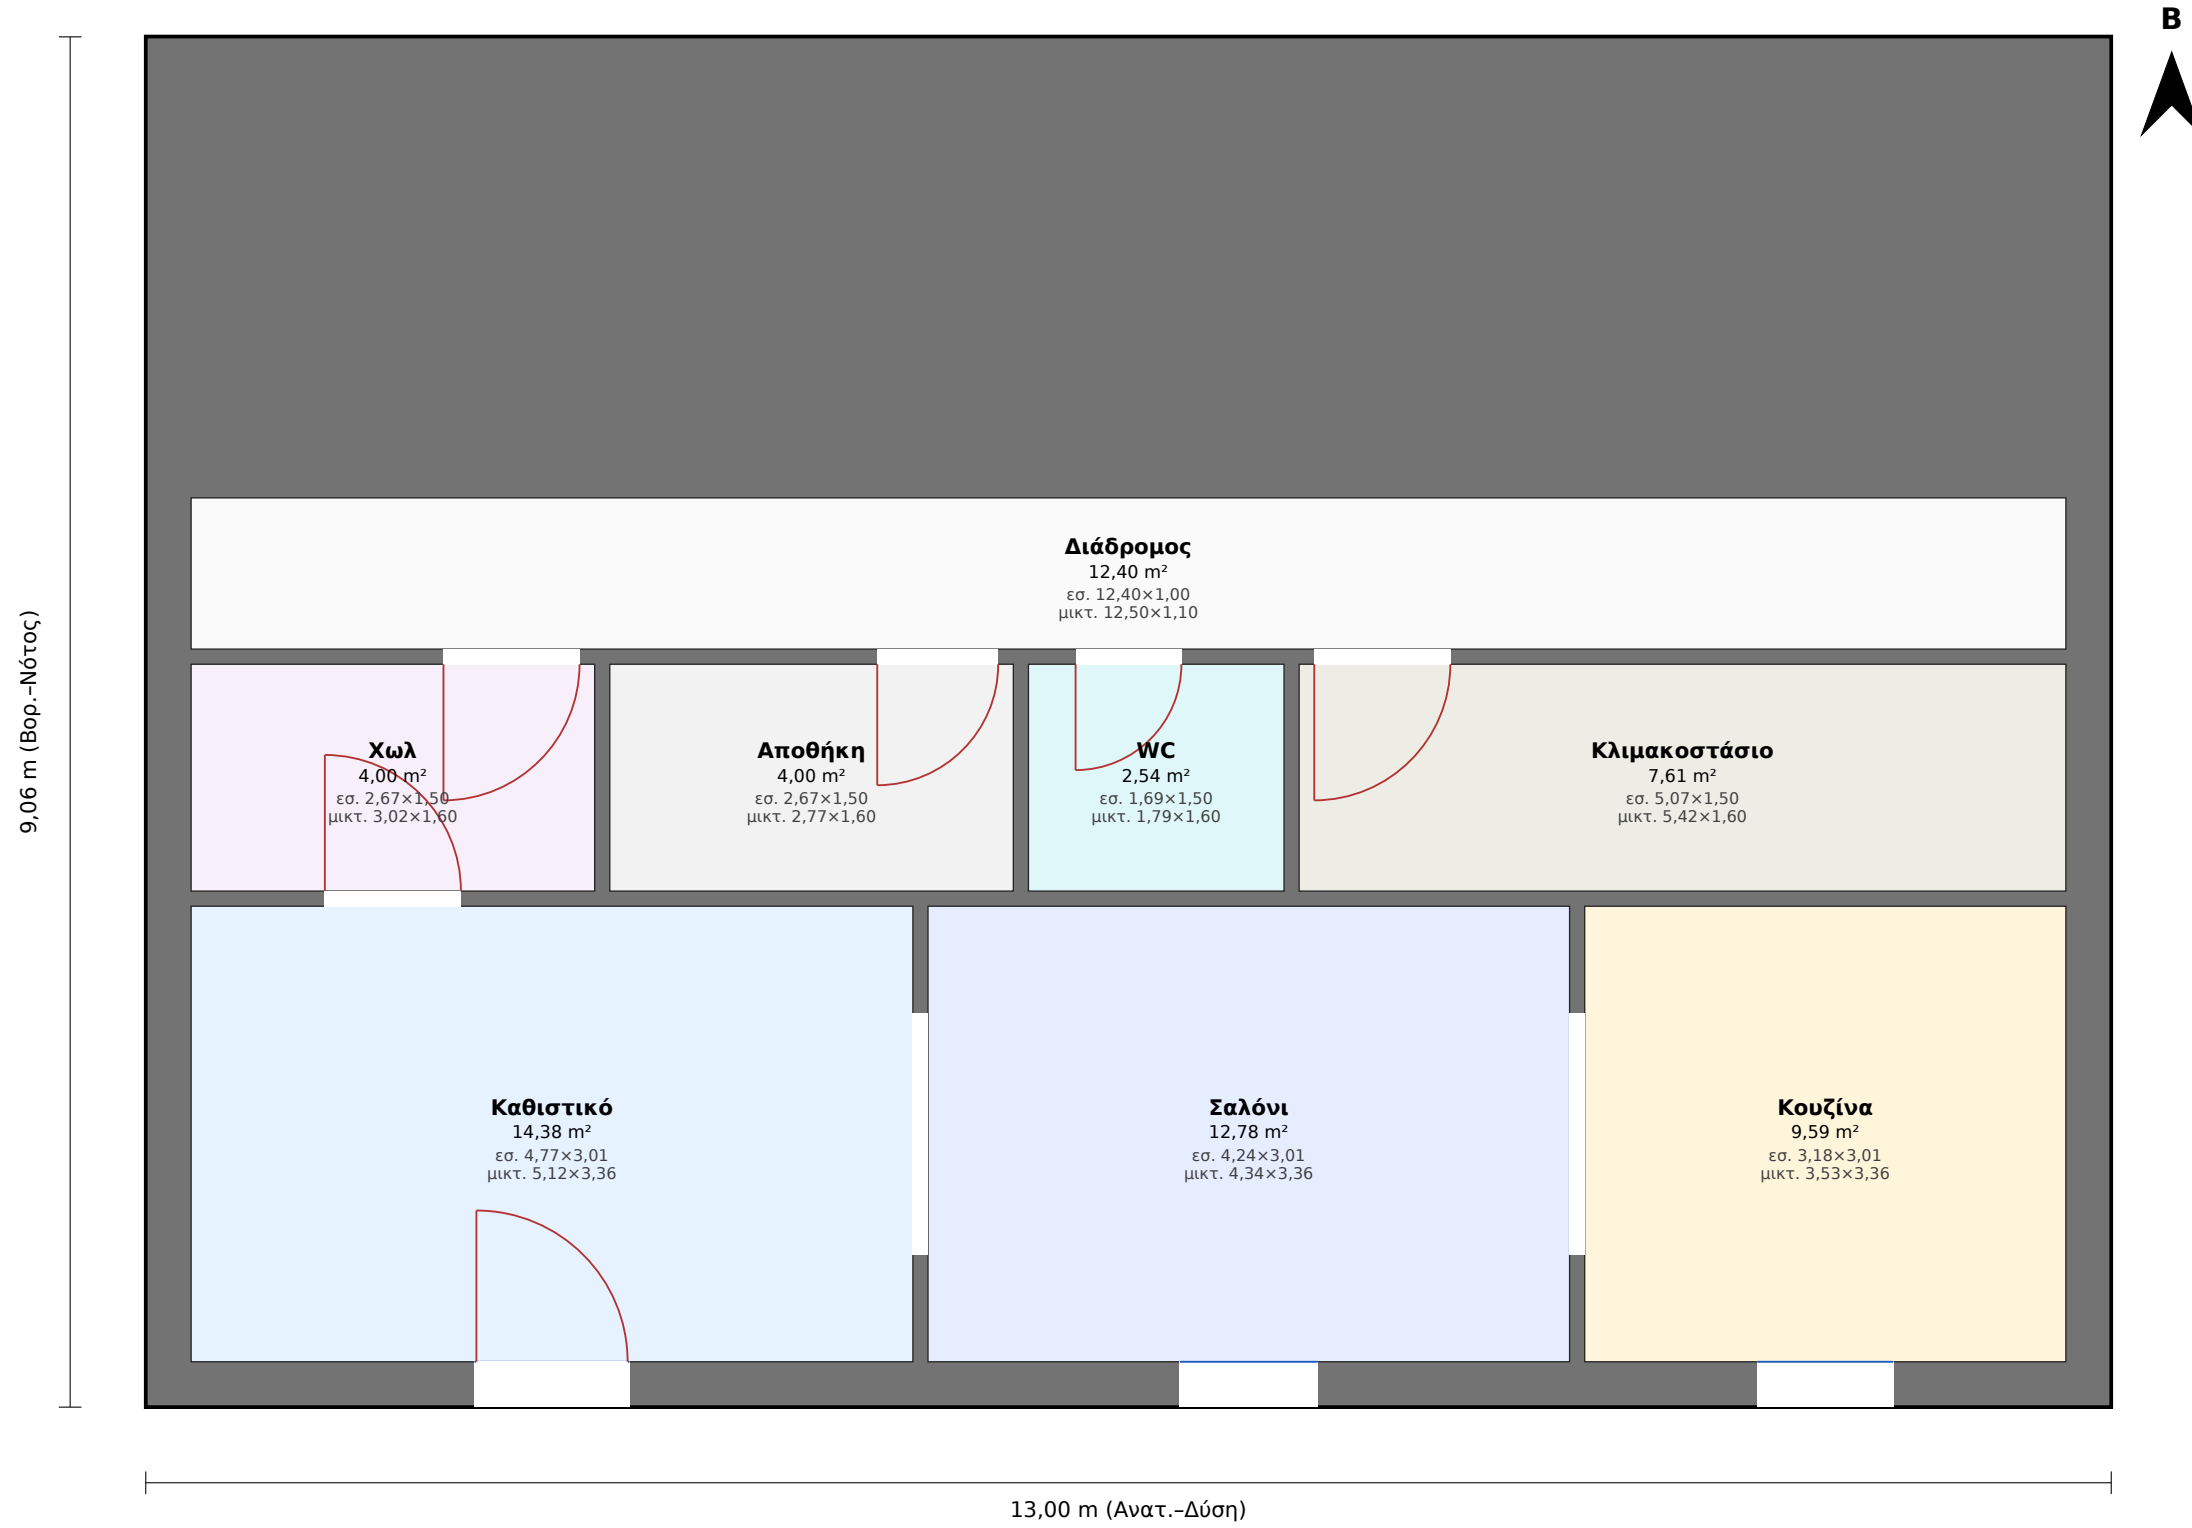

Τεχνικό Γραφείο Μελετών — Γεωργακόπουλος Χρ. / Φουντάς Αθ.
Έργο: Μονοκατοικία Αμαλιάδας
Πρόταση 3 — Ισόγειο
Κλίμακα 1:50 · Μικτό εμβ.: 117,81 m²
Είσοδος: Νότος · Αμαλιάδα, Π.Ε. Ηλείας
Ημερομηνία: 16.08.2026 · Σχεδ.: Γεωργακόπουλος Χρ. (AM TEE 101893)

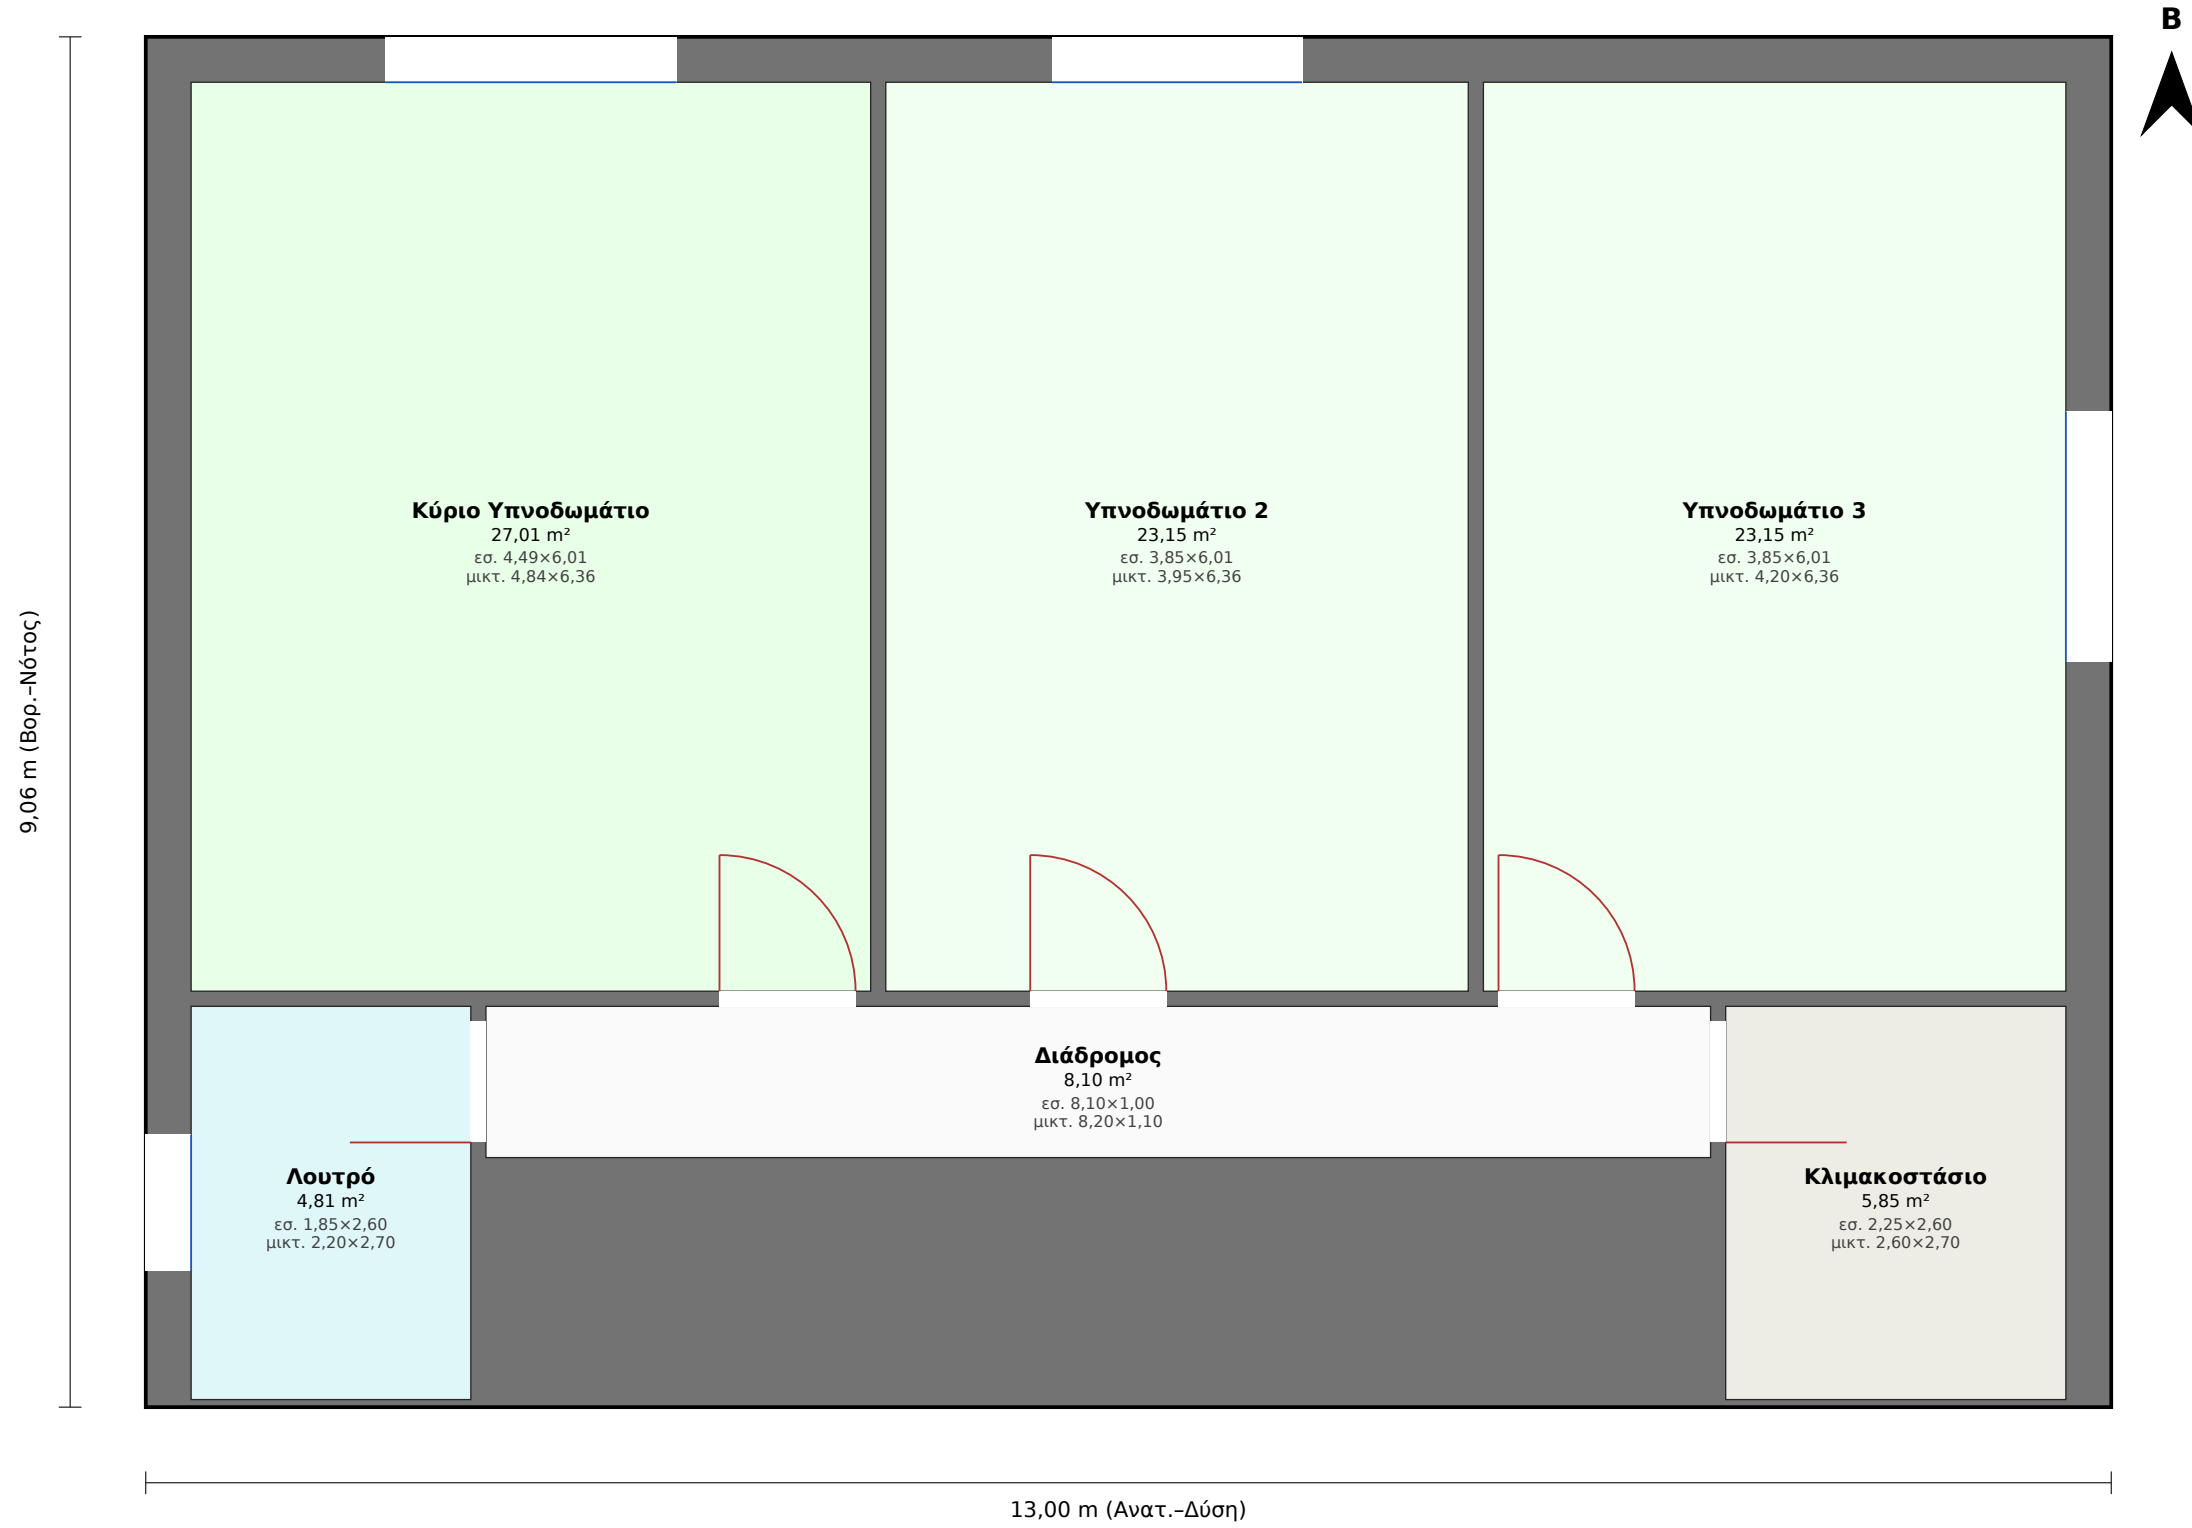

Τεχνικό Γραφείο Μελετών — Γεωργακόπουλος Χρ. / Φουντάς Αθ.
Έργο: Μονοκατοικία Αμαλιάδας
Πρόταση 3 — Α' Όροφος
Κλίμακα 1:50 · Μικτό εμβ.: 117,78 m²
Είσοδος: Νότος · Αμαλιάδα, Π.Ε. Ηλείας
Ημερομηνία: 16.08.2026 · Σχεδ.: Γεωργακόπουλος Χρ. (AM TEE 101893)

Μονοκατοικία Αμαλιάδας — Πρόταση 3: Πίνακες χώρων & έλεγχοι

Διαστάσεις: «καθαρές» = εσωτερικές ελεύθερες · «μικτές» = με τοίχους (εξωτ. πλήρες πάχος, εσωτ. μισό). Βορράς: επάνω.

■ Ισόγειο (μικτό 117,81 m², καθαρό 67,30 m²)

#	Χώρος	Καθ. εμβ. (m²)	Καθ. Α×Β (m)	Μικτές Α×Β (m)	Ζώνη
1	Καθιστικό	14,38	4,77×3,01	5,12×3,36	κύρια
2	Σαλόνι	12,78	4,24×3,01	4,34×3,36	κύρια
3	Κουζίνα	9,59	3,18×3,01	3,53×3,36	κύρια
4	Χωλ	4,00	2,67×1,50	3,02×1,60	βοηθ.
5	Αποθήκη	4,00	2,67×1,50	2,77×1,60	βοηθ.
6	WC	2,54	1,69×1,50	1,79×1,60	βοηθ.
7	Κλιμακοστάσιο	7,61	5,07×1,50	5,42×1,60	βοηθ.
8	Διάδρομος	12,40	12,40×1,00	12,50×1,10	βοηθ.

Έλεγχος φωτισμού & αερισμού (Κ.Κ. αρ. 20 §5.1.2 / αρ. 21 §5.2)

Χώρος	Εμβ.	Φως≥10%	Υαλοπ.	Αερ.≥5%	Ανοιγ.	Φως	Αερ.
Καθιστικό	14,4	1,44	1,44	0,72	0,72	✓	✓
Σαλόνι	12,8	1,28	1,28	0,64	0,64	✓	✓
Κουζίνα	9,6	0,96	1,26	0,48	0,63	✓	✓
Χωλ	4,0	0,40	0,00	0,20	0,00	✓	✓
Αποθήκη	4,0	0,40	0,00	0,20	0,00	✓	✓
WC	2,5	0,25	0,00	0,13	0,00	✓	✓
Κλιμακοστάσιο	7,6	0,76	0,00	0,38	0,00	✓	✓

→ Όλοι οι χώροι κύριας χρήσης πληρούν φωτισμό ≥10% & αερισμό ≥5%.

■ Α' Όροφος (μικτό 117,78 m², καθαρό 92,08 m²)

#	Χώρος	Καθ. εμβ. (m²)	Καθ. Α×Β (m)	Μικτές Α×Β (m)	Ζώνη
1	Κύριο Υπνοδωμάτιο	27,01	4,49×6,01	4,84×6,36	κύρια
2	Υπνοδωμάτιο 2	23,15	3,85×6,01	3,95×6,36	κύρια
3	Υπνοδωμάτιο 3	23,15	3,85×6,01	4,20×6,36	κύρια
4	Λουτρό	4,81	1,85×2,60	2,20×2,70	βοηθ.
5	Κλιμακοστάσιο	5,85	2,25×2,60	2,60×2,70	βοηθ.
6	Διάδρομος	8,10	8,10×1,00	8,20×1,10	βοηθ.

Έλεγχος φωτισμού & αερισμού (Κ.Κ. αρ. 20 §5.1.2 / αρ. 21 §5.2)

Χώρος	Εμβ.	Φως≥10%	Υαλοπ.	Αερ.≥5%	Ανοιγ.	Φως	Αερ.
Κύριο Υπνοδωμάτιο	27,0	2,70	2,70	1,35	1,35	✓	✓
Υπνοδωμάτιο 2	23,2	2,32	2,32	1,16	1,16	✓	✓
Υπνοδωμάτιο 3	23,2	2,32	2,32	1,16	1,16	✓	✓
Λουτρό	4,8	0,48	1,26	0,24	0,63	✓	✓
Κλιμακοστάσιο	5,9	0,59	0,00	0,29	0,00	✓	✓

→ Όλοι οι χώροι κύριας χρήσης πληρούν φωτισμό ≥10% & αερισμό ≥5%.

