



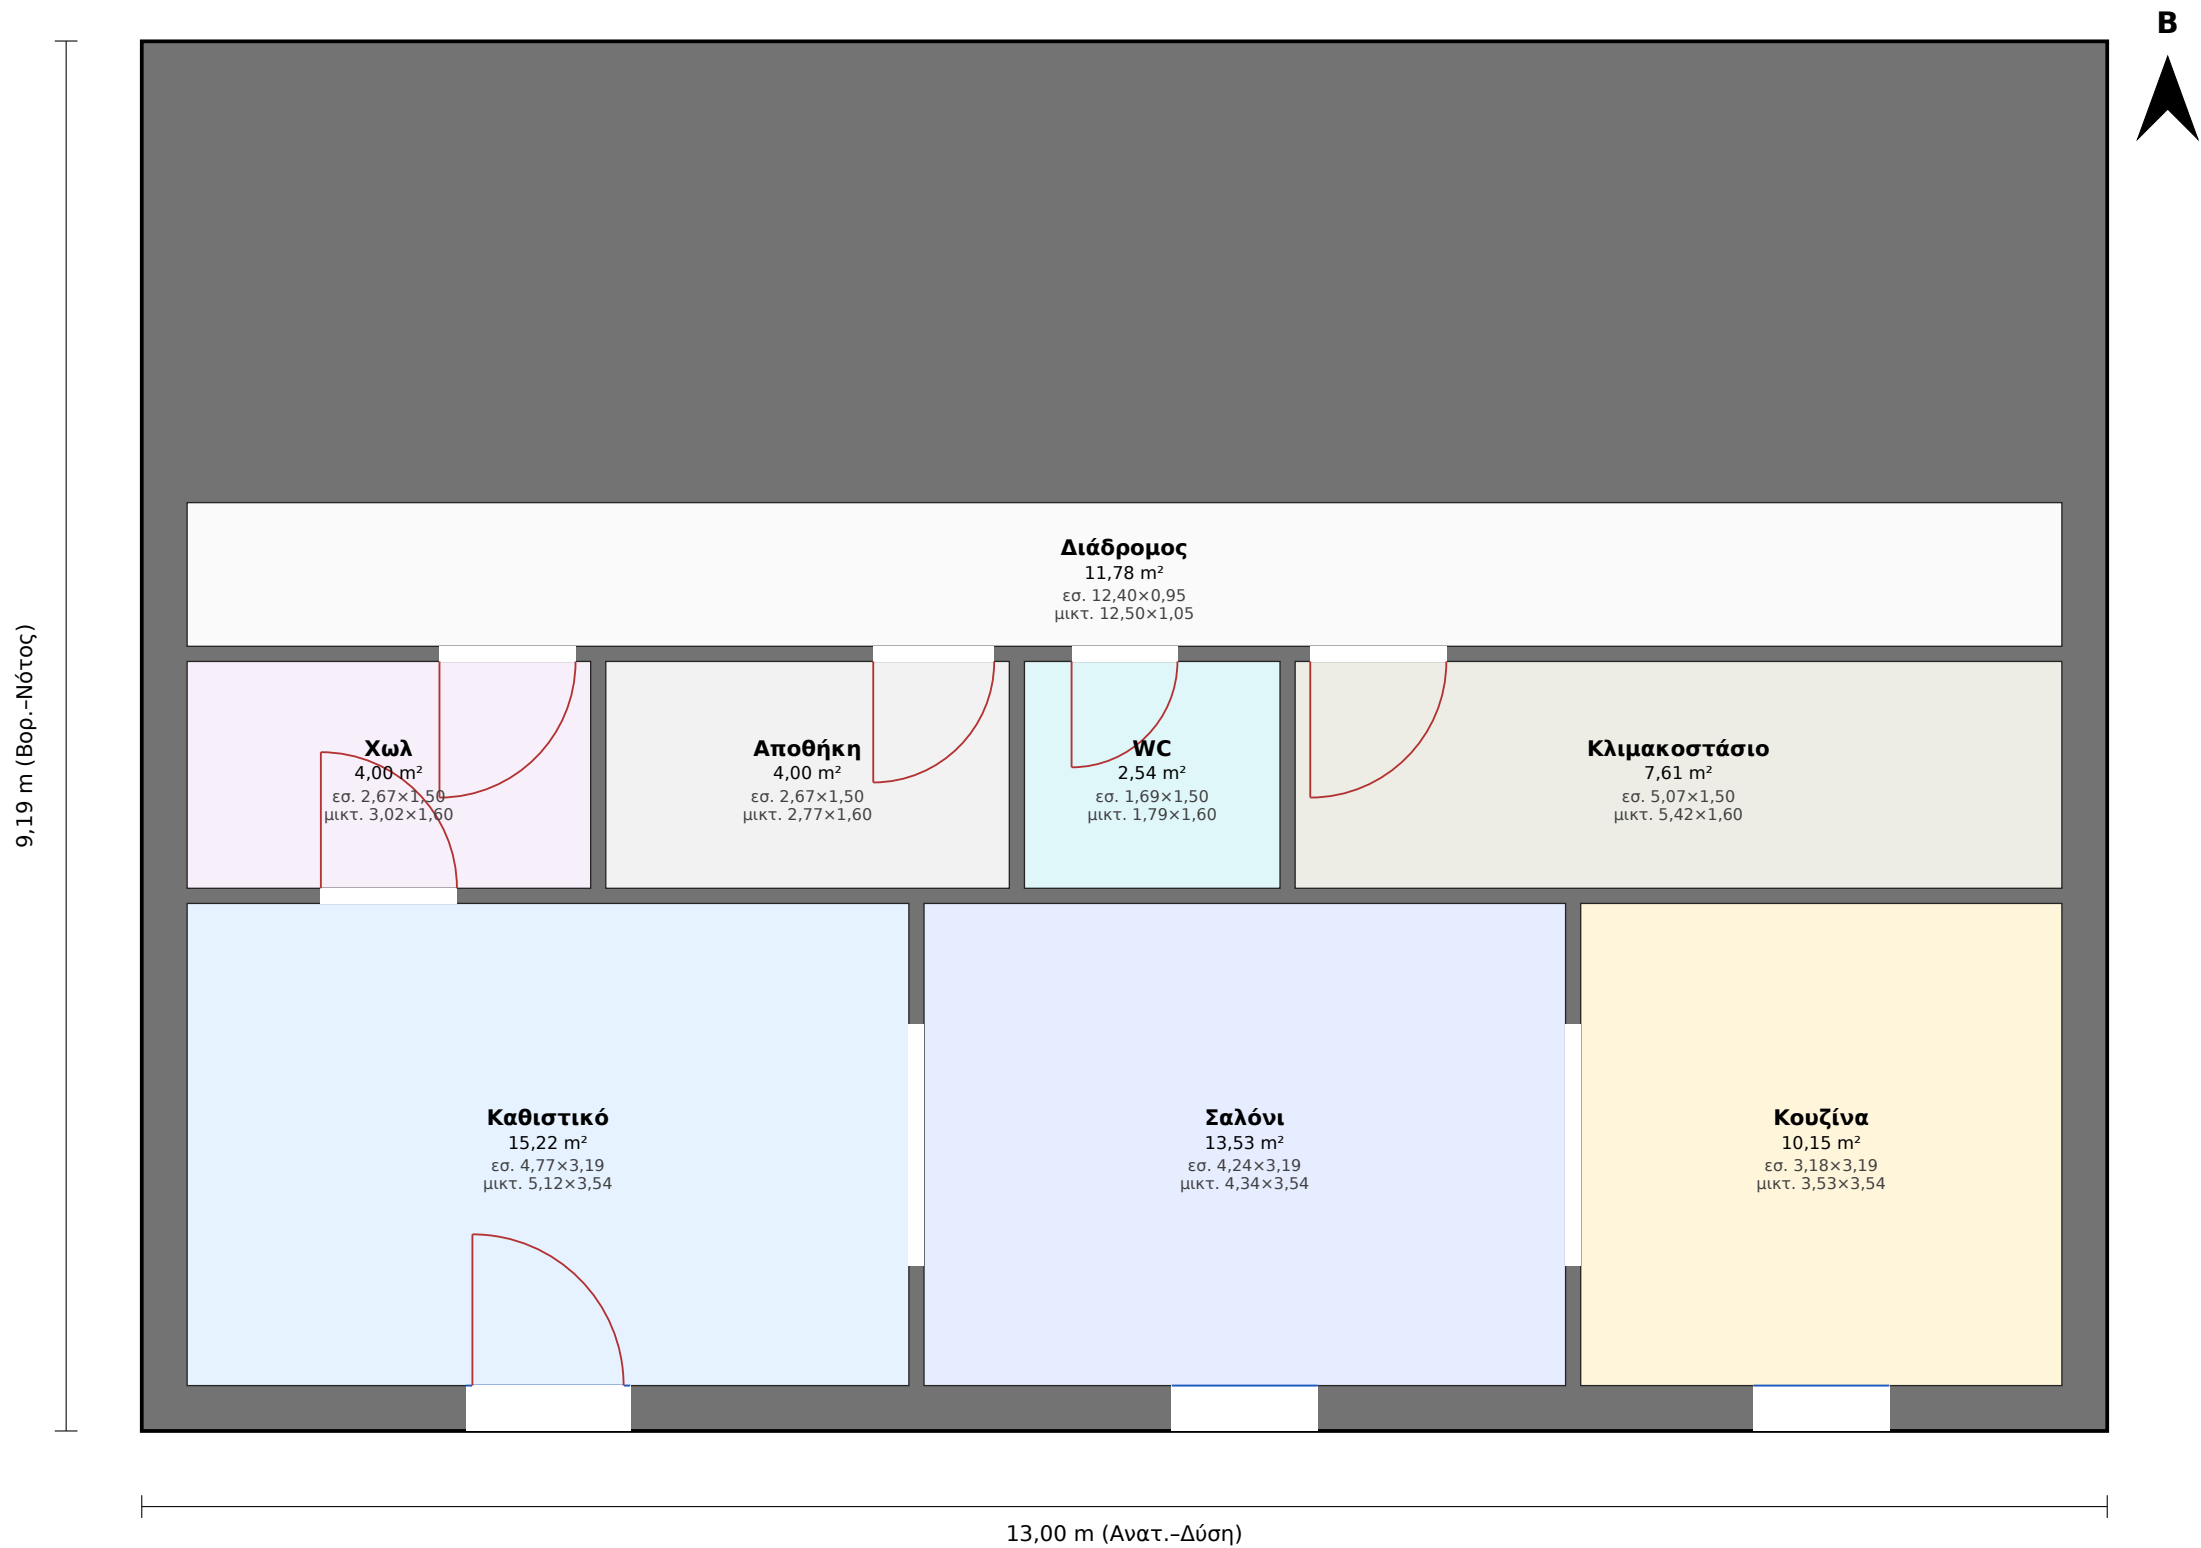

Τεχνικό Γραφείο Μελετών — Γεωργακόπουλος Χρ. / Φουντάς Αθ.
Έργο: Μονοκατοικία Αμαλιάδας
Πρόταση 1 — Ισόγειο
Κλίμακα 1:50 · Μικτό εμβ.: 119,44 m²
Είσοδος: Νότος · Αμαλιάδα, Π.Ε. Ηλείας
Ημερομηνία: 16.08.2026 · Σχεδ.: Γεωργακόπουλος Χρ. (ΑΜ ΤΕΕ 101893)

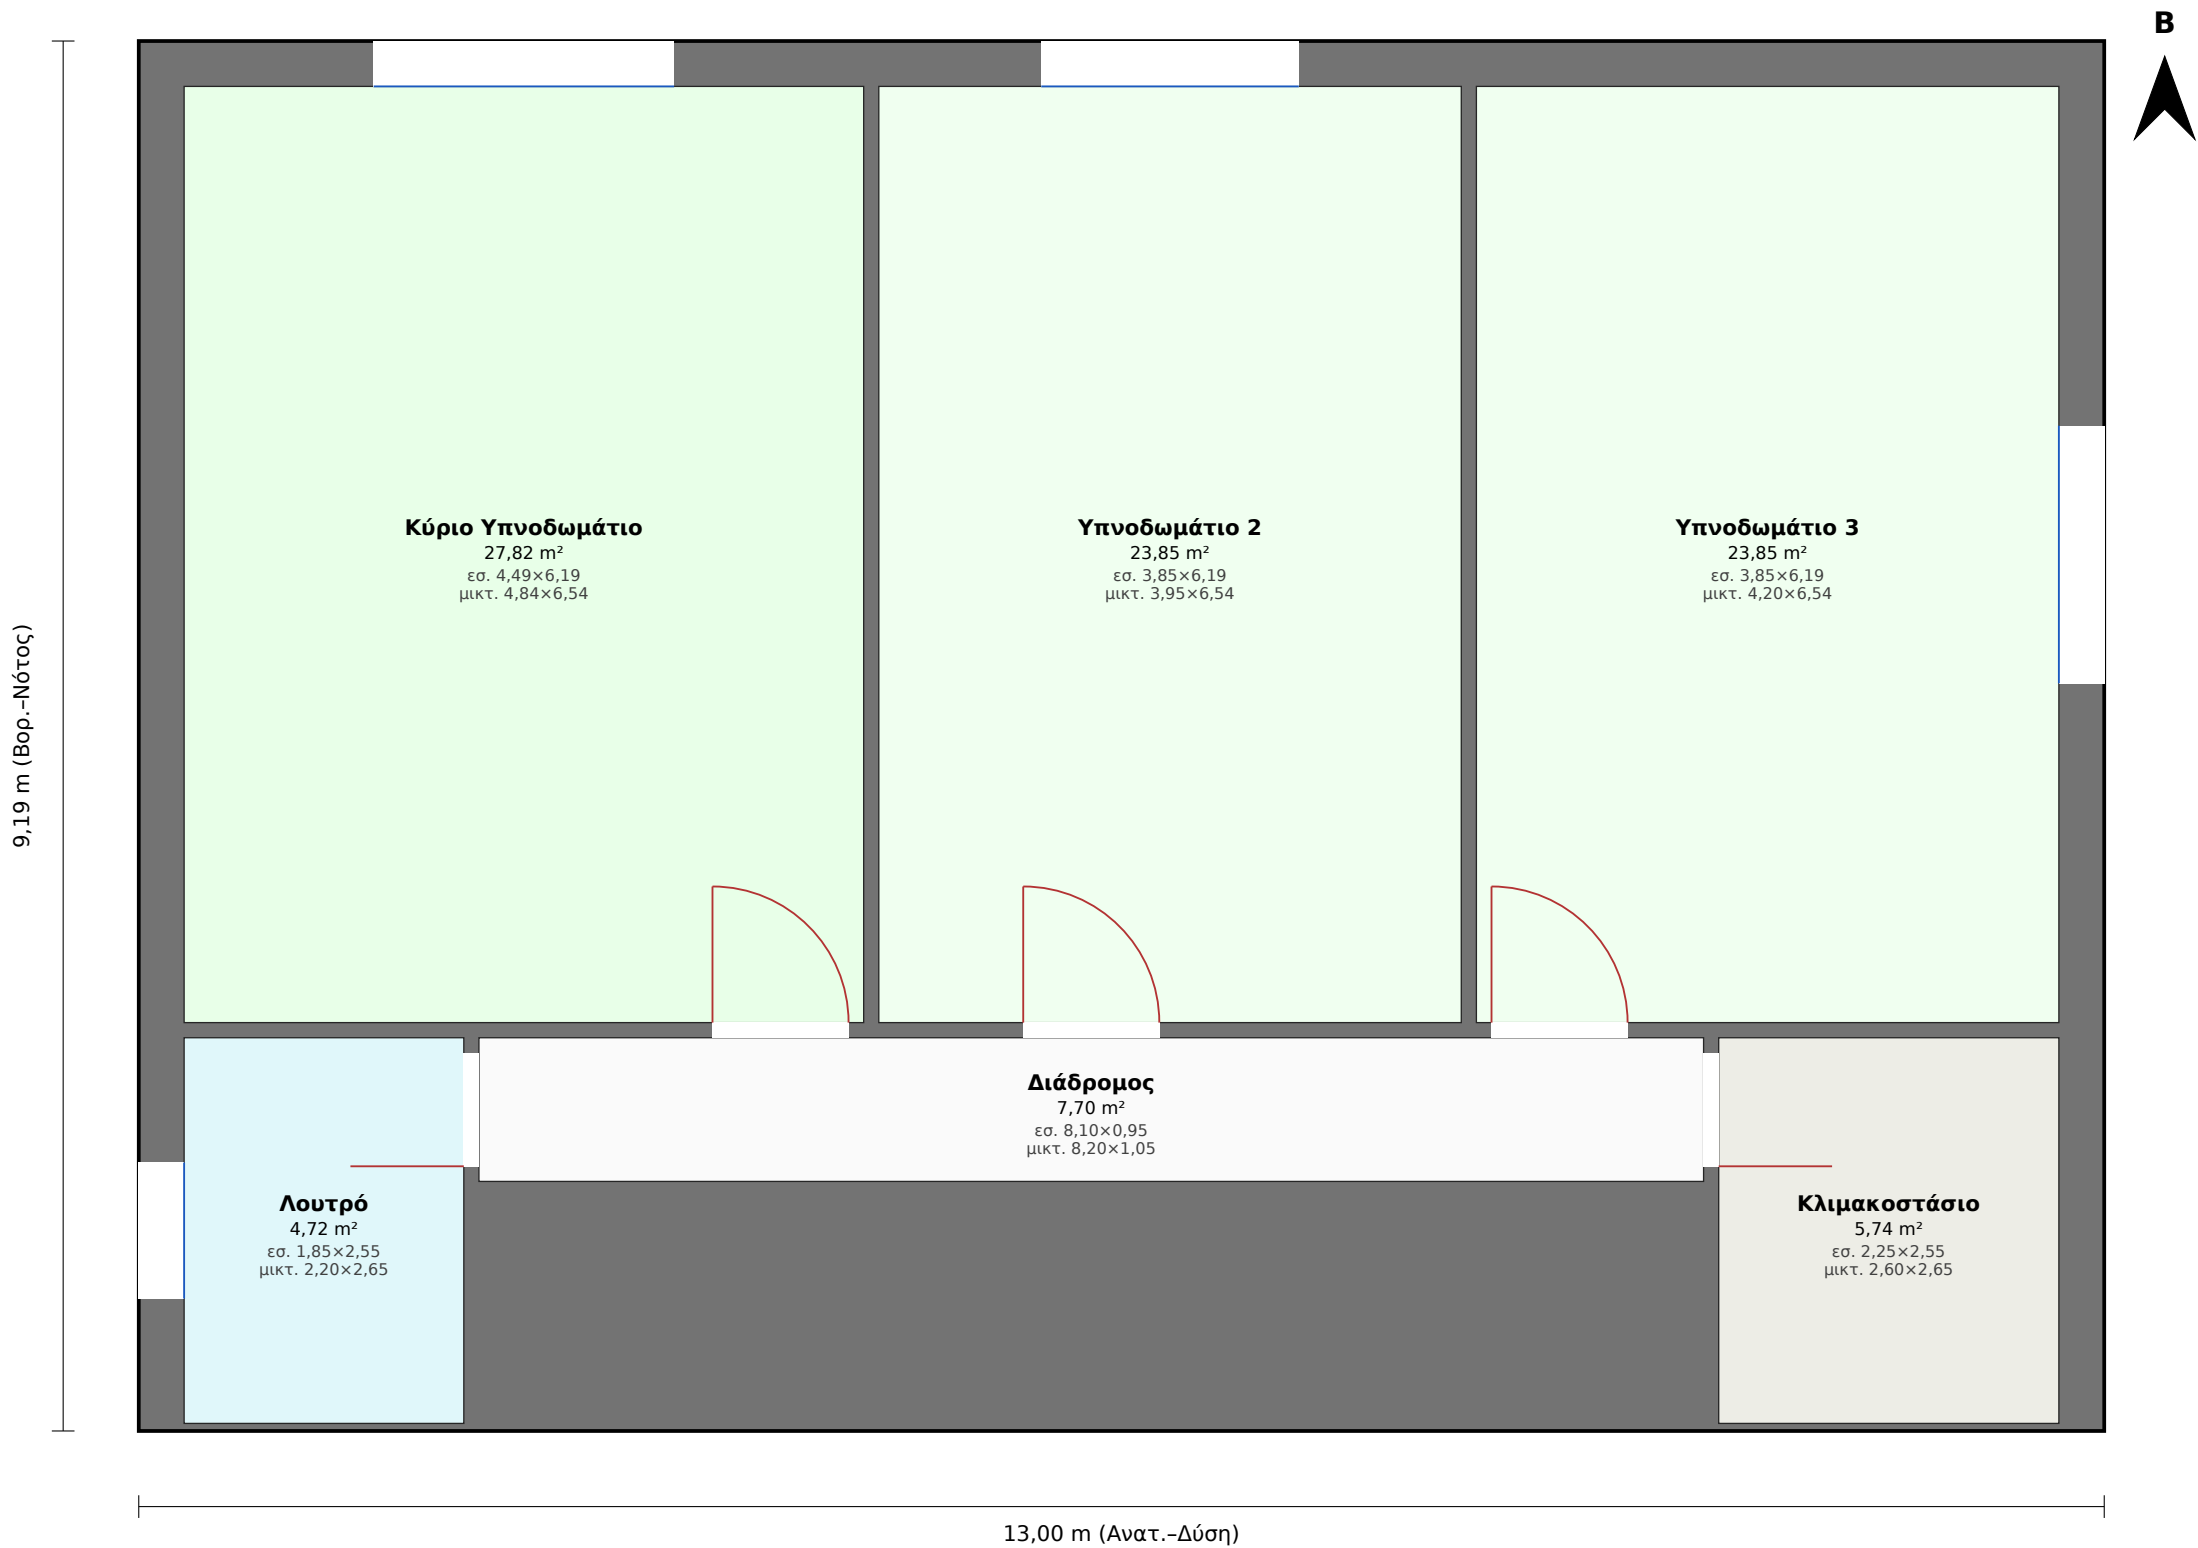

Τεχνικό Γραφείο Μελετών — Γεωργακόπουλος Χρ. / Φουντάς Αθ.
Έργο: Μονοκατοικία Αμαλιάδας
Πρόταση 1 — Α' Όροφος
Κλίμακα 1:50 · Μικτό εμβ.: 119,47 m²
Είσοδος: Νότος · Αμαλιάδα, Π.Ε. Ηλείας
Ημερομηνία: 16.08.2026 · Σχεδ.: Γεωργακόπουλος Χρ. (ΑΜ ΤΕΕ 101893)

Μονοκατοικία Αμαλιάδας — Πρόταση 1: Πίνακες χώρων & έλεγχοι

Διαστάσεις: «καθαρές» = εσωτερικές ελεύθερες · «μικτές» = με τοίχους (εξωτ. πλήρες πάχος, εσωτ. μισό). Βορράς: επάνω.

■ Ισόγειο (μικτό 119,44 m², καθαρό 68,82 m²)

#	Χώρος	Καθ. εμβ. (m²)	Καθ. Α×Β (m)	Μικτές Α×Β (m)	Ζώνη
1	Καθιστικό	15,22	4,77×3,19	5,12×3,54	κύρια
2	Σαλόνι	13,53	4,24×3,19	4,34×3,54	κύρια
3	Κουζίνα	10,15	3,18×3,19	3,53×3,54	κύρια
4	Χωλ	4,00	2,67×1,50	3,02×1,60	βοηθ.
5	Αποθήκη	4,00	2,67×1,50	2,77×1,60	βοηθ.
6	WC	2,54	1,69×1,50	1,79×1,60	βοηθ.
7	Κλιμακοστάσιο	7,61	5,07×1,50	5,42×1,60	βοηθ.
8	Διάδρομος	11,78	12,40×0,95	12,50×1,05	βοηθ.

Έλεγχος φωτισμού & αερισμού (Κ.Κ. αρ. 20 §5.1.2 / αρ. 21 §5.2)

Χώρος	Εμβ.	Φως≥10%	Υαλοπ.	Αερ.≥5%	Ανοιγ.	Φως	Αερ.
Καθιστικό	15,2	1,52	1,52	0,76	0,76	✓	✓
Σαλόνι	13,5	1,35	1,35	0,68	0,68	✓	✓
Κουζίνα	10,1	1,01	1,26	0,51	0,63	✓	✓
Χωλ	4,0	0,40	0,00	0,20	0,00	✓	✓
Αποθήκη	4,0	0,40	0,00	0,20	0,00	✓	✓
WC	2,5	0,25	0,00	0,13	0,00	✓	✓
Κλιμακοστάσιο	7,6	0,76	0,00	0,38	0,00	✓	✓

→ Όλοι οι χώροι κύριας χρήσης πληρούν φωτισμό ≥10% & αερισμό ≥5%.

■ Α' Όροφος (μικτό 119,47 m², καθαρό 93,67 m²)

#	Χώρος	Καθ. εμβ. (m²)	Καθ. Α×Β (m)	Μικτές Α×Β (m)	Ζώνη
1	Κύριο Υπνοδωμάτιο	27,82	4,49×6,19	4,84×6,54	κύρια
2	Υπνοδωμάτιο 2	23,85	3,85×6,19	3,95×6,54	κύρια
3	Υπνοδωμάτιο 3	23,85	3,85×6,19	4,20×6,54	κύρια
4	Λουτρό	4,72	1,85×2,55	2,20×2,65	βοηθ.
5	Κλιμακοστάσιο	5,74	2,25×2,55	2,60×2,65	βοηθ.
6	Διάδρομος	7,70	8,10×0,95	8,20×1,05	βοηθ.

Έλεγχος φωτισμού & αερισμού (Κ.Κ. αρ. 20 §5.1.2 / αρ. 21 §5.2)

Χώρος	Εμβ.	Φως≥10%	Υαλοπ.	Αερ.≥5%	Ανοιγ.	Φως	Αερ.
Κύριο Υπνοδωμάτιο	27,8	2,78	2,78	1,39	1,39	✓	✓
Υπνοδωμάτιο 2	23,8	2,38	2,38	1,19	1,19	✓	✓
Υπνοδωμάτιο 3	23,8	2,38	2,38	1,19	1,19	✓	✓
Λουτρό	4,7	0,47	1,26	0,24	0,63	✓	✓
Κλιμακοστάσιο	5,7	0,57	0,00	0,29	0,00	✓	✓

→ Όλοι οι χώροι κύριας χρήσης πληρούν φωτισμό ≥10% & αερισμό ≥5%.

