



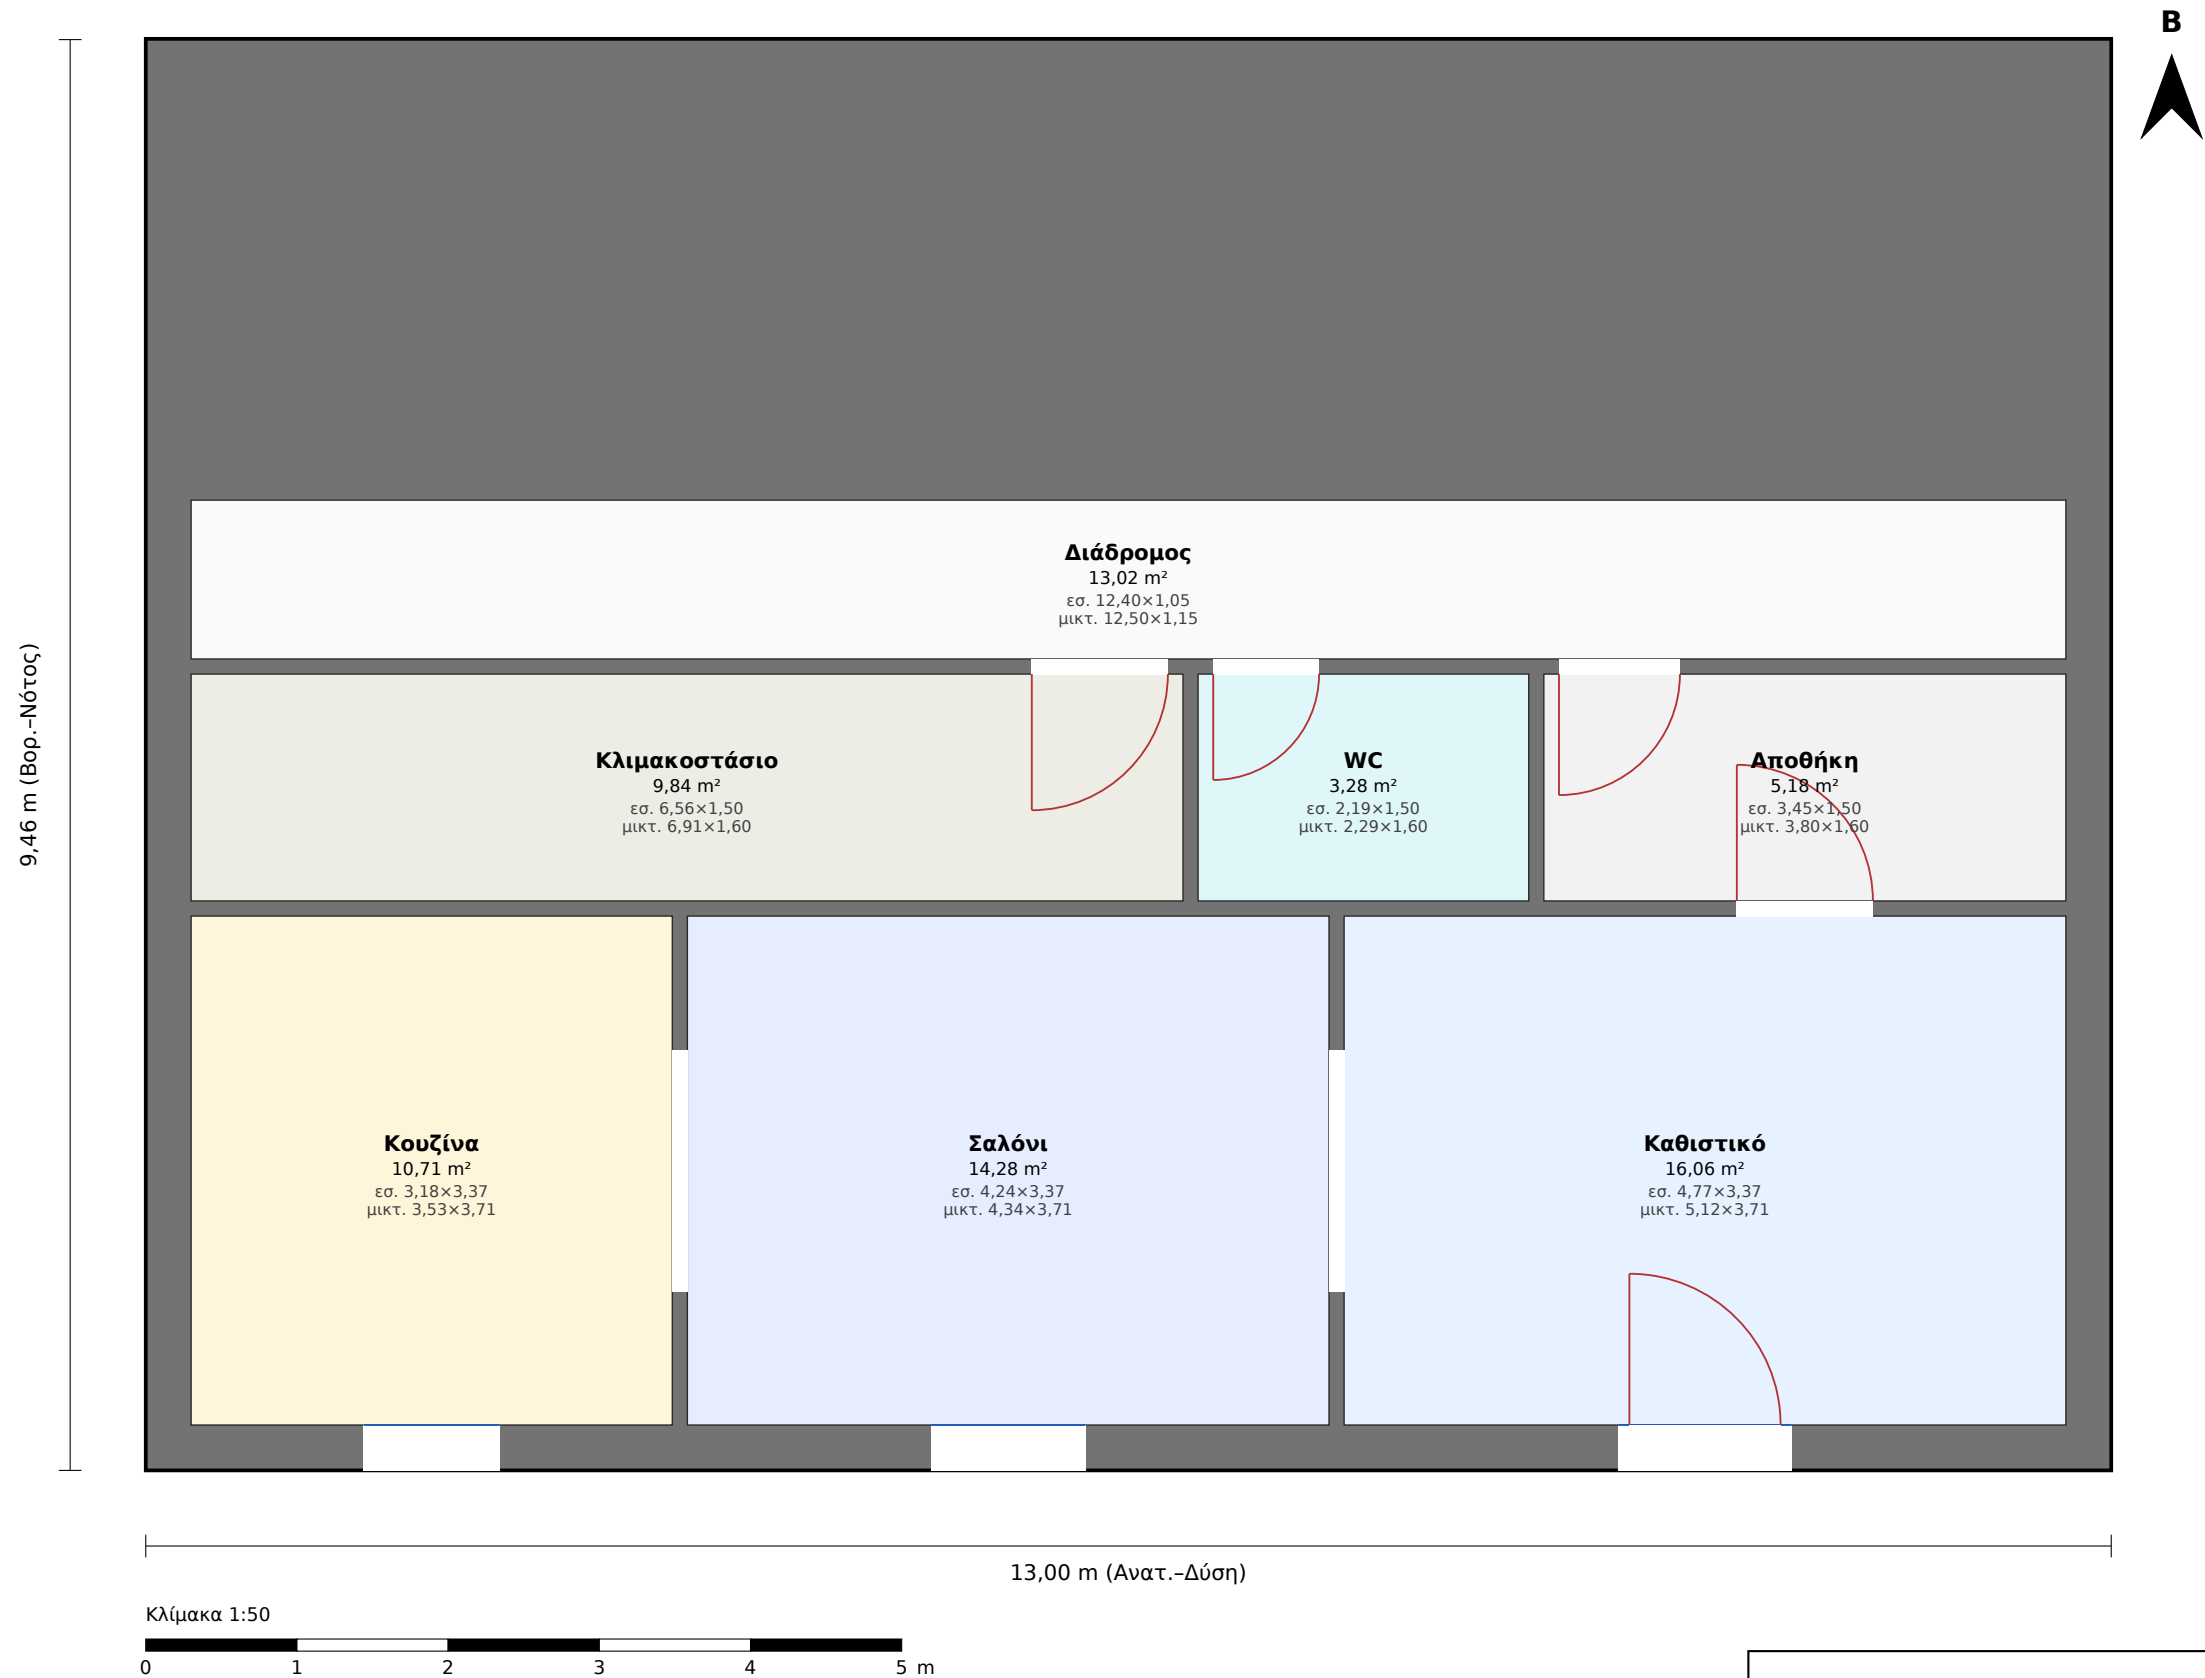

Τεχνικό Γραφείο Μελετών — Γεωργακόπουλος Χρ. / Φουντάς Αθ.
Έργο: Μονοκατοικία Αμαλιάδας
Πρόταση 2 — Ισόγειο
Κλίμακα 1:50 · Μικτό εμβ.: 123,05 m²
Είσοδος: Νότος · Αμαλιάδα, Π.Ε. Ηλείας
Ημερομηνία: 16.08.2026 · Σχεδ.: Γεωργακόπουλος Χρ. (ΑΜ ΤΕΕ 101893)

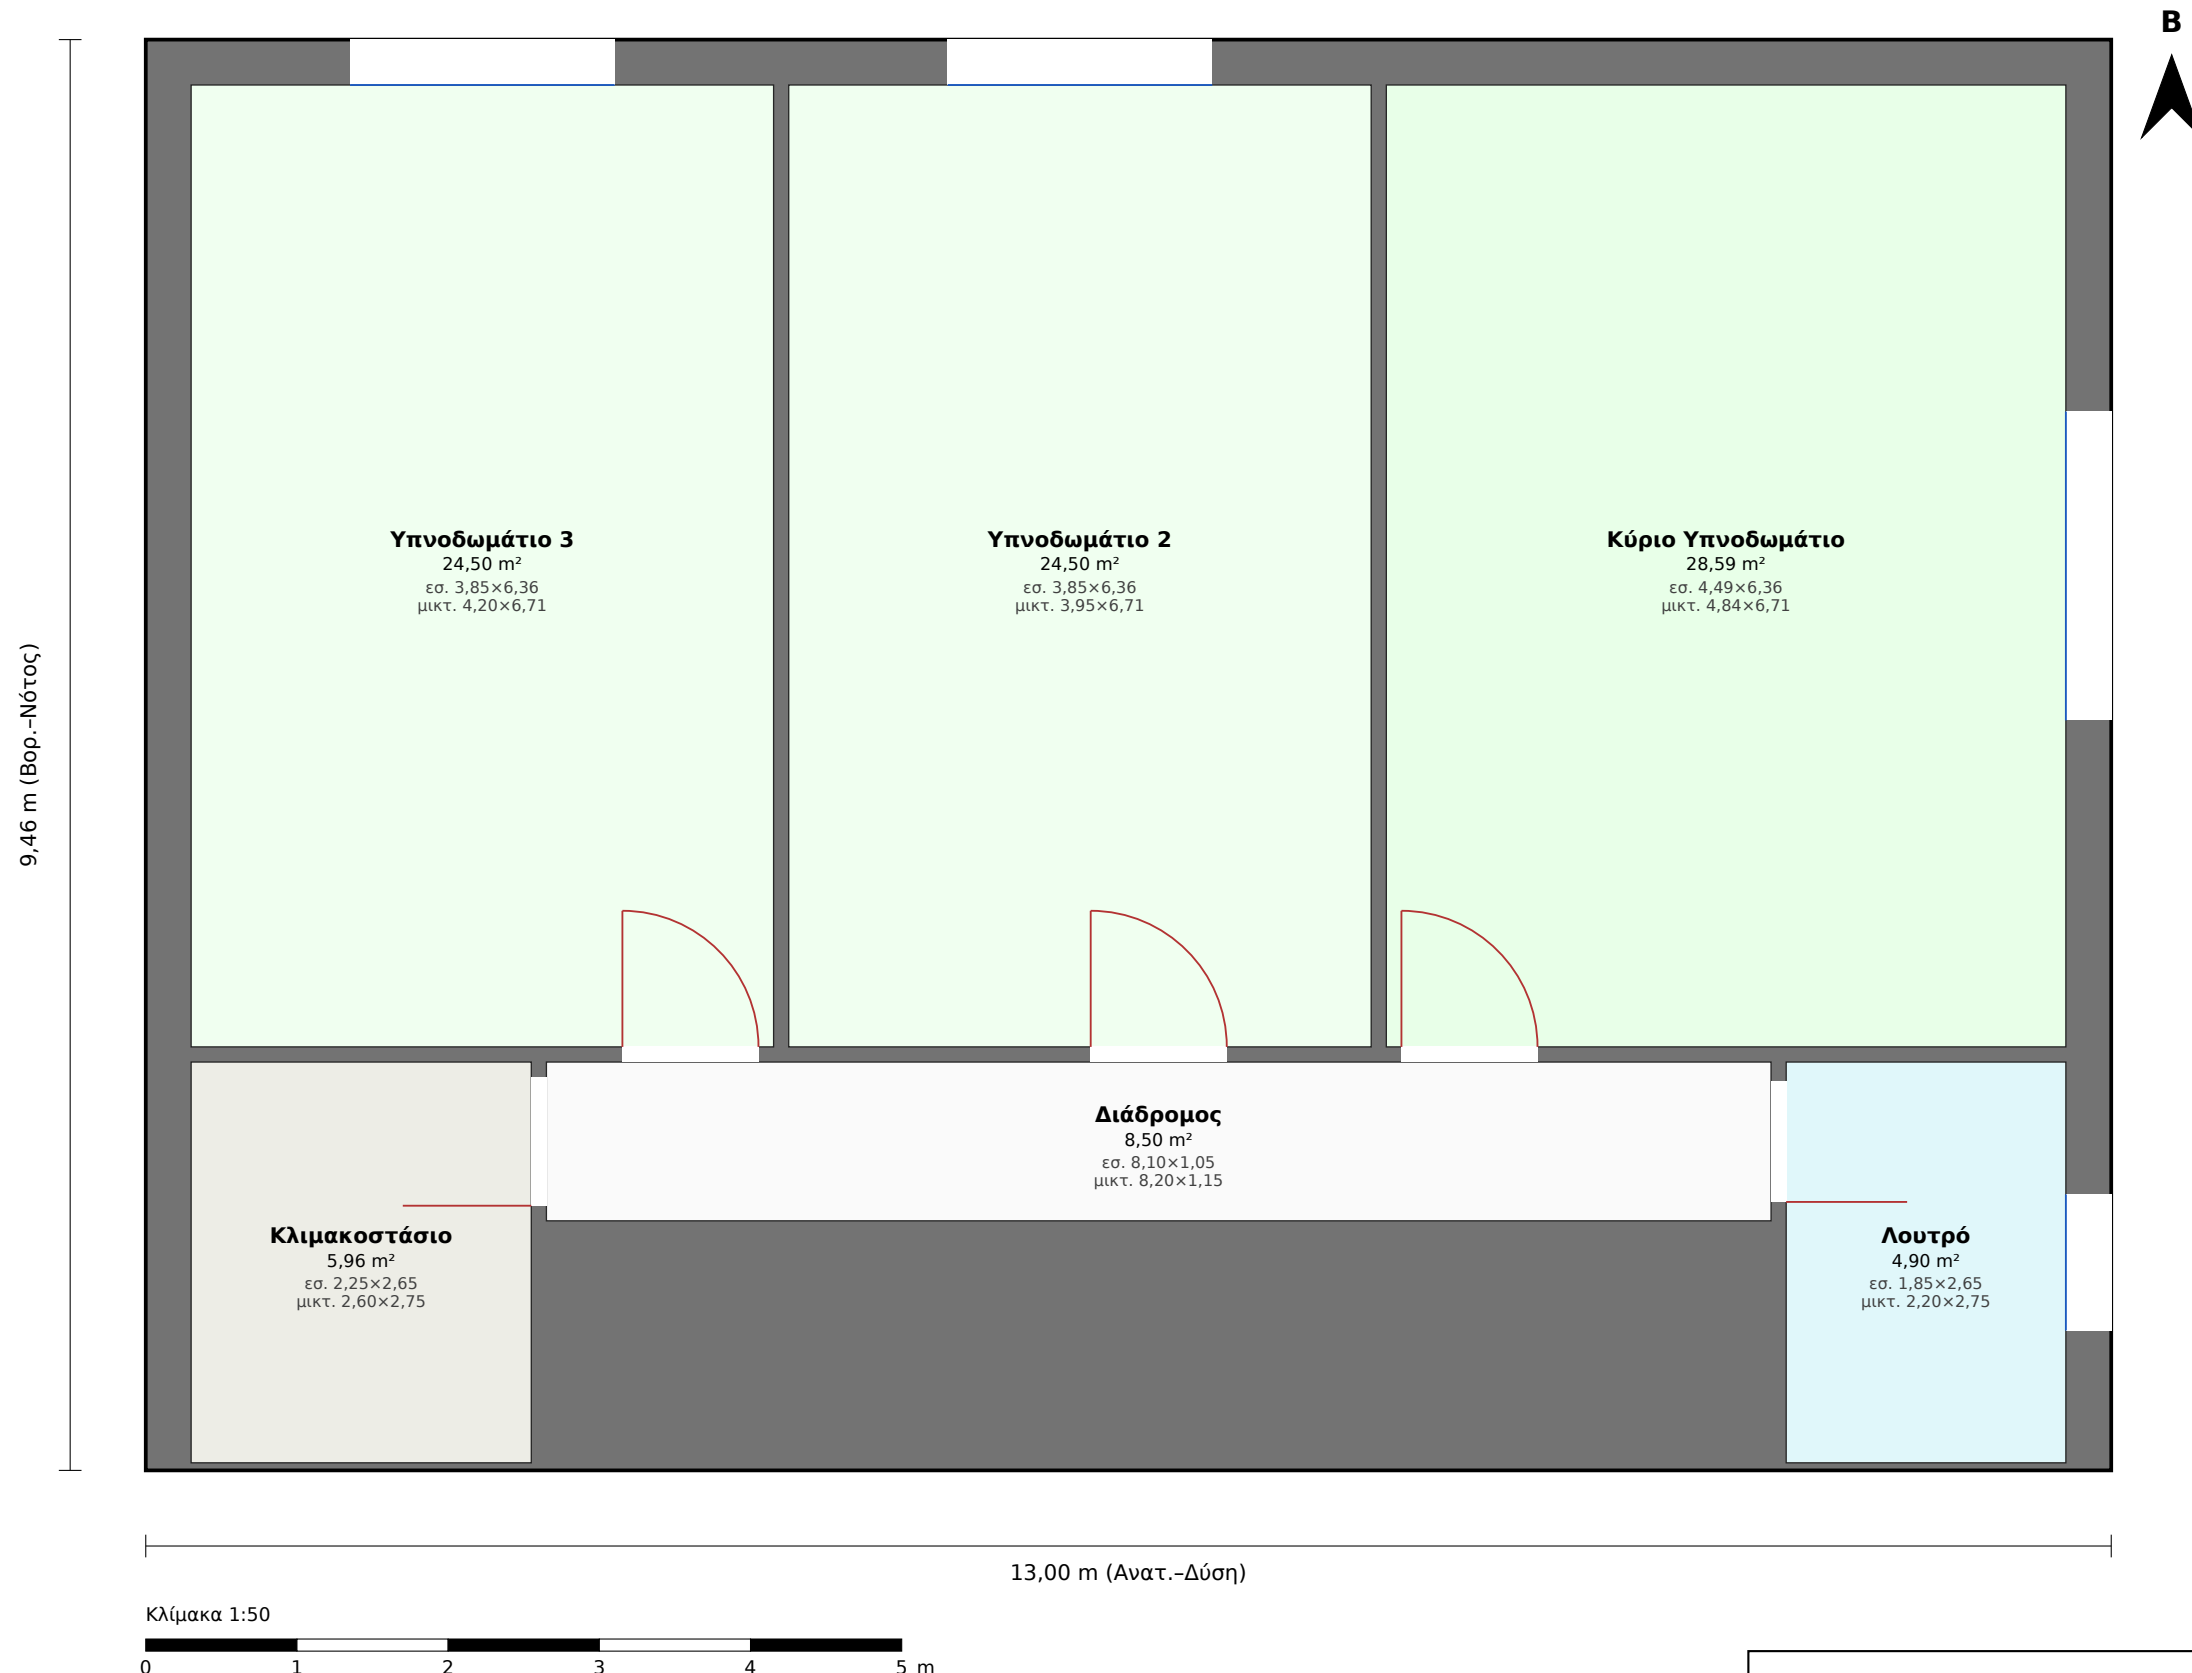

Τεχνικό Γραφείο Μελετών — Γεωργακόπουλος Χρ. / Φουντάς Αθ.
Έργο: Μονοκατοικία Αμαλιάδας
Πρόταση 2 — Α' Όροφος
Κλίμακα 1:50 · Μικτό εμβ.: 122,98 m²
Είσοδος: Νότος · Αμαλιάδα, Π.Ε. Ηλείας
Ημερομηνία: 16.08.2026 · Σχεδ.: Γεωργακόπουλος Χρ. (ΑΜ ΤΕΕ 101893)

Μονοκατοικία Αμαλιάδας — Πρόταση 2: Πίνακες χώρων & έλεγχοι

Διαστάσεις: «καθαρές» = εσωτερικές ελεύθερες · «μικτές» = με τοίχους (εξωτ. πλήρες πάχος, εσωτ. μισό). Βορράς: επάνω.

■ Ισόγειο (μικτό 123,05 m², καθαρό 72,37 m²)

#	Χώρος	Καθ. εμβ. (m²)	Καθ. Α×Β (m)	Μικτές Α×Β (m)	Ζώνη
1	Κουζίνα	10,71	3,18×3,37	3,53×3,71	κύρια
2	Σαλόνι	14,28	4,24×3,37	4,34×3,71	κύρια
3	Καθιστικό	16,06	4,77×3,37	5,12×3,71	κύρια
4	Κλιμακοστάσιο	9,84	6,56×1,50	6,91×1,60	βοηθ.
5	WC	3,28	2,19×1,50	2,29×1,60	βοηθ.
6	Αποθήκη	5,18	3,45×1,50	3,80×1,60	βοηθ.
7	Διάδρομος	13,02	12,40×1,05	12,50×1,15	βοηθ.

Έλεγχος φωτισμού & αερισμού (Κ.Κ. αρ. 20 §5.1.2 / αρ. 21 §5.2)

Χώρος	Εμβ.	Φως≥10%	Υαλοπ.	Αερ.≥5%	Ανοιγ.	Φως	Αερ.
Κουζίνα	10,7	1,07	1,26	0,54	0,63	✓	✓
Σαλόνι	14,3	1,43	1,43	0,71	0,71	✓	✓
Καθιστικό	16,1	1,61	1,61	0,80	0,80	✓	✓
Κλιμακοστάσιο	9,8	0,98	0,00	0,49	0,00	✓	✓
WC	3,3	0,33	0,00	0,16	0,00	✓	✓
Αποθήκη	5,2	0,52	0,00	0,26	0,00	✓	✓

→ Όλοι οι χώροι κύριας χρήσης πληρούν φωτισμό ≥10% & αερισμό ≥5%.

■ Α' Όροφος (μικτό 122,98 m², καθαρό 96,96 m²)

#	Χώρος	Καθ. εμβ. (m²)	Καθ. Α×Β (m)	Μικτές Α×Β (m)	Ζώνη
1	Υπνοδωμάτιο 3	24,50	3,85×6,36	4,20×6,71	κύρια
2	Υπνοδωμάτιο 2	24,50	3,85×6,36	3,95×6,71	κύρια
3	Κύριο Υπνοδωμάτιο	28,59	4,49×6,36	4,84×6,71	κύρια
4	Κλιμακοστάσιο	5,96	2,25×2,65	2,60×2,75	βοηθ.
5	Λουτρό	4,90	1,85×2,65	2,20×2,75	βοηθ.
6	Διάδρομος	8,50	8,10×1,05	8,20×1,15	βοηθ.

Έλεγχος φωτισμού & αερισμού (Κ.Κ. αρ. 20 §5.1.2 / αρ. 21 §5.2)

Χώρος	Εμβ.	Φως≥10%	Υαλοπ.	Αερ.≥5%	Ανοιγ.	Φως	Αερ.
Υπνοδωμάτιο 3	24,5	2,45	2,45	1,23	1,23	✓	✓
Υπνοδωμάτιο 2	24,5	2,45	2,45	1,23	1,23	✓	✓
Κύριο Υπνοδωμάτιο	28,6	2,86	2,86	1,43	1,43	✓	✓
Κλιμακοστάσιο	6,0	0,60	0,00	0,30	0,00	✓	✓
Λουτρό	4,9	0,49	1,26	0,25	0,63	✓	✓

→ Όλοι οι χώροι κύριας χρήσης πληρούν φωτισμό ≥10% & αερισμό ≥5%.