



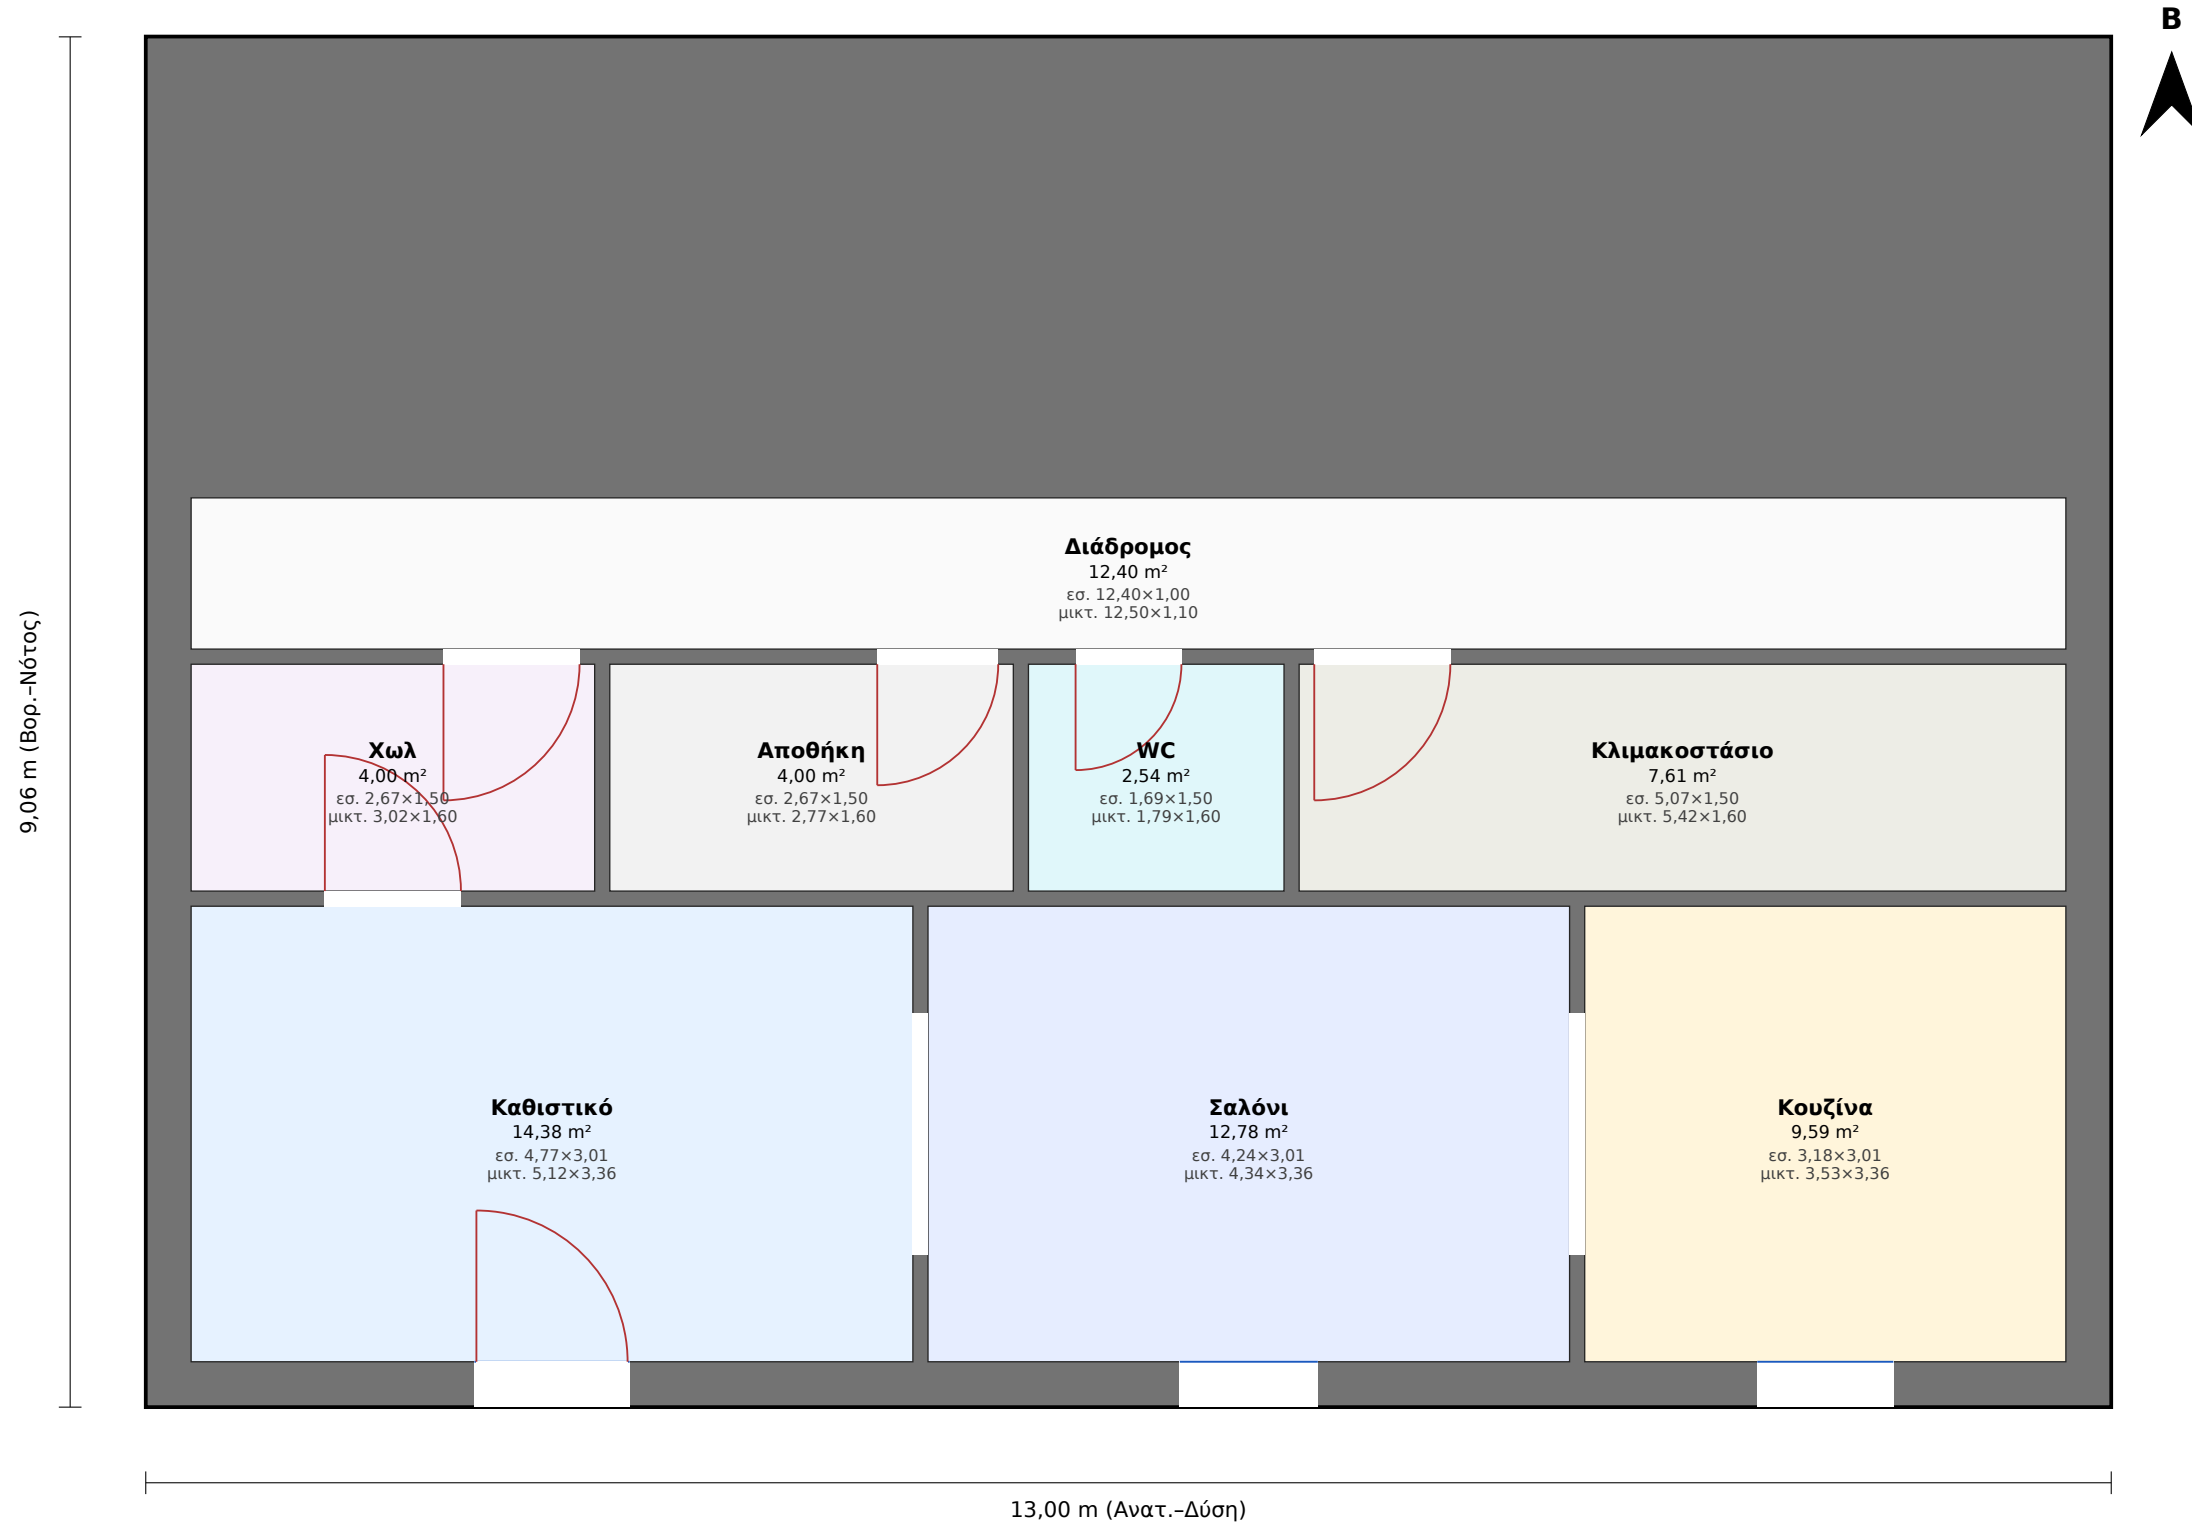

Τεχνικό Γραφείο Μελετών — Γεωργακόπουλος Χρ. / Φουντάς Αθ.
Έργο: Μονοκατοικία Αμαλιάδας
Πρόταση 3 — Ισόγειο
Κλίμακα 1:50 · Μικτό εμβ.: 117,81 m²
Είσοδος: Νότος · Αμαλιάδα, Π.Ε. Ηλείας
Ημερομηνία: 16.08.2026 · Σχεδ.: Γεωργακόπουλος Χρ. (AM TEE 101893)

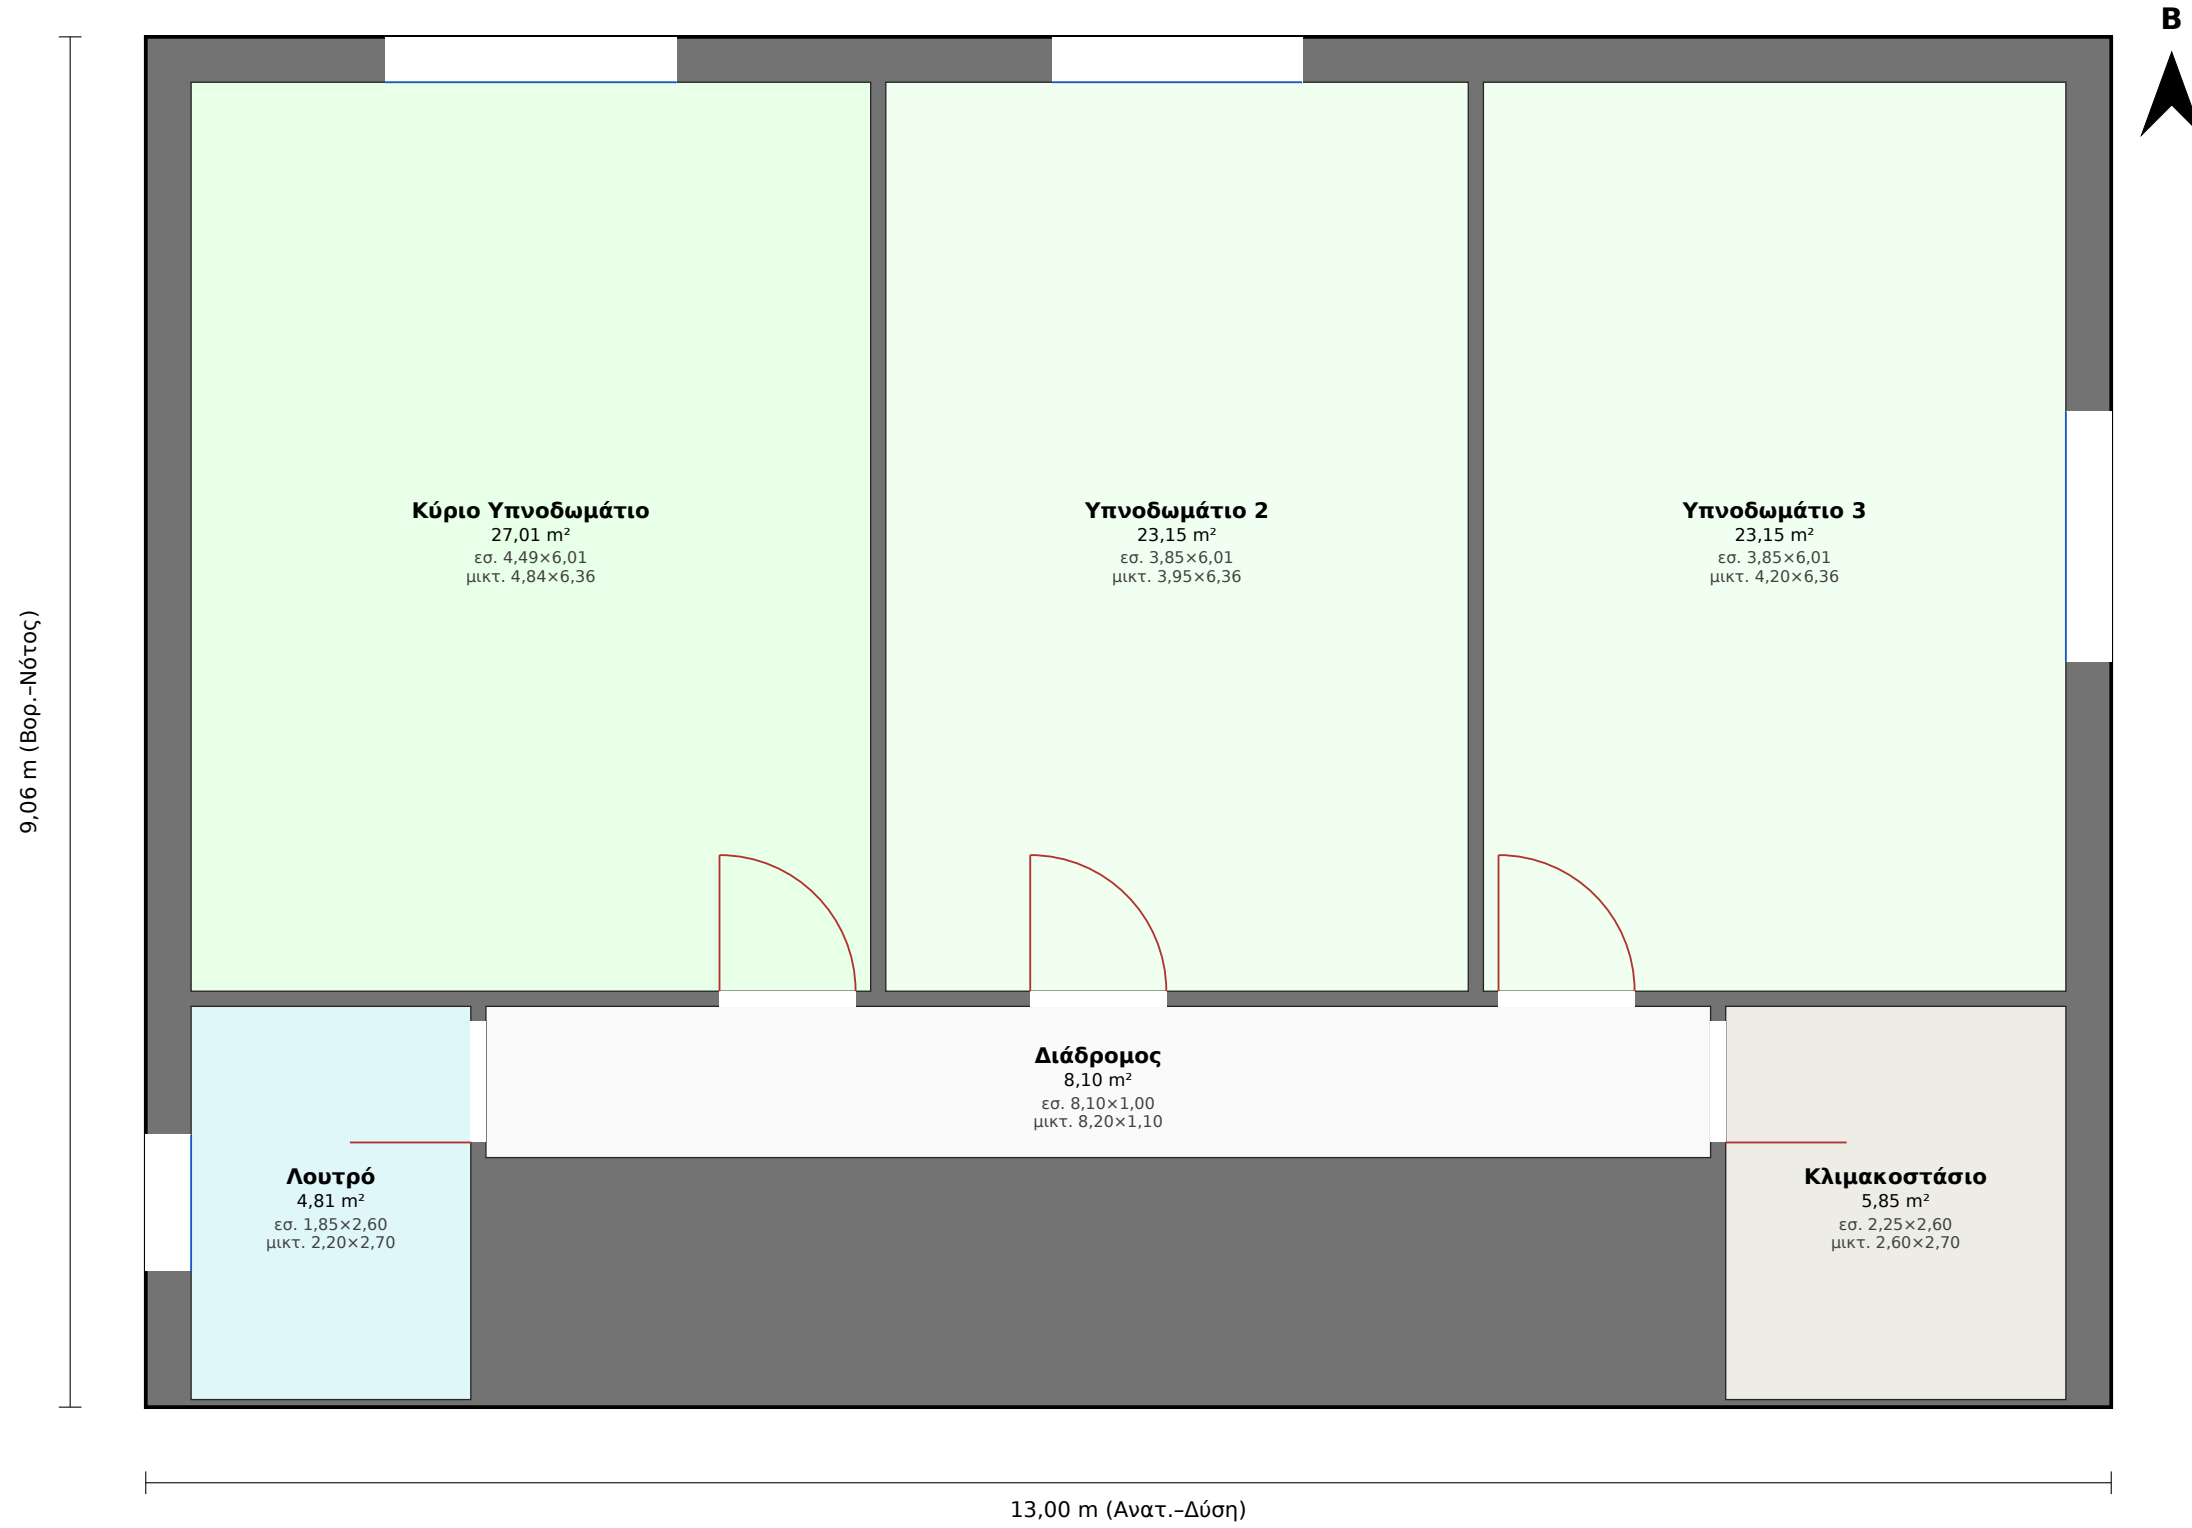

Τεχνικό Γραφείο Μελετών — Γεωργακόπουλος Χρ. / Φουντάς Αθ.
Έργο: Μονοκατοικία Αμαλιάδας
Πρόταση 3 — Α' Όροφος
Κλίμακα 1:50 · Μικτό εμβ.: 117,78 m²
Είσοδος: Νότος · Αμαλιάδα, Π.Ε. Ηλείας
Ημερομηνία: 16.08.2026 · Σχεδ.: Γεωργακόπουλος Χρ. (AM TEE 101893)

Μονοκατοικία Αμαλιάδας — Πρόταση 3: Πίνακες χώρων & έλεγχοι

Διαστάσεις: «καθαρές» = εσωτερικές ελεύθερες · «μικτές» = με τοίχους (εξωτ. πλήρες πάχος, εσωτ. μισό). Βορράς: επάνω.

■ Ισόγειο (μικτό 117,81 m², καθαρό 67,30 m²)

#	Χώρος	Καθ. εμβ. (m²)	Καθ. Α×Β (m)	Μικτές Α×Β (m)	Ζώνη
1	Καθιστικό	14,38	4,77×3,01	5,12×3,36	κύρια
2	Σαλόνι	12,78	4,24×3,01	4,34×3,36	κύρια
3	Κουζίνα	9,59	3,18×3,01	3,53×3,36	κύρια
4	Χωλ	4,00	2,67×1,50	3,02×1,60	βοηθ.
5	Αποθήκη	4,00	2,67×1,50	2,77×1,60	βοηθ.
6	WC	2,54	1,69×1,50	1,79×1,60	βοηθ.
7	Κλιμακοστάσιο	7,61	5,07×1,50	5,42×1,60	βοηθ.
8	Διάδρομος	12,40	12,40×1,00	12,50×1,10	βοηθ.

Έλεγχος φωτισμού & αερισμού (Κ.Κ. αρ. 20 §5.1.2 / αρ. 21 §5.2)

Χώρος	Εμβ.	Φως≥10%	Υαλοπ.	Αερ.≥5%	Ανοιγ.	Φως	Αερ.
Καθιστικό	14,4	1,44	1,44	0,72	0,72	✓	✓
Σαλόνι	12,8	1,28	1,28	0,64	0,64	✓	✓
Κουζίνα	9,6	0,96	1,26	0,48	0,63	✓	✓
Χωλ	4,0	0,40	0,00	0,20	0,00	✓	✓
Αποθήκη	4,0	0,40	0,00	0,20	0,00	✓	✓
WC	2,5	0,25	0,00	0,13	0,00	✓	✓
Κλιμακοστάσιο	7,6	0,76	0,00	0,38	0,00	✓	✓

→ Όλοι οι χώροι κύριας χρήσης πληρούν φωτισμό ≥10% & αερισμό ≥5%.

■ Α' Όροφος (μικτό 117,78 m², καθαρό 92,08 m²)

#	Χώρος	Καθ. εμβ. (m²)	Καθ. Α×Β (m)	Μικτές Α×Β (m)	Ζώνη
1	Κύριο Υπνοδωμάτιο	27,01	4,49×6,01	4,84×6,36	κύρια
2	Υπνοδωμάτιο 2	23,15	3,85×6,01	3,95×6,36	κύρια
3	Υπνοδωμάτιο 3	23,15	3,85×6,01	4,20×6,36	κύρια
4	Λουτρό	4,81	1,85×2,60	2,20×2,70	βοηθ.
5	Κλιμακοστάσιο	5,85	2,25×2,60	2,60×2,70	βοηθ.
6	Διάδρομος	8,10	8,10×1,00	8,20×1,10	βοηθ.

Έλεγχος φωτισμού & αερισμού (Κ.Κ. αρ. 20 §5.1.2 / αρ. 21 §5.2)

Χώρος	Εμβ.	Φως≥10%	Υαλοπ.	Αερ.≥5%	Ανοιγ.	Φως	Αερ.
Κύριο Υπνοδωμάτιο	27,0	2,70	2,70	1,35	1,35	✓	✓
Υπνοδωμάτιο 2	23,2	2,32	2,32	1,16	1,16	✓	✓
Υπνοδωμάτιο 3	23,2	2,32	2,32	1,16	1,16	✓	✓
Λουτρό	4,8	0,48	1,26	0,24	0,63	✓	✓
Κλιμακοστάσιο	5,9	0,59	0,00	0,29	0,00	✓	✓

→ Όλοι οι χώροι κύριας χρήσης πληρούν φωτισμό ≥10% & αερισμό ≥5%.

