


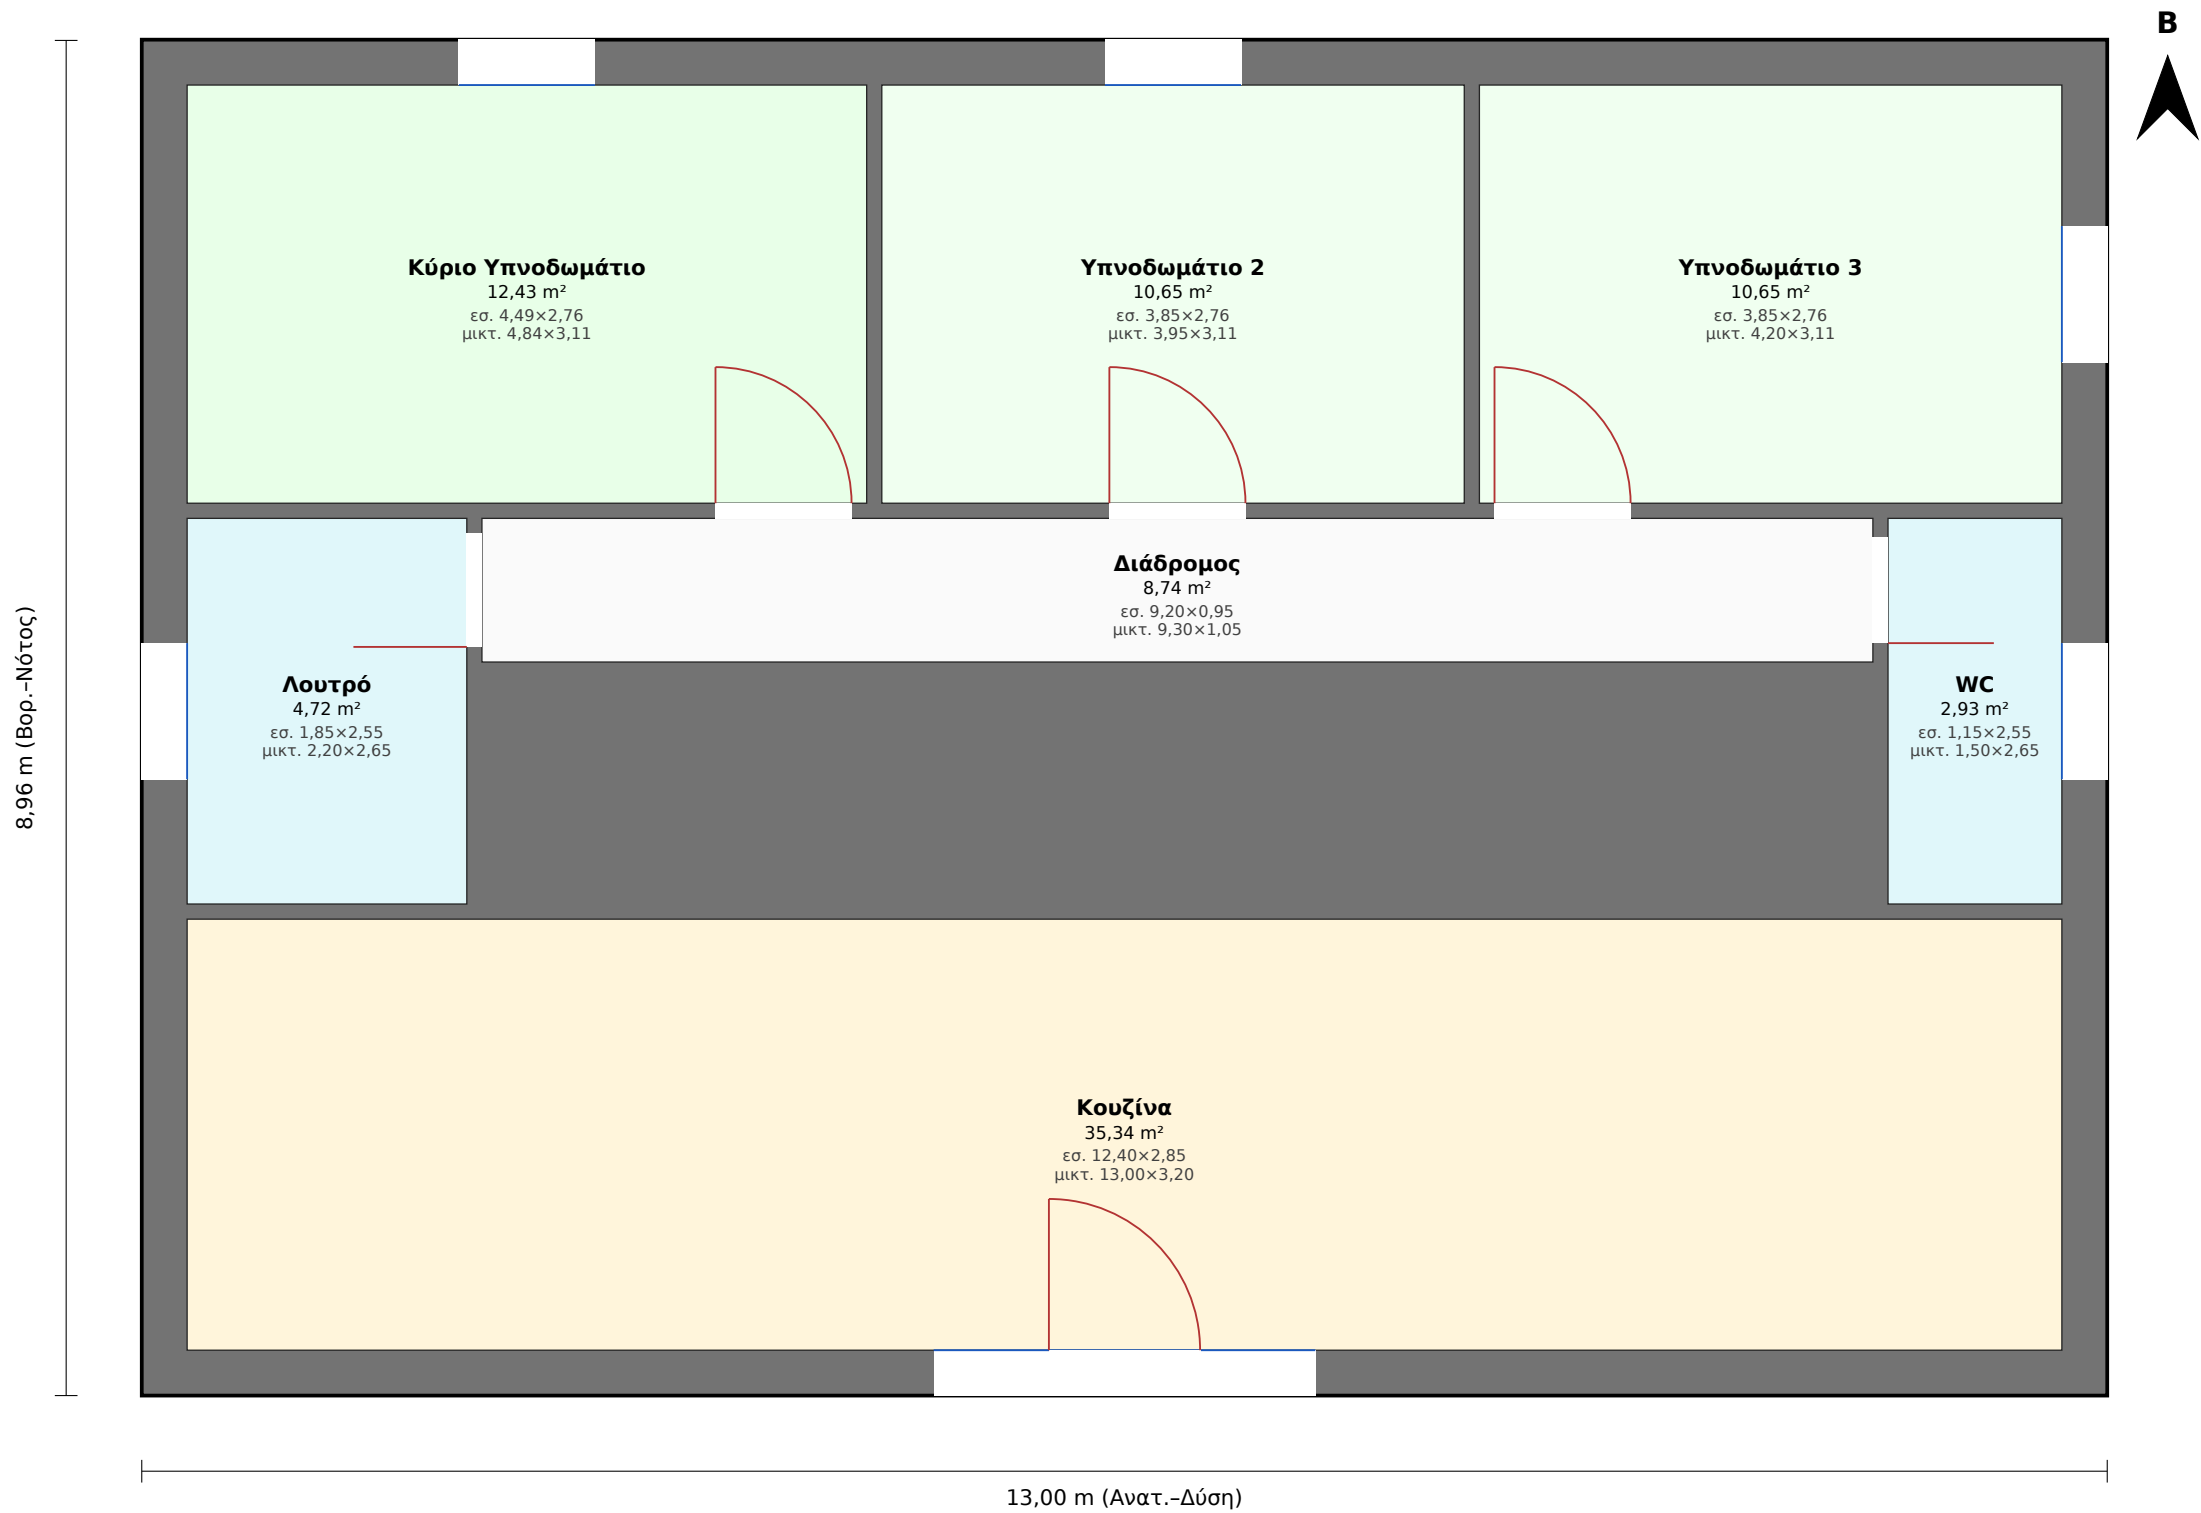

Τεχνικό Γραφείο Μελετών — Γεωργακόπουλος Χρ. / Φουντάς Αθ.
Έργο: Κατοικία
Πρόταση 1 — Ισόγειο
Κλίμακα 1:50 · Μικτό εμβ.: 116,55 m²
Είσοδος: Νότος · Αμαλιάδα, Π.Ε. Ηλείας
Ημερομηνία: 16.08.2026 · Σχεδ.: Γεωργακόπουλος Χρ. (AM TEE 101893)

Κατοικία — Πρόταση 1: Πίνακες χώρων & έλεγχοι

Διαστάσεις: «καθαρές» = εσωτερικές ελεύθερες · «μικτές» = με τοίχους (εξωτ. πλήρες πάχος, εσωτ. μισό). Βορράς: επάνω.

■ Ισόγειο (μικτό 116,55 m², καθαρό 85,46 m²)

#	Χώρος	Καθ. εμβ. (m²)	Καθ. Α×Β (m)	Μικτές Α×Β (m)	Ζώνη
1	Κουζίνα	35,34	12,40×2,85	13,00×3,20	κύρια
2	Κύριο Υπνοδωμάτιο	12,43	4,49×2,76	4,84×3,11	κύρια
3	Υπνοδωμάτιο 2	10,65	3,85×2,76	3,95×3,11	κύρια
4	Υπνοδωμάτιο 3	10,65	3,85×2,76	4,20×3,11	κύρια
5	Λουτρό	4,72	1,85×2,55	2,20×2,65	βοηθ.
6	WC	2,93	1,15×2,55	1,50×2,65	βοηθ.
7	Διάδρομος	8,74	9,20×0,95	9,30×1,05	βοηθ.


Έλεγχος φωτισμού & αερισμού (Κ.Κ. αρ. 20 §5.1.2 / αρ. 21 §5.2)

Χώρος	Εμβ.	Φως≥10%	Υαλοπ.	Αερ.≥5%	Ανοιγ.	Φως	Αερ.
Κουζίνα	35,3	3,53	3,53	1,77	1,77	✓	✓
Κύριο Υπνοδωμάτιο	12,4	1,24	1,26	0,62	0,63	✓	✓
Υπνοδωμάτιο 2	10,7	1,07	1,26	0,53	0,63	✓	✓
Υπνοδωμάτιο 3	10,7	1,07	1,26	0,53	0,63	✓	✓
Λουτρό	4,7	0,47	1,26	0,24	0,63	✓	✓
WC	2,9	0,29	1,26	0,15	0,63	✓	✓

→ Όλοι οι χώροι κύριας χρήσης πληρούν φωτισμό ≥10% & αερισμό ≥5%.

Παρατηρήσεις / περιορισμοί:

- [Ισόγειο] Κύριο Υπνοδωμάτιο: 4.49×2.76 m — ελάχιστη πλευρά κάτω από 3.00 m (στενό περίγραμμα).
- [Ισόγειο] Υπνοδωμάτιο 2: 3.85×2.76 m — ελάχιστη πλευρά κάτω από 3.00 m (στενό περίγραμμα).
- [Ισόγειο] Υπνοδωμάτιο 3: 3.85×2.76 m — ελάχιστη πλευρά κάτω από 3.00 m (στενό περίγραμμα).

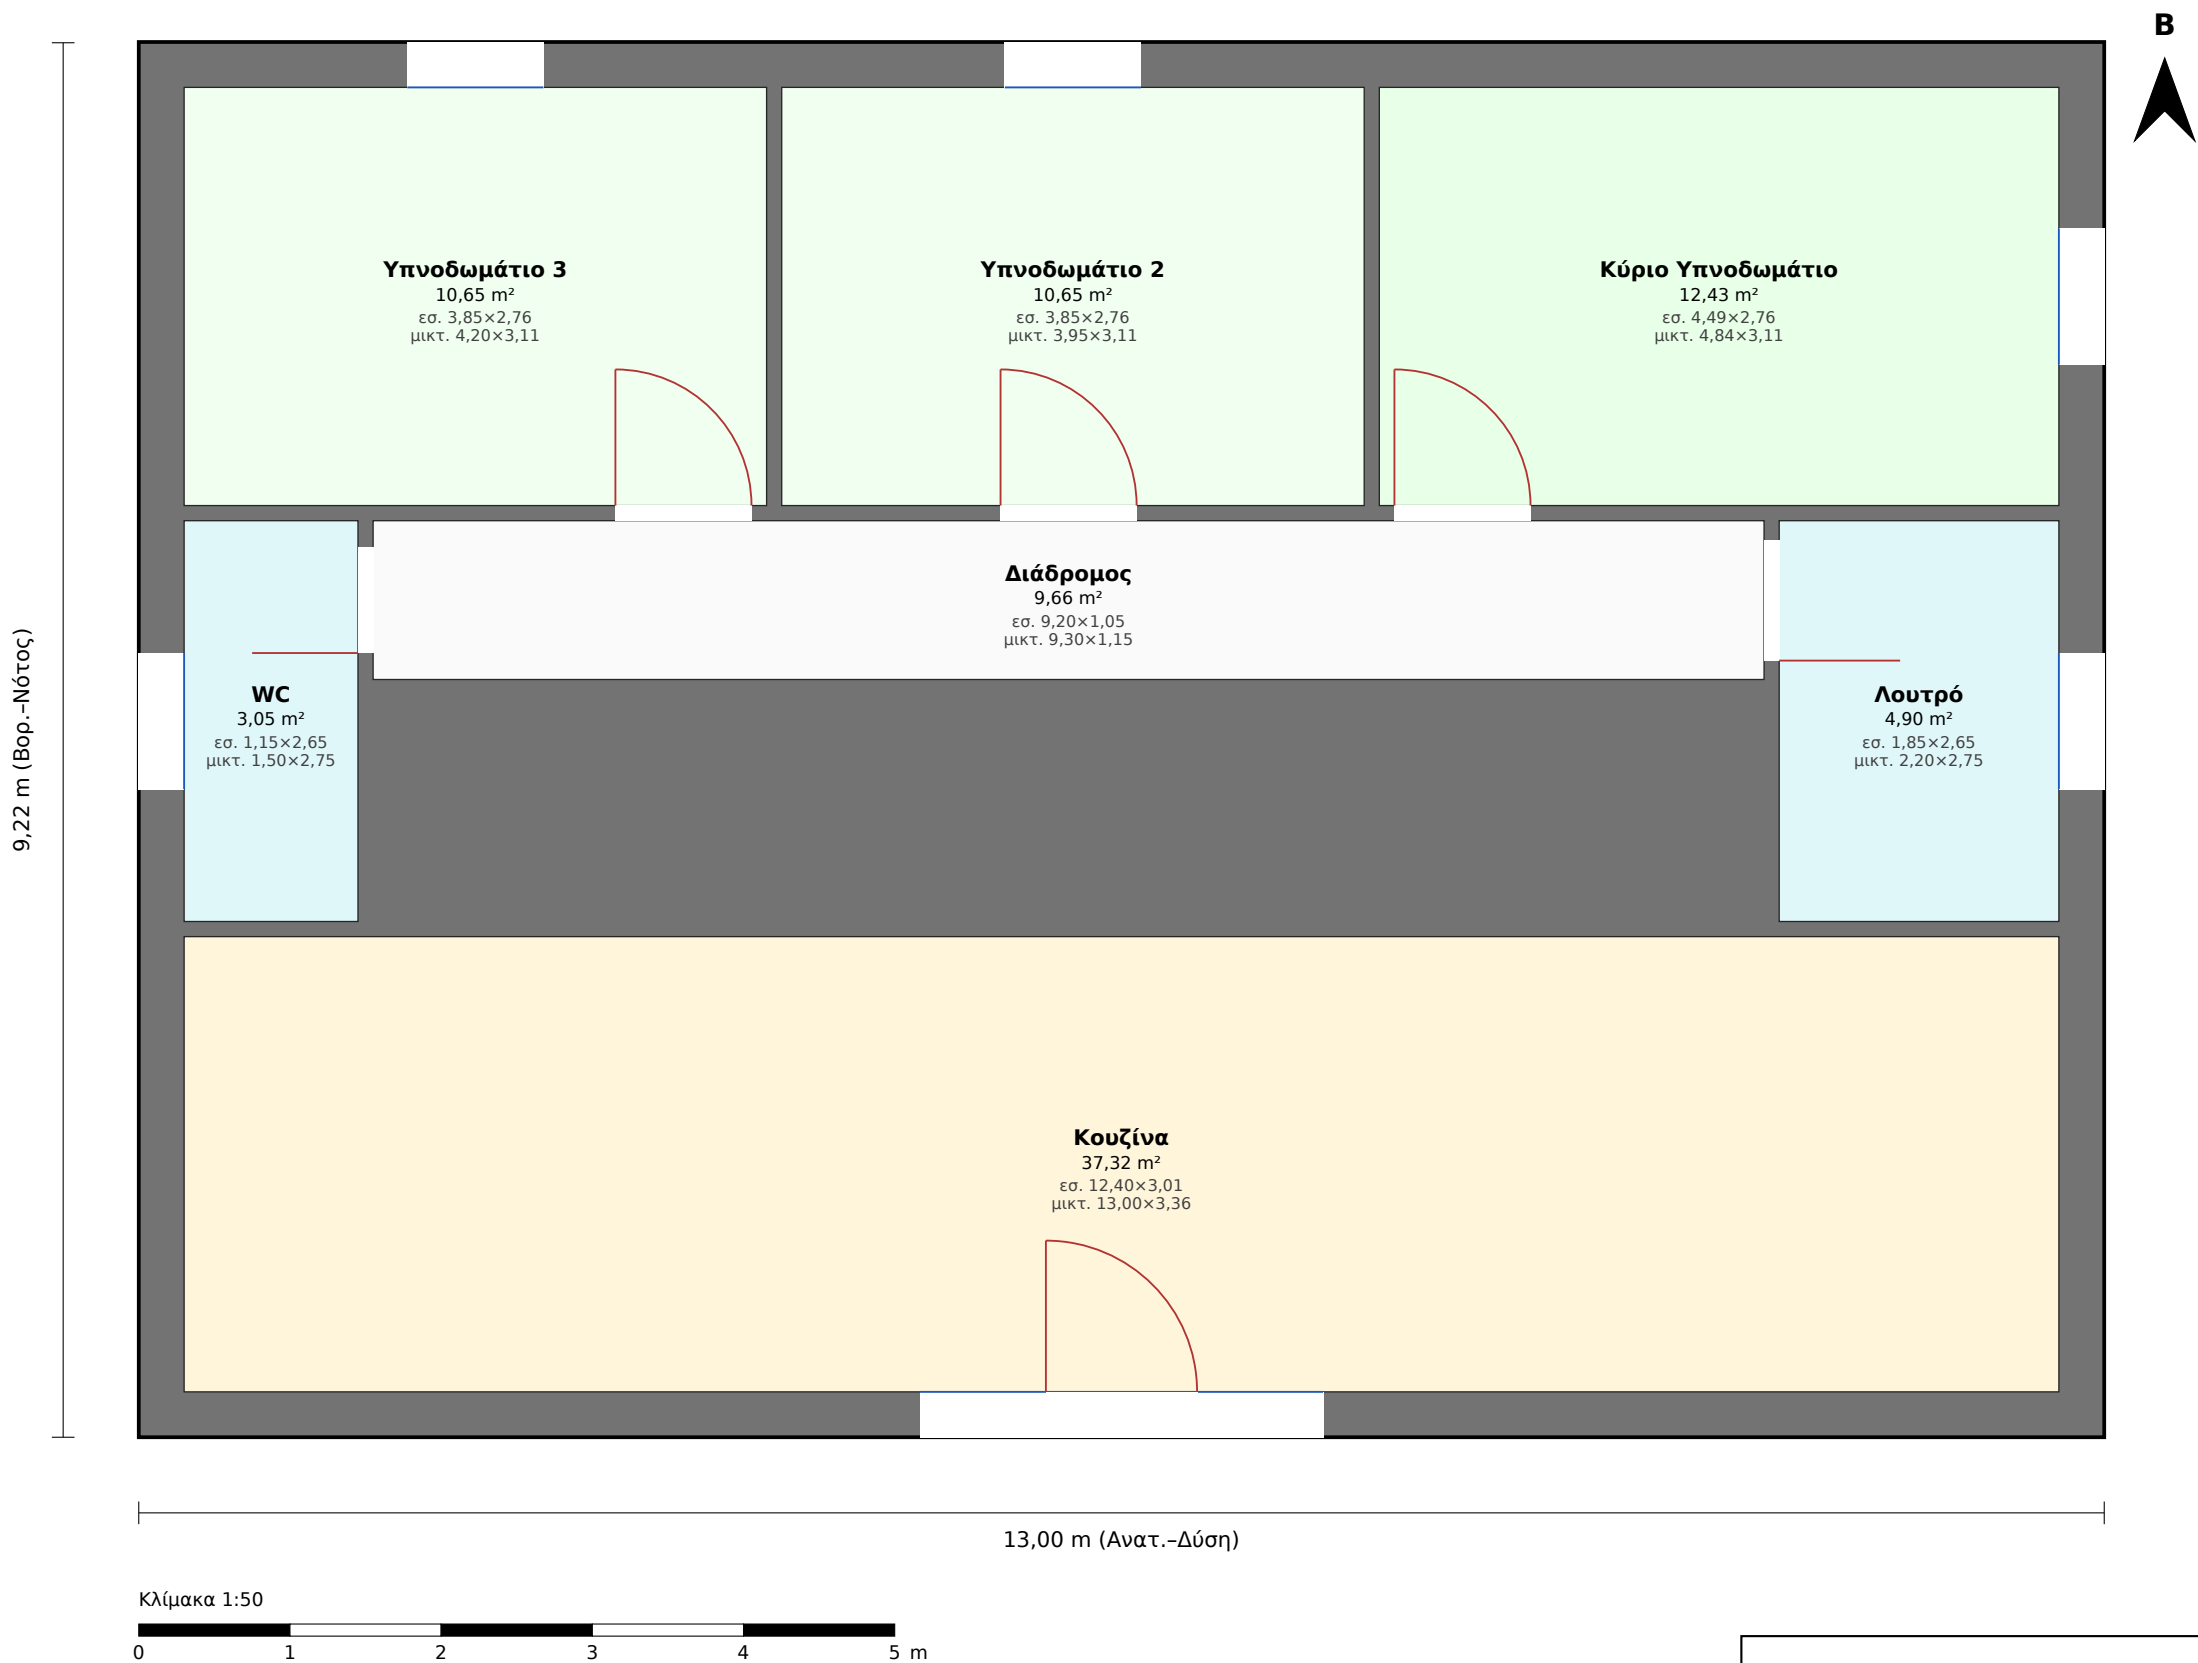

Τεχνικό Γραφείο Μελετών — Γεωργακόπουλος Χρ. / Φουντάς Αθ.
Έργο: Κατοικία
Πρόταση 2 — Ισόγειο
Κλίμακα 1:50 · Μικτό εμβ.: 119,92 m²
Είσοδος: Νότος · Αμαλιάδα, Π.Ε. Ηλείας
Ημερομηνία: 16.08.2026 · Σχεδ.: Γεωργακόπουλος Χρ. (AM TEE 101893)

Κατοικία — Πρόταση 2: Πίνακες χώρων & έλεγχοι

Διαστάσεις: «καθαρές» = εσωτερικές ελεύθερες · «μικτές» = με τοίχους (εξωτ. πλήρες πάχος, εσωτ. μισό). Βορράς: επάνω.

■ **Ισόγειο (μικτό 119,92 m², καθαρό 88,67 m²)**

#	Χώρος	Καθ. εμβ. (m²)	Καθ. Α×Β (m)	Μικτές Α×Β (m)	Ζώνη
1	Κουζίνα	37,32	12,40×3,01	13,00×3,36	κύρια
2	Υπνοδωμάτιο 3	10,65	3,85×2,76	4,20×3,11	κύρια
3	Υπνοδωμάτιο 2	10,65	3,85×2,76	3,95×3,11	κύρια
4	Κύριο Υπνοδωμάτιο	12,43	4,49×2,76	4,84×3,11	κύρια
5	WC	3,05	1,15×2,65	1,50×2,75	βοηθ.
6	Λουτρό	4,90	1,85×2,65	2,20×2,75	βοηθ.
7	Διάδρομος	9,66	9,20×1,05	9,30×1,15	βοηθ.


Έλεγχος φωτισμού & αερισμού (Κ.Κ. αρ. 20 §5.1.2 / αρ. 21 §5.2)

Χώρος	Εμβ.	Φως≥10%	Υαλοπ.	Αερ.≥5%	Ανοιγ.	Φως	Αερ.
Κουζίνα	37,3	3,73	3,73	1,87	1,87	✓	✓
Υπνοδωμάτιο 3	10,7	1,07	1,26	0,53	0,63	✓	✓
Υπνοδωμάτιο 2	10,7	1,07	1,26	0,53	0,63	✓	✓
Κύριο Υπνοδωμάτιο	12,4	1,24	1,26	0,62	0,63	✓	✓
WC	3,0	0,30	1,26	0,15	0,63	✓	✓
Λουτρό	4,9	0,49	1,26	0,25	0,63	✓	✓

→ Όλοι οι χώροι κύριας χρήσης πληρούν φωτισμό ≥10% & αερισμό ≥5%.

Παρατηρήσεις / περιορισμοί:

- [Ισόγειο] Υπνοδωμάτιο 3: 3.85×2.76 m — ελάχιστη πλευρά κάτω από 3.00 m (στενό περίγραμμα).
- [Ισόγειο] Υπνοδωμάτιο 2: 3.85×2.76 m — ελάχιστη πλευρά κάτω από 3.00 m (στενό περίγραμμα).
- [Ισόγειο] Κύριο Υπνοδωμάτιο: 4.49×2.76 m — ελάχιστη πλευρά κάτω από 3.00 m (στενό περίγραμμα).

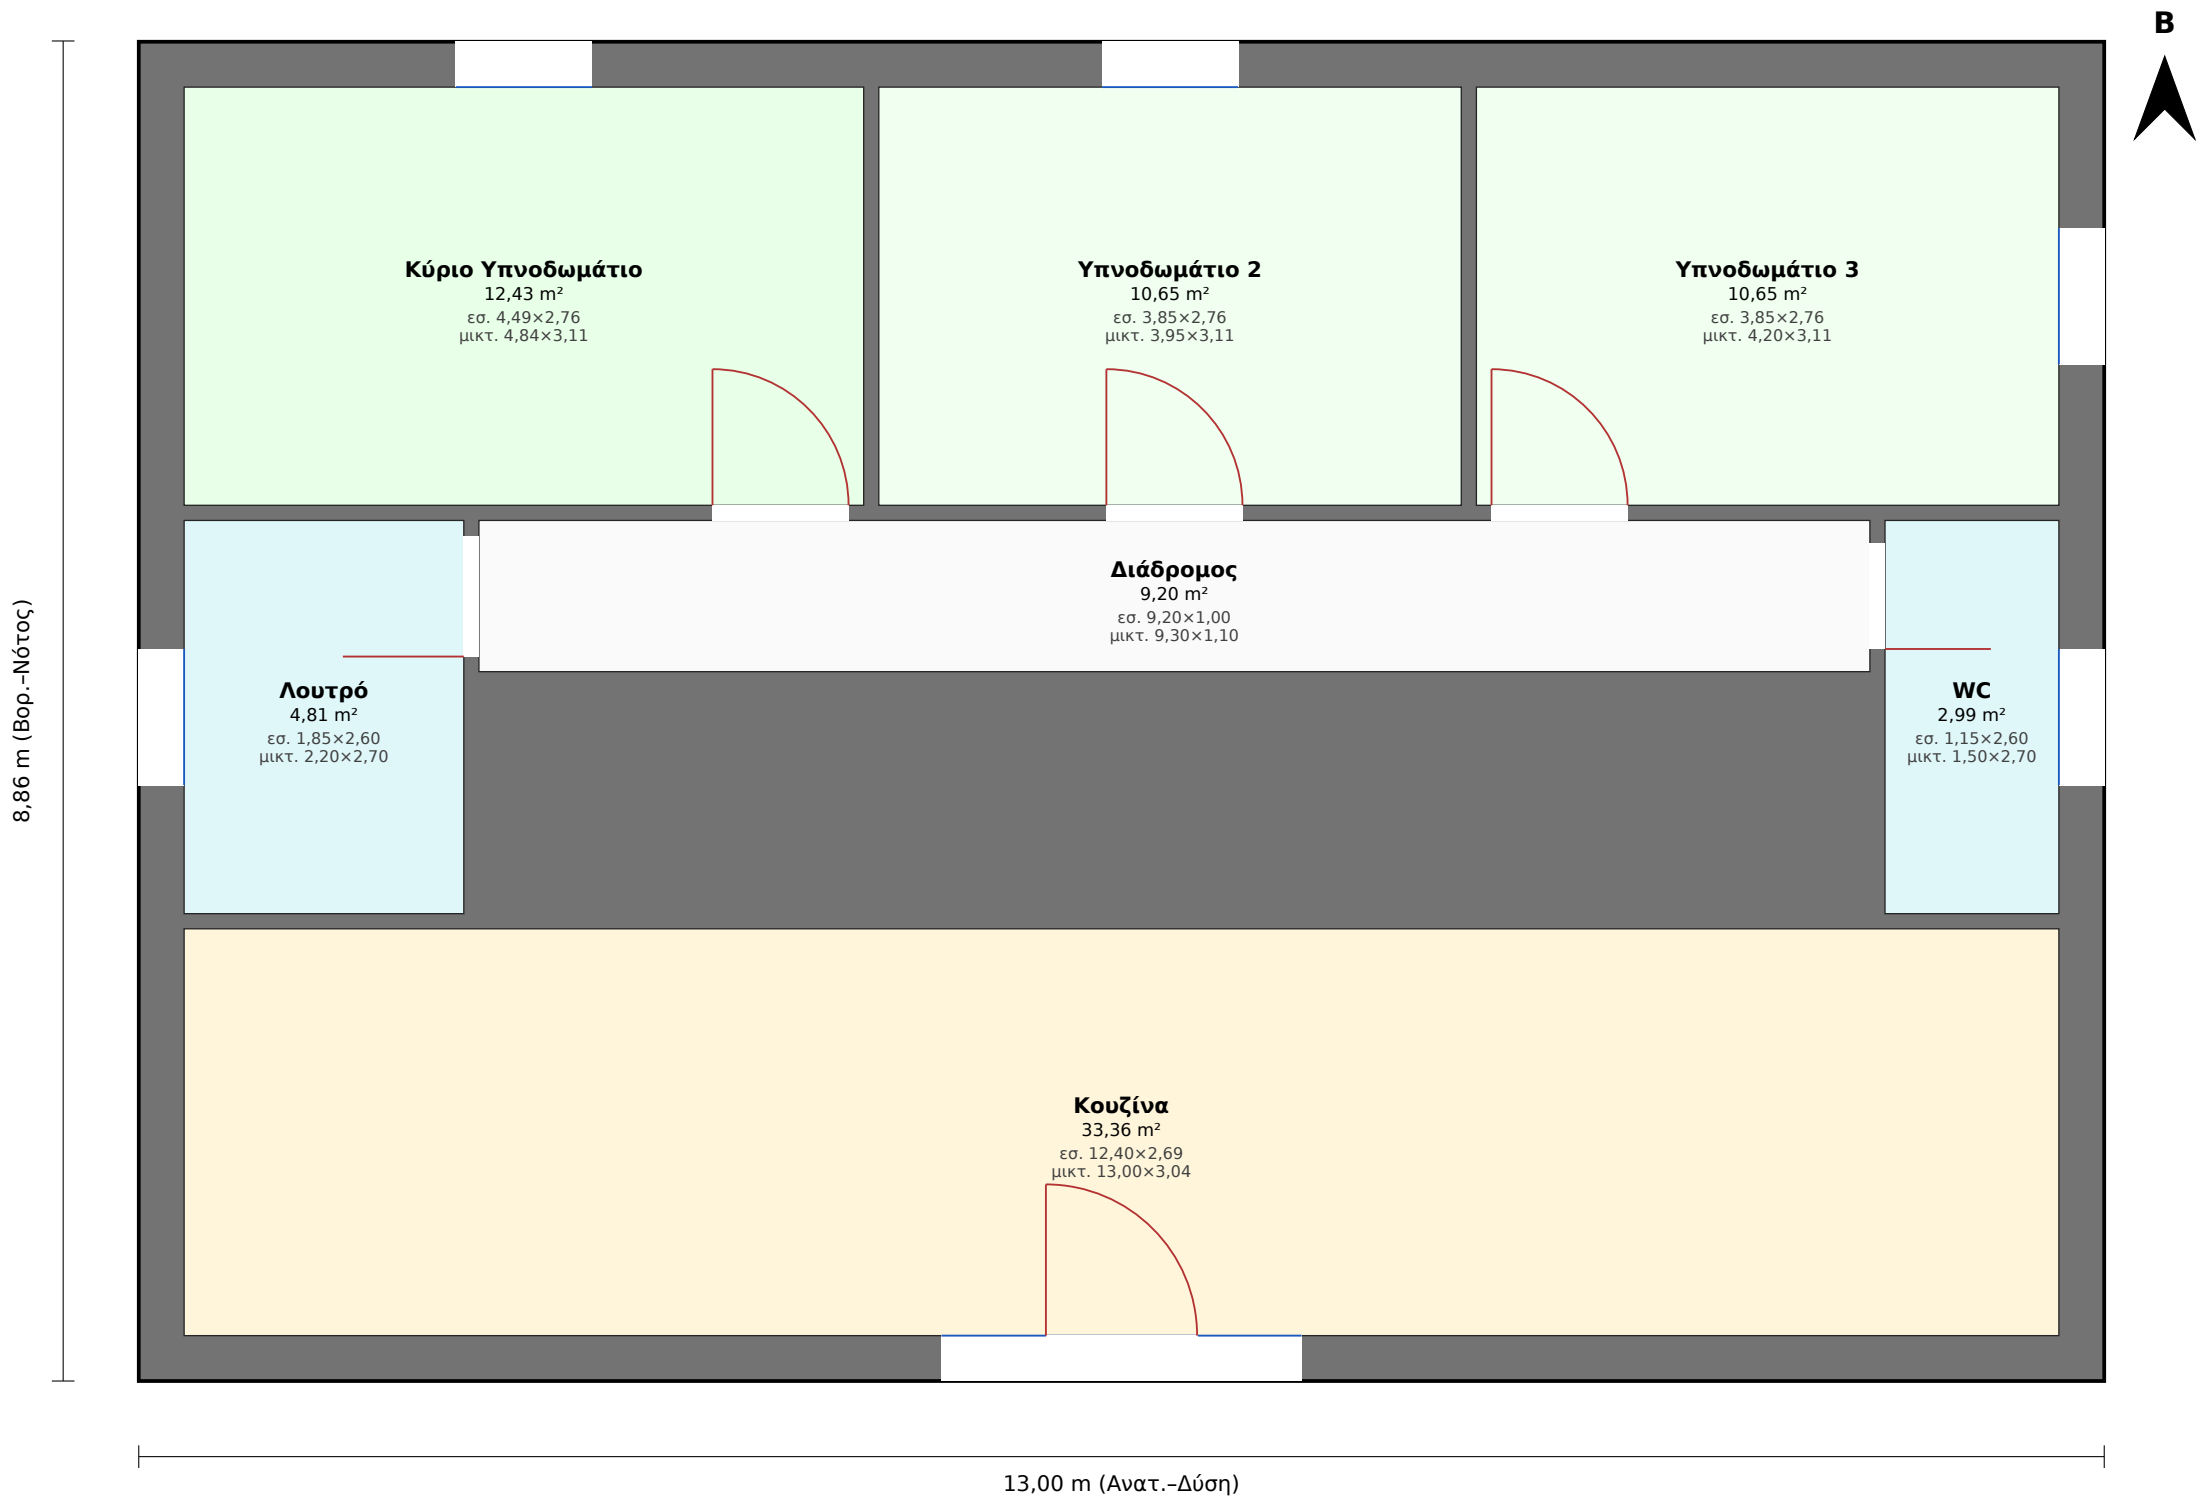

Τεχνικό Γραφείο Μελετών — Γεωργακόπουλος Χρ. / Φουντάς Αθ.
Έργο: Κατοικία
Πρόταση 3 — Ισόγειο
Κλίμακα 1:50 · Μικτό εμβ.: 115,12 m²
Είσοδος: Νότος · Αμαλιάδα, Π.Ε. Ηλείας
Ημερομηνία: 16.08.2026 · Σχεδ.: Γεωργακόπουλος Χρ. (AM TEE 101893)

Κατοικία — Πρόταση 3: Πίνακες χώρων & έλεγχοι

Διαστάσεις: «καθαρές» = εσωτερικές ελεύθερες · «μικτές» = με τοίχους (εξωτ. πλήρες πάχος, εσωτ. μισό). Βορράς: επάνω.

■ **Ισόγειο (μικτό 115,12 m², καθαρό 84,09 m²)**

#	Χώρος	Καθ. εμβ. (m²)	Καθ. Α×Β (m)	Μικτές Α×Β (m)	Ζώνη
1	Κουζίνα	33,36	12,40×2,69	13,00×3,04	κύρια
2	Κύριο Υπνοδωμάτιο	12,43	4,49×2,76	4,84×3,11	κύρια
3	Υπνοδωμάτιο 2	10,65	3,85×2,76	3,95×3,11	κύρια
4	Υπνοδωμάτιο 3	10,65	3,85×2,76	4,20×3,11	κύρια
5	Λουτρό	4,81	1,85×2,60	2,20×2,70	βοηθ.
6	WC	2,99	1,15×2,60	1,50×2,70	βοηθ.
7	Διάδρομος	9,20	9,20×1,00	9,30×1,10	βοηθ.

Έλεγχος φωτισμού & αερισμού (Κ.Κ. αρ. 20 §5.1.2 / αρ. 21 §5.2)

Χώρος	Εμβ.	Φως≥10%	Υαλοπ.	Αερ.≥5%	Ανοιγ.	Φως	Αερ.
Κουζίνα	33,4	3,34	3,34	1,67	1,67	✓	✓
Κύριο Υπνοδωμάτιο	12,4	1,24	1,26	0,62	0,63	✓	✓
Υπνοδωμάτιο 2	10,7	1,07	1,26	0,53	0,63	✓	✓
Υπνοδωμάτιο 3	10,7	1,07	1,26	0,53	0,63	✓	✓
Λουτρό	4,8	0,48	1,26	0,24	0,63	✓	✓
WC	3,0	0,30	1,26	0,15	0,63	✓	✓

→ Όλοι οι χώροι κύριας χρήσης πληρούν φωτισμό ≥10% & αερισμό ≥5%.

Παρατηρήσεις / περιορισμοί:

- [Ισόγειο] Κύριο Υπνοδωμάτιο: 4.49×2.76 m — ελάχιστη πλευρά κάτω από 3.00 m (στενό περίγραμμα).
- [Ισόγειο] Υπνοδωμάτιο 2: 3.85×2.76 m — ελάχιστη πλευρά κάτω από 3.00 m (στενό περίγραμμα).
- [Ισόγειο] Υπνοδωμάτιο 3: 3.85×2.76 m — ελάχιστη πλευρά κάτω από 3.00 m (στενό περίγραμμα).