


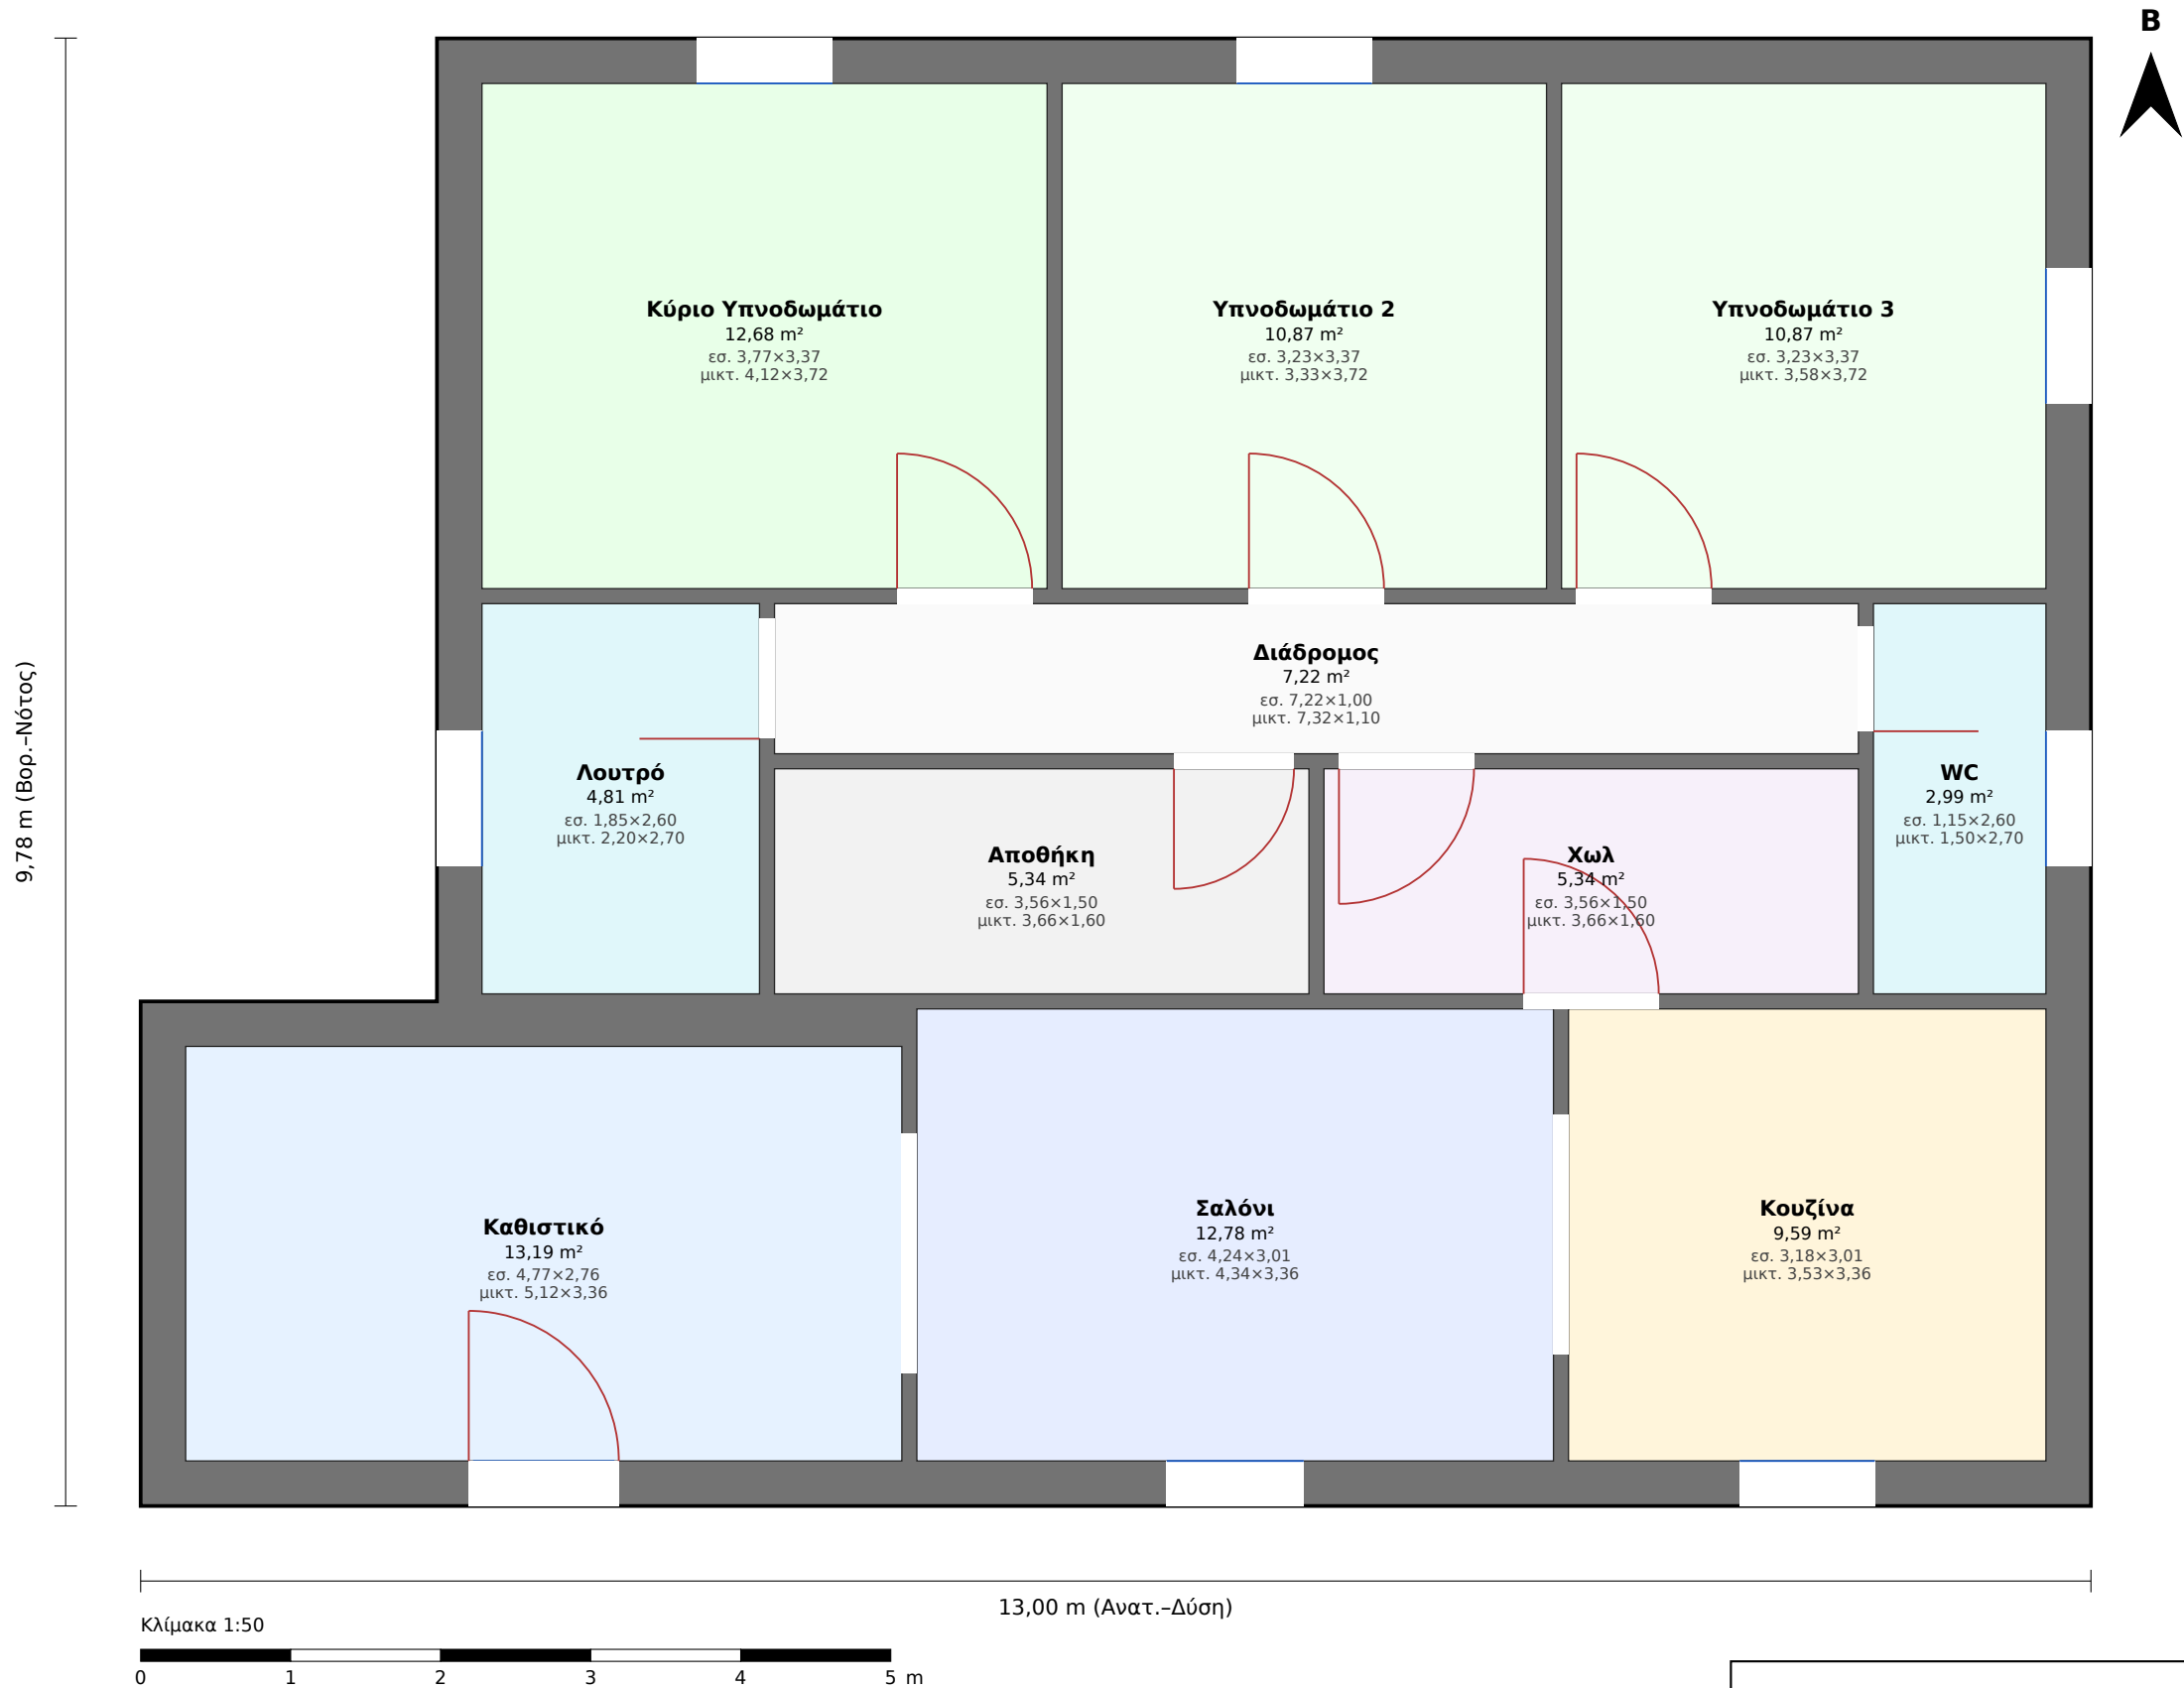

Τεχνικό Γραφείο Μελετών — Γεωργακόπουλος Χρ. / Φουντάς Αθ.
Έργο: Μονοκατοικία Αμαλιάδας
Πρόταση 3 — Ισόγειο
Κλίμακα 1:50 · Μικτό εμβ.: 114,44 m²
Είσοδος: Νότος · Αμαλιάδα, Π.Ε. Ηλείας
Ημερομηνία: 16.08.2026 · Σχεδ.: Γεωργακόπουλος Χρ. (ΑΜ ΤΕΕ 101893)

Μονοκατοικία Αμαλιάδας — Πρόταση 3: Πίνακες χώρων & έλεγχοι

Διαστάσεις: «καθαρές» = εσωτερικές ελεύθερες · «μικτές» = με τοίχους (εξωτ. πλήρες πάχος, εσωτ. μισό). Βορράς: επάνω.

■ Ισόγειο (μικτό 114,44 m², καθαρό 95,68 m²)

#	Χώρος	Καθ. εμβ. (m²)	Καθ. Α×Β (m)	Μικτές Α×Β (m)	Ζώνη
1	Καθιστικό	13,19	4,77×2,76	5,12×3,36	κύρια
2	Σαλόνι	12,78	4,24×3,01	4,34×3,36	κύρια
3	Κουζίνα	9,59	3,18×3,01	3,53×3,36	κύρια
4	Κύριο Υπνοδωμάτιο	12,68	3,77×3,37	4,12×3,72	κύρια
5	Υπνοδωμάτιο 2	10,87	3,23×3,37	3,33×3,72	κύρια
6	Υπνοδωμάτιο 3	10,87	3,23×3,37	3,58×3,72	κύρια
7	Λουτρό	4,81	1,85×2,60	2,20×2,70	βοηθ.
8	Αποθήκη	5,34	3,56×1,50	3,66×1,60	βοηθ.
9	Χωλ	5,34	3,56×1,50	3,66×1,60	βοηθ.
10	WC	2,99	1,15×2,60	1,50×2,70	βοηθ.
11	Διάδρομος	7,22	7,22×1,00	7,32×1,10	βοηθ.

Έλεγχος φωτισμού & αερισμού (Κ.Κ. αρ. 20 §5.1.2 / αρ. 21 §5.2)

Χώρος	Εμβ.	Φως≥10%	Υαλοπ.	Αερ.≥5%	Ανοιγ.	Φως	Αερ.
Καθιστικό	13,2	1,32	1,32	0,66	0,66	✓	✓
Σαλόνι	12,8	1,28	1,28	0,64	0,64	✓	✓
Κουζίνα	9,6	0,96	1,26	0,48	0,63	✓	✓
Κύριο Υπνοδωμάτιο	12,7	1,27	1,27	0,63	0,63	✓	✓
Υπνοδωμάτιο 2	10,9	1,09	1,26	0,54	0,63	✓	✓
Υπνοδωμάτιο 3	10,9	1,09	1,26	0,54	0,63	✓	✓
Λουτρό	4,8	0,48	1,26	0,24	0,63	✓	✓
Αποθήκη	5,3	0,53	0,00	0,27	0,00	✓	✓
Χωλ	5,3	0,53	0,00	0,27	0,00	✓	✓
WC	3,0	0,30	1,26	0,15	0,63	✓	✓

→ Όλοι οι χώροι κύριας χρήσης πληρούν φωτισμό ≥10% & αερισμό ≥5%.