


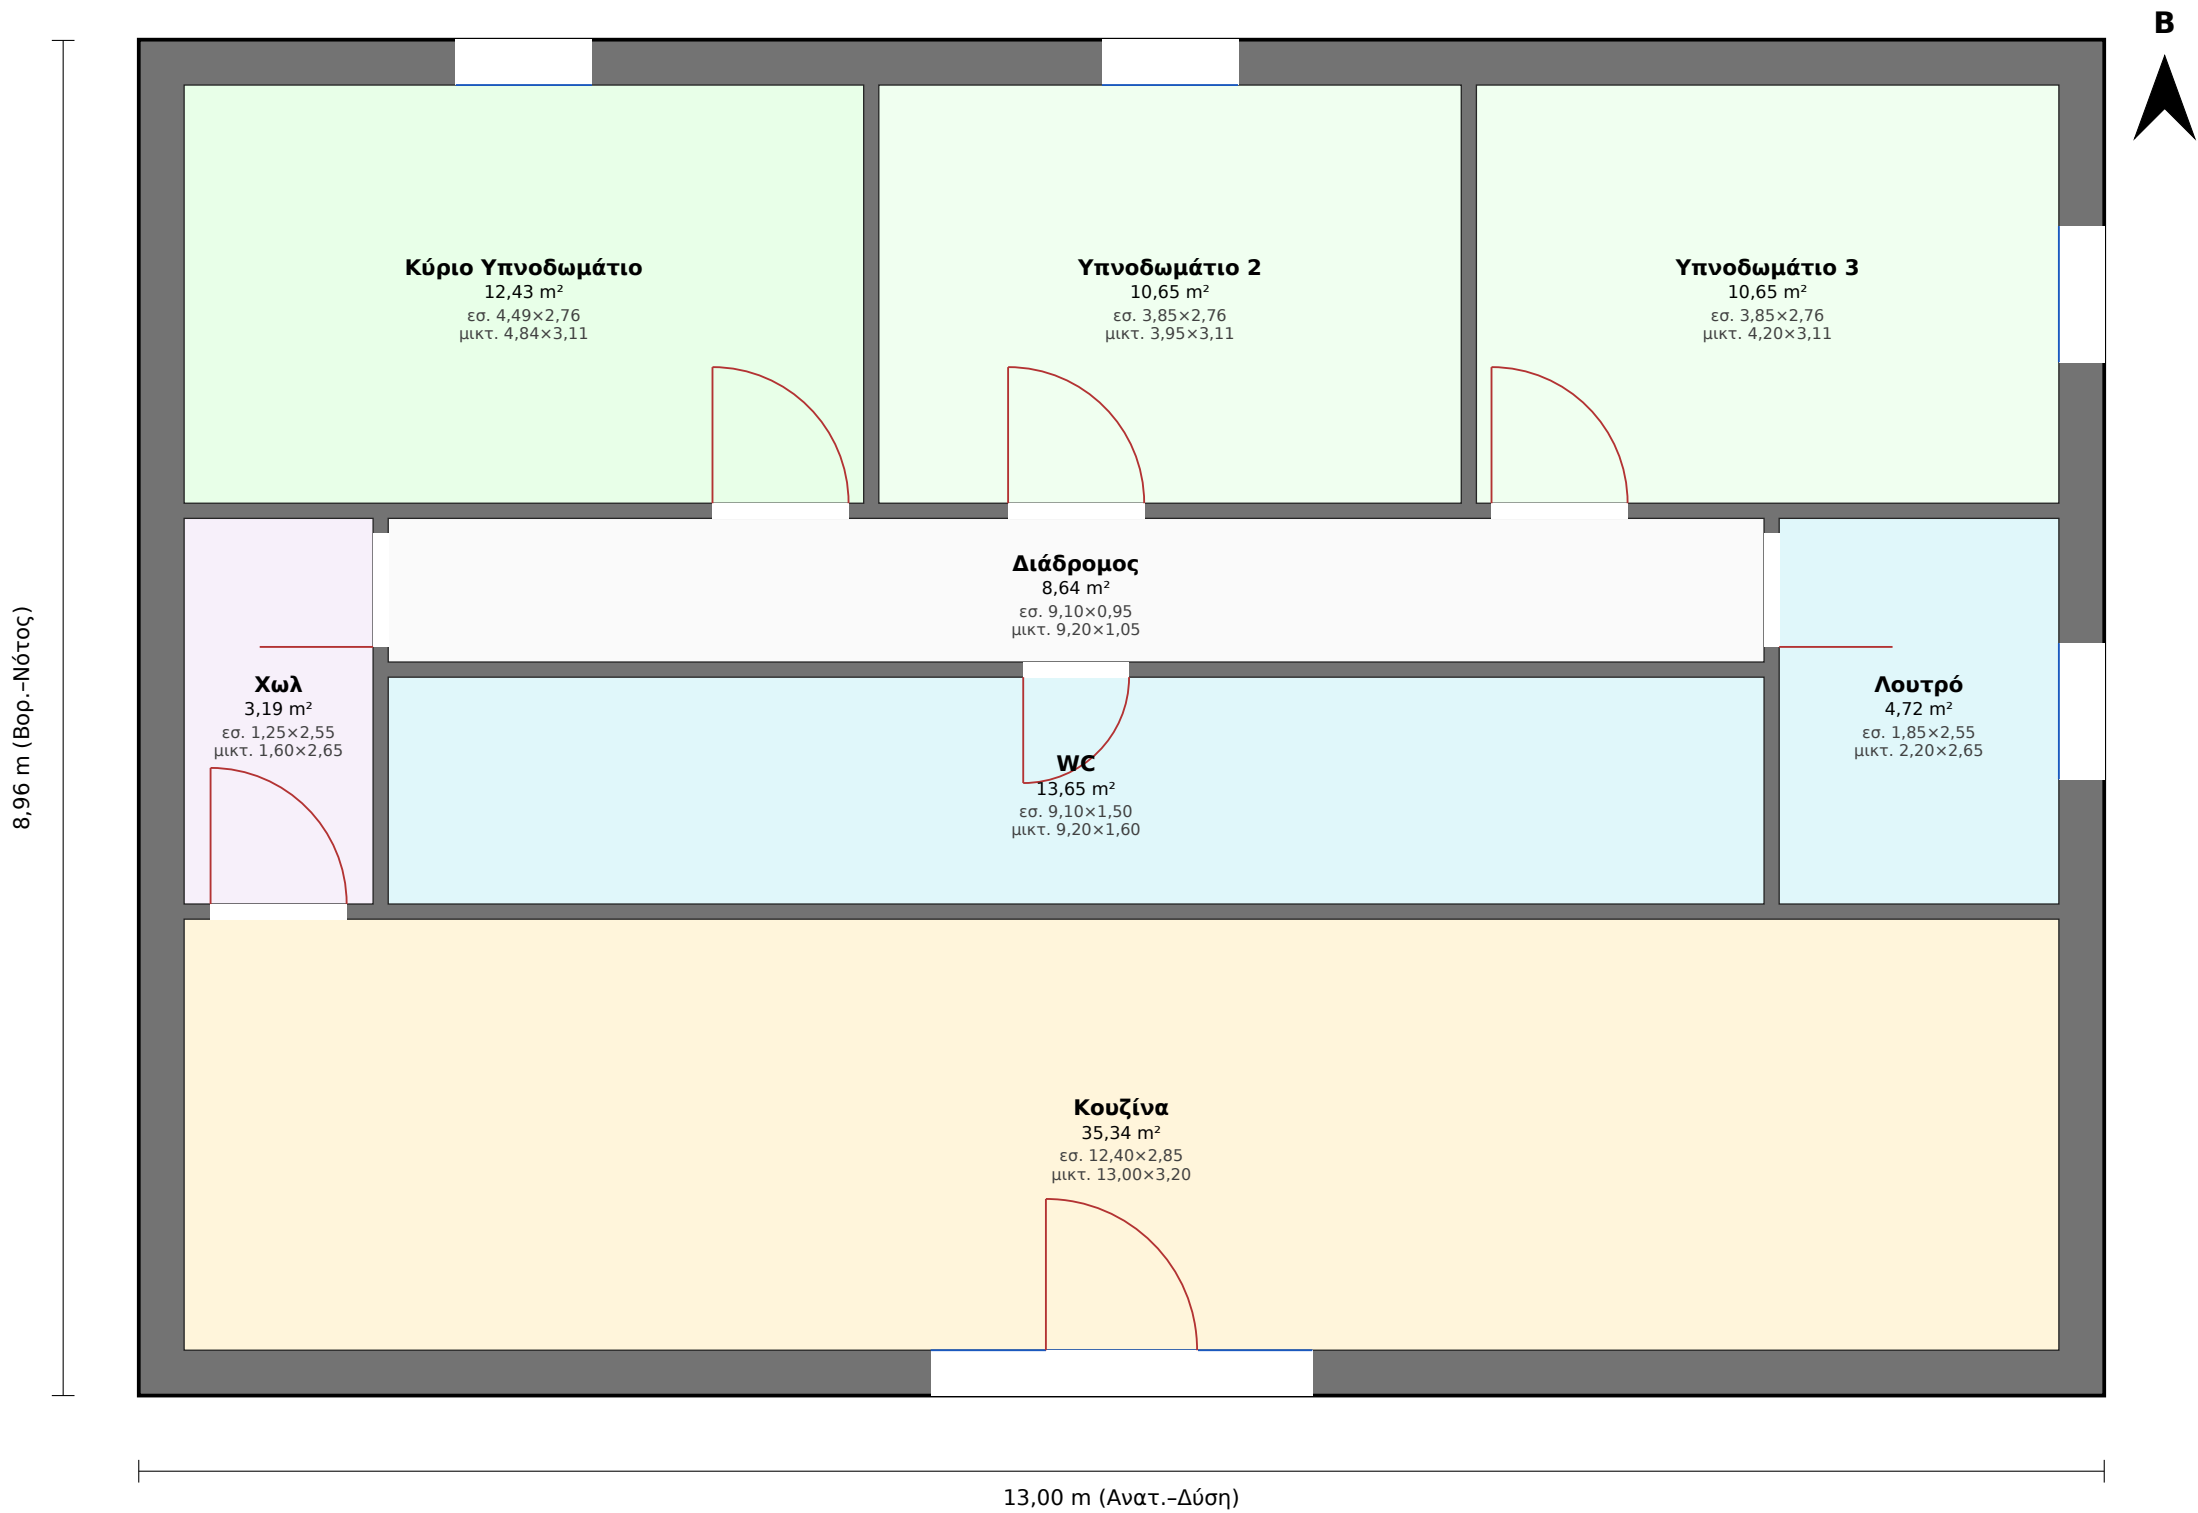

Τεχνικό Γραφείο Μελετών — Γεωργακόπουλος Χρ. / Φουντάς Αθ.
Έργο: Κατοικία
Πρόταση 1 — Ισόγειο
Κλίμακα 1:50 · Μικτό εμβ.: 116,55 m²
Είσοδος: Νότος · Αμαλιάδα, Π.Ε. Ηλείας
Ημερομηνία: 16.08.2026 · Σχεδ.: Γεωργακόπουλος Χρ. (AM TEE 101893)

Κατοικία — Πρόταση 1: Πίνακες χώρων & έλεγχοι

Διαστάσεις: «καθαρές» = εσωτερικές ελεύθερες · «μικτές» = με τοίχους (εξωτ. πλήρες πάχος, εσωτ. μισό). Βορράς: επάνω.

■ Ισόγειο (μικτό 116,55 m², καθαρό 99,27 m²)

#	Χώρος	Καθ. εμβ. (m²)	Καθ. Α×Β (m)	Μικτές Α×Β (m)	Ζώνη
1	Κουζίνα	35,34	12,40×2,85	13,00×3,20	κύρια
2	Κύριο Υπνοδωμάτιο	12,43	4,49×2,76	4,84×3,11	κύρια
3	Υπνοδωμάτιο 2	10,65	3,85×2,76	3,95×3,11	κύρια
4	Υπνοδωμάτιο 3	10,65	3,85×2,76	4,20×3,11	κύρια
5	Χωλ	3,19	1,25×2,55	1,60×2,65	βοηθ.
6	WC	13,65	9,10×1,50	9,20×1,60	βοηθ.
7	Λουτρό	4,72	1,85×2,55	2,20×2,65	βοηθ.
8	Διάδρομος	8,64	9,10×0,95	9,20×1,05	βοηθ.

Έλεγχος φωτισμού & αερισμού (Κ.Κ. αρ. 20 §5.1.2 / αρ. 21 §5.2)

Χώρος	Εμβ.	Φως≥10%	Υαλοπ.	Αερ.≥5%	Ανοιγ.	Φως	Αερ.
Κουζίνα	35,3	3,53	3,53	1,77	1,77	✓	✓
Κύριο Υπνοδωμάτιο	12,4	1,24	1,26	0,62	0,63	✓	✓
Υπνοδωμάτιο 2	10,7	1,07	1,26	0,53	0,63	✓	✓
Υπνοδωμάτιο 3	10,7	1,07	1,26	0,53	0,63	✓	✓
Χωλ	3,2	0,32	0,00	0,16	0,00	✓	✓
WC	13,7	1,37	0,00	0,68	0,00	✓	✓
Λουτρό	4,7	0,47	1,26	0,24	0,63	✓	✓

→ Όλοι οι χώροι κύριας χρήσης πληρούν φωτισμό ≥10% & αερισμό ≥5%.

Παρατηρήσεις / περιορισμοί:

- [Ισόγειο] Κύριο Υπνοδωμάτιο: 4.49×2.76 m — ελάχιστη πλευρά κάτω από 3.00 m (στενό περίγραμμα).
- [Ισόγειο] Υπνοδωμάτιο 2: 3.85×2.76 m — ελάχιστη πλευρά κάτω από 3.00 m (στενό περίγραμμα).
- [Ισόγειο] Υπνοδωμάτιο 3: 3.85×2.76 m — ελάχιστη πλευρά κάτω από 3.00 m (στενό περίγραμμα).