


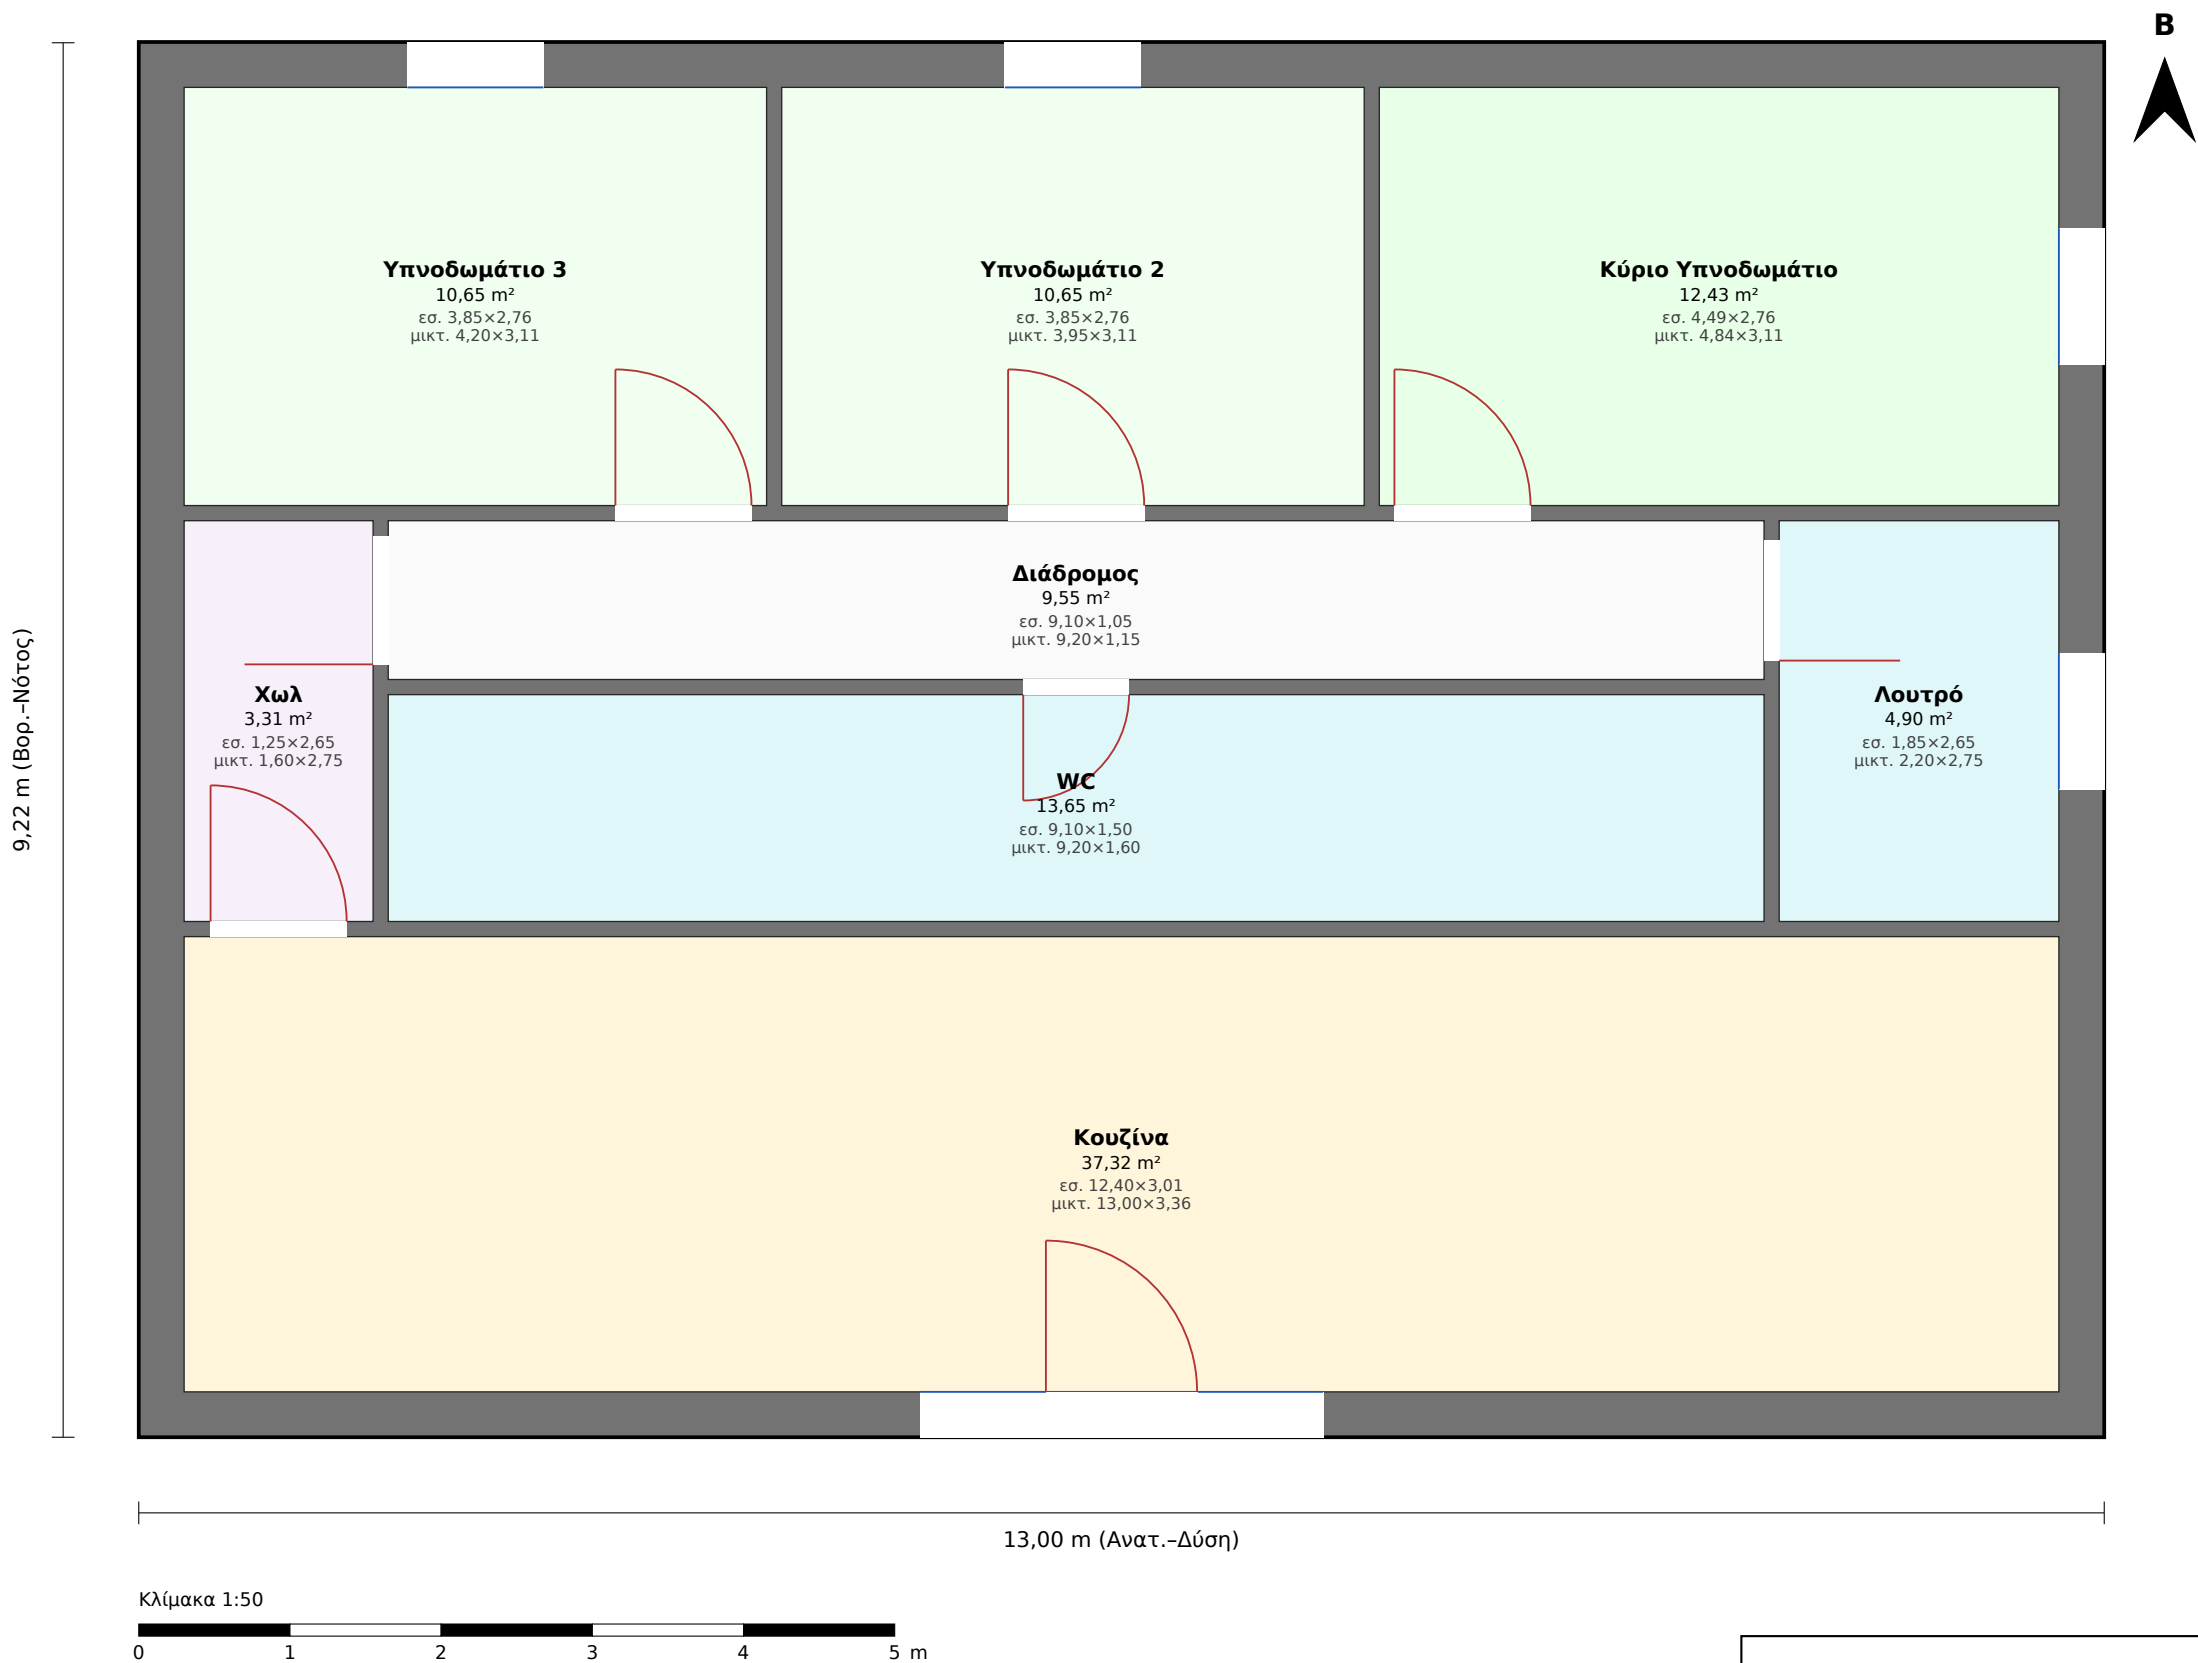

Τεχνικό Γραφείο Μελετών — Γεωργακόπουλος Χρ. / Φουντάς Αθ.
Έργο: Κατοικία
Πρόταση 2 — Ισόγειο
Κλίμακα 1:50 · Μικτό εμβ.: 119,92 m²
Είσοδος: Νότος · Αμαλιάδα, Π.Ε. Ηλείας
Ημερομηνία: 16.08.2026 · Σχεδ.: Γεωργακόπουλος Χρ. (ΑΜ ΤΕΕ 101893)

Κατοικία — Πρόταση 2: Πίνακες χώρων & έλεγχοι

Διαστάσεις: «καθαρές» = εσωτερικές ελεύθερες · «μικτές» = με τοίχους (εξωτ. πλήρες πάχος, εσωτ. μισό). Βορράς: επάνω.

■ Ισόγειο (μικτό 119,92 m², καθαρό 102,48 m²)

#	Χώρος	Καθ. εμβ. (m²)	Καθ. Α×Β (m)	Μικτές Α×Β (m)	Ζώνη
1	Κουζίνα	37,32	12,40×3,01	13,00×3,36	κύρια
2	Υπνοδωμάτιο 3	10,65	3,85×2,76	4,20×3,11	κύρια
3	Υπνοδωμάτιο 2	10,65	3,85×2,76	3,95×3,11	κύρια
4	Κύριο Υπνοδωμάτιο	12,43	4,49×2,76	4,84×3,11	κύρια
5	Χωλ	3,31	1,25×2,65	1,60×2,75	βοηθ.
6	WC	13,65	9,10×1,50	9,20×1,60	βοηθ.
7	Λουτρό	4,90	1,85×2,65	2,20×2,75	βοηθ.
8	Διάδρομος	9,55	9,10×1,05	9,20×1,15	βοηθ.

Έλεγχος φωτισμού & αερισμού (Κ.Κ. αρ. 20 §5.1.2 / αρ. 21 §5.2)

Χώρος	Εμβ.	Φως≥10%	Υαλοπ.	Αερ.≥5%	Ανοιγ.	Φως	Αερ.
Κουζίνα	37,3	3,73	3,73	1,87	1,87	✓	✓
Υπνοδωμάτιο 3	10,7	1,07	1,26	0,53	0,63	✓	✓
Υπνοδωμάτιο 2	10,7	1,07	1,26	0,53	0,63	✓	✓
Κύριο Υπνοδωμάτιο	12,4	1,24	1,26	0,62	0,63	✓	✓
Χωλ	3,3	0,33	0,00	0,17	0,00	✓	✓
WC	13,7	1,37	0,00	0,68	0,00	✓	✓
Λουτρό	4,9	0,49	1,26	0,25	0,63	✓	✓

→ Όλοι οι χώροι κύριας χρήσης πληρούν φωτισμό ≥10% & αερισμό ≥5%.

Παρατηρήσεις / περιορισμοί:

- [Ισόγειο] Υπνοδωμάτιο 3: 3.85×2.76 m — ελάχιστη πλευρά κάτω από 3.00 m (στενό περίγραμμα).
- [Ισόγειο] Υπνοδωμάτιο 2: 3.85×2.76 m — ελάχιστη πλευρά κάτω από 3.00 m (στενό περίγραμμα).
- [Ισόγειο] Κύριο Υπνοδωμάτιο: 4.49×2.76 m — ελάχιστη πλευρά κάτω από 3.00 m (στενό περίγραμμα).