


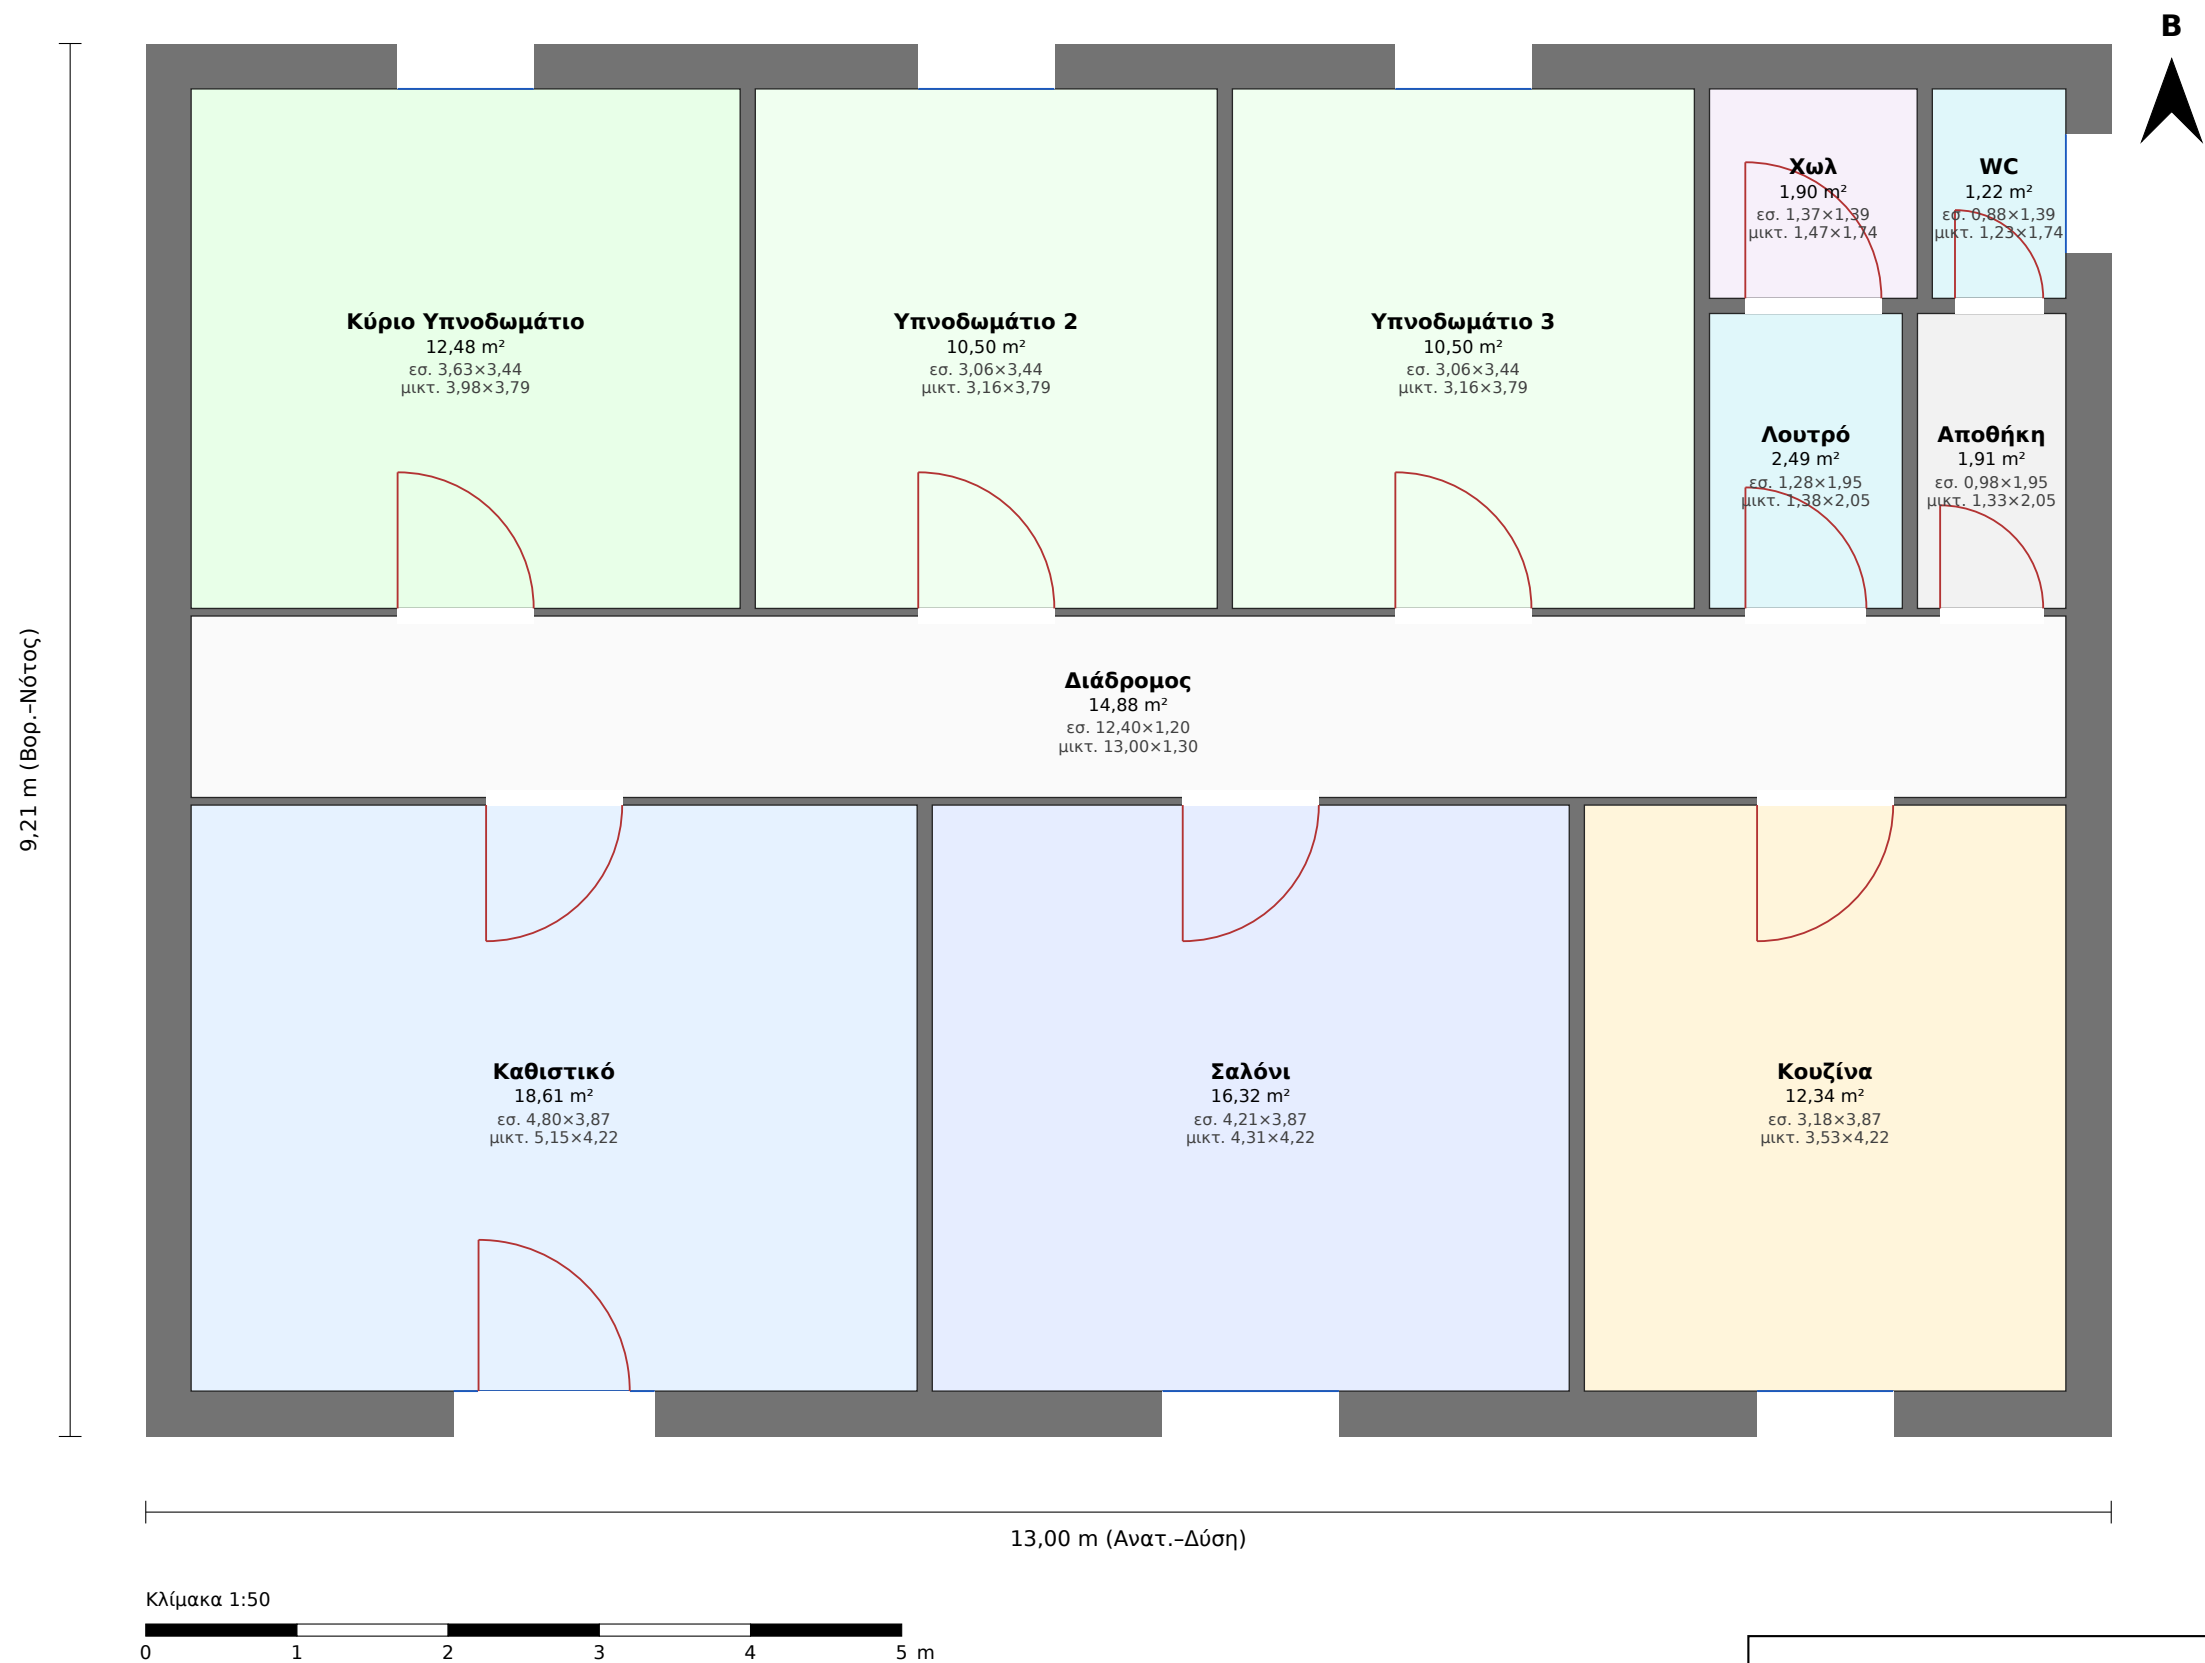

Τεχνικό Γραφείο Μελετών — Γεωργακόπουλος Χρ. / Φουντάς Αθ.
Έργο: Μονοκατοικία Αμαλιάδας
Πρόταση 1 — Ισόγειο
Κλίμακα 1:50 · Μικτό εμβ.: 119,73 m²
Είσοδος: Νότος · Αμαλιάδα, Π.Ε. Ηλείας
Ημερομηνία: 15.08.2026 · Σχεδ.: Γεωργακόπουλος Χρ. (AM TEE 101893)

Μονοκατοικία Αμαλιάδας — Πρόταση 1: Πίνακες χώρων & έλεγχοι

Διαστάσεις: «καθαρές» = εσωτερικές ελεύθερες · «μικτές» = με τοίχους (εξωτ. πλήρες πάχος, εσωτ. μισό). Βορράς: επάνω.


■ **Ισόγειο (μικτό 119,73 m², καθαρό 103,15 m²)**

#	Χώρος	Καθ. εμβ. (m²)	Καθ. Α×Β (m)	Μικτές Α×Β (m)	Ζώνη
1	Καθιστικό	18,61	4,80×3,87	5,15×4,22	κύρια
2	Σαλόνι	16,32	4,21×3,87	4,31×4,22	κύρια
3	Κουζίνα	12,34	3,18×3,87	3,53×4,22	κύρια
4	Κύριο Υπνοδωμάτιο	12,48	3,63×3,44	3,98×3,79	κύρια
5	Υπνοδωμάτιο 2	10,50	3,06×3,44	3,16×3,79	κύρια
6	Υπνοδωμάτιο 3	10,50	3,06×3,44	3,16×3,79	κύρια
7	Λουτρό	2,49	1,28×1,95	1,38×2,05	βοηθ.
8	Αποθήκη	1,91	0,98×1,95	1,33×2,05	βοηθ.
9	Χωλ	1,90	1,37×1,39	1,47×1,74	βοηθ.
10	WC	1,22	0,88×1,39	1,23×1,74	βοηθ.
11	Διάδρομος	14,88	12,40×1,20	13,00×1,30	βοηθ.

Έλεγχος φωτισμού & αερισμού (Κ.Κ. αρ. 20 §5.1.2 / αρ. 21 §5.2)

Χώρος	Εμβ.	Φως≥10%	Υαλοπ.	Αερ.≥5%	Ανοιγ.	Φως	Αερ.
Καθιστικό	18,6	1,86	1,86	0,93	0,93	✓	✓
Σαλόνι	16,3	1,63	1,63	0,82	0,82	✓	✓
Κουζίνα	12,3	1,23	1,26	0,62	0,63	✓	✓
Κύριο Υπνοδωμάτιο	12,5	1,25	1,26	0,62	0,63	✓	✓
Υπνοδωμάτιο 2	10,5	1,05	1,26	0,52	0,63	✓	✓
Υπνοδωμάτιο 3	10,5	1,05	1,26	0,52	0,63	✓	✓
Λουτρό	2,5	0,25	0,00	0,12	0,00	✓	✓
Αποθήκη	1,9	0,19	0,00	0,10	0,00	✓	✓
Χωλ	1,9	0,19	0,00	0,10	0,00	✓	✓
WC	1,2	0,12	1,10	0,06	0,55	✓	✓

→ Όλοι οι χώροι κύριας χρήσης πληρούν φωτισμό ≥10% & αερισμό ≥5%.

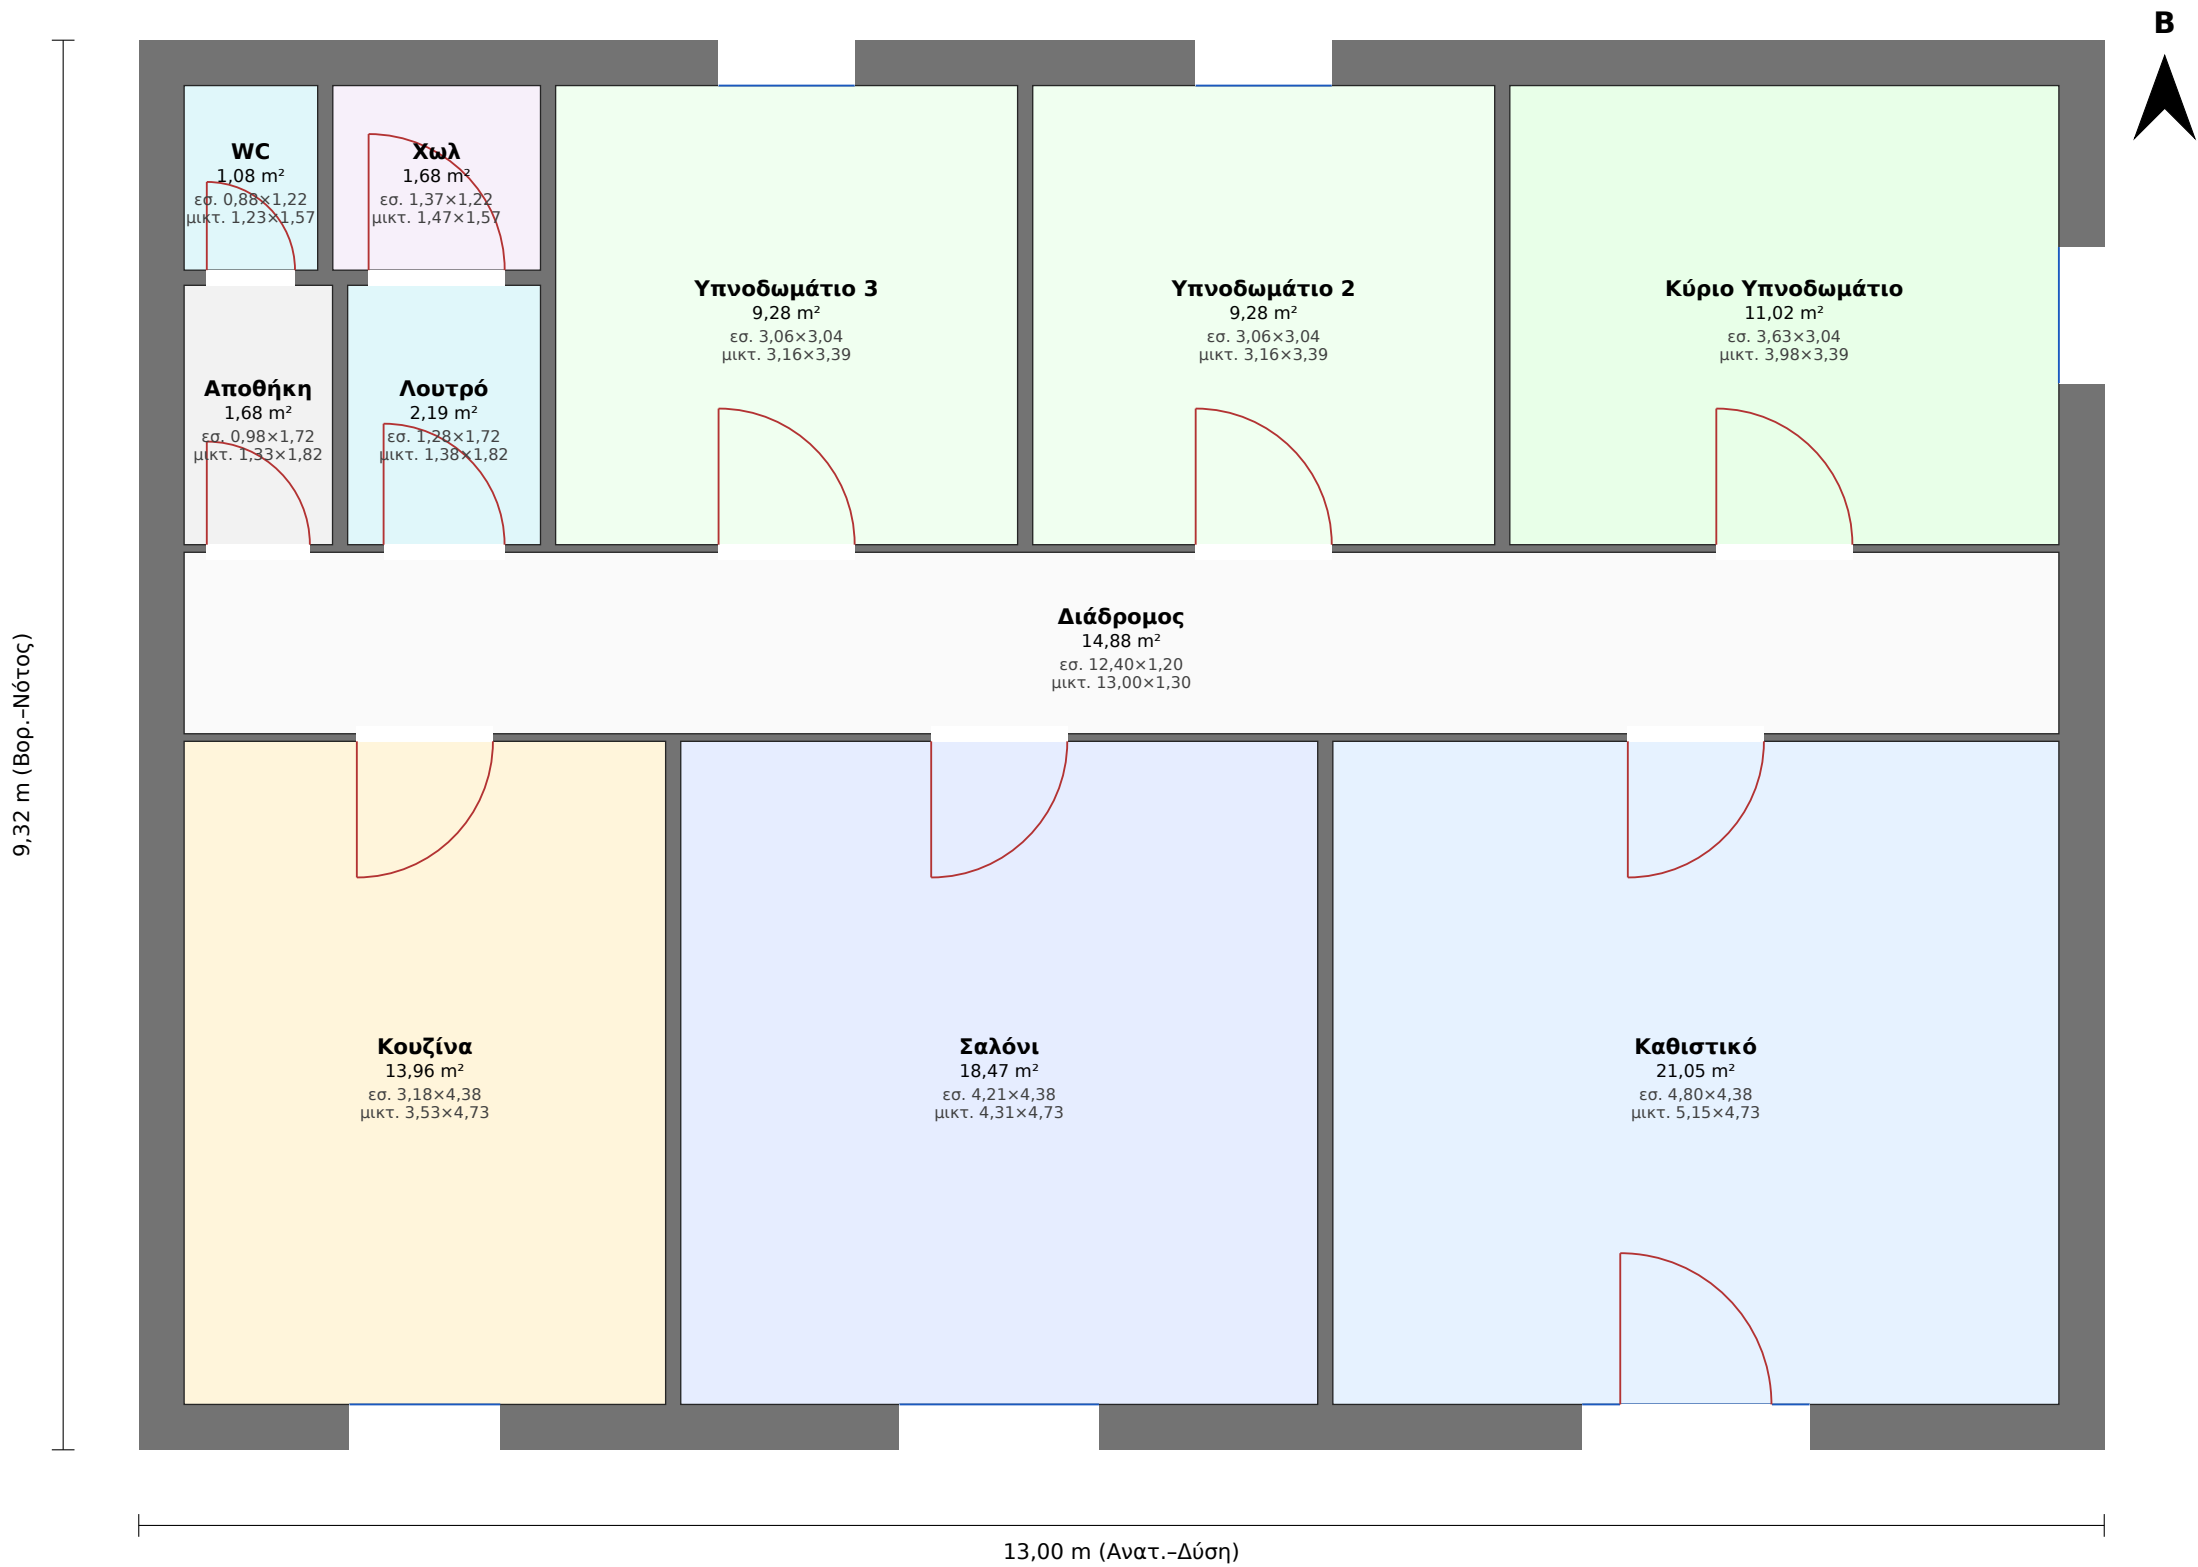

Κλίμακα 1:50



Τεχνικό Γραφείο Μελετών — Γεωργακόπουλος Χρ. / Φουντάς Αθ.
Έργο: Μονοκατοικία Αμαλιάδας
Πρόταση 2 — Ισόγειο
Κλίμακα 1:50 · Μικτό εμβ.: 121,16 m²
Είσοδος: Νότος · Αμαλιάδα, Π.Ε. Ηλείας
Ημερομηνία: 15.08.2026 · Σχεδ.: Γεωργακόπουλος Χρ. (ΑΜ ΤΕΕ 101893)

Μονοκατοικία Αμαλιάδας — Πρόταση 2: Πίνακες χώρων & έλεγχοι

Διαστάσεις: «καθαρές» = εσωτερικές ελεύθερες · «μικτές» = με τοίχους (εξωτ. πλήρες πάχος, εσωτ. μισό). Βορράς: επάνω.


■ Ισόγειο (μικτό 121,16 m², καθαρό 104,57 m²)

#	Χώρος	Καθ. εμβ. (m²)	Καθ. Α×Β (m)	Μικτές Α×Β (m)	Ζώνη
1	Καθιστικό	21,05	4,80×4,38	5,15×4,73	κύρια
2	Σαλόνι	18,47	4,21×4,38	4,31×4,73	κύρια
3	Κουζίνα	13,96	3,18×4,38	3,53×4,73	κύρια
4	Κύριο Υπνοδωμάτιο	11,02	3,63×3,04	3,98×3,39	κύρια
5	Υπνοδωμάτιο 2	9,28	3,06×3,04	3,16×3,39	κύρια
6	Υπνοδωμάτιο 3	9,28	3,06×3,04	3,16×3,39	κύρια
7	Λουτρό	2,19	1,28×1,72	1,38×1,82	βοηθ.
8	Αποθήκη	1,68	0,98×1,72	1,33×1,82	βοηθ.
9	Χωλ	1,68	1,37×1,22	1,47×1,57	βοηθ.
10	WC	1,08	0,88×1,22	1,23×1,57	βοηθ.
11	Διάδρομος	14,88	12,40×1,20	13,00×1,30	βοηθ.

Έλεγχος φωτισμού & αερισμού (Κ.Κ. αρ. 20 §5.1.2 / αρ. 21 §5.2)

Χώρος	Εμβ.	Φως≥10%	Υαλοπ.	Αερ.≥5%	Ανοιγ.	Φως	Αερ.
Καθιστικό	21,1	2,11	2,11	1,05	1,05	✓	✓
Σαλόνι	18,5	1,85	1,85	0,92	0,92	✓	✓
Κουζίνα	14,0	1,40	1,40	0,70	0,70	✓	✓
Κύριο Υπνοδωμάτιο	11,0	1,10	1,26	0,55	0,63	✓	✓
Υπνοδωμάτιο 2	9,3	0,93	1,26	0,46	0,63	✓	✓
Υπνοδωμάτιο 3	9,3	0,93	1,26	0,46	0,63	✓	✓
Λουτρό	2,2	0,22	0,00	0,11	0,00	✓	✓
Αποθήκη	1,7	0,17	0,00	0,08	0,00	✓	✓
Χωλ	1,7	0,17	0,00	0,08	0,00	✓	✓
WC	1,1	0,11	0,00	0,05	0,00	✓	✗

→ Όλοι οι χώροι κύριας χρήσης πληρούν φωτισμό ≥10% & αερισμό ≥5%.

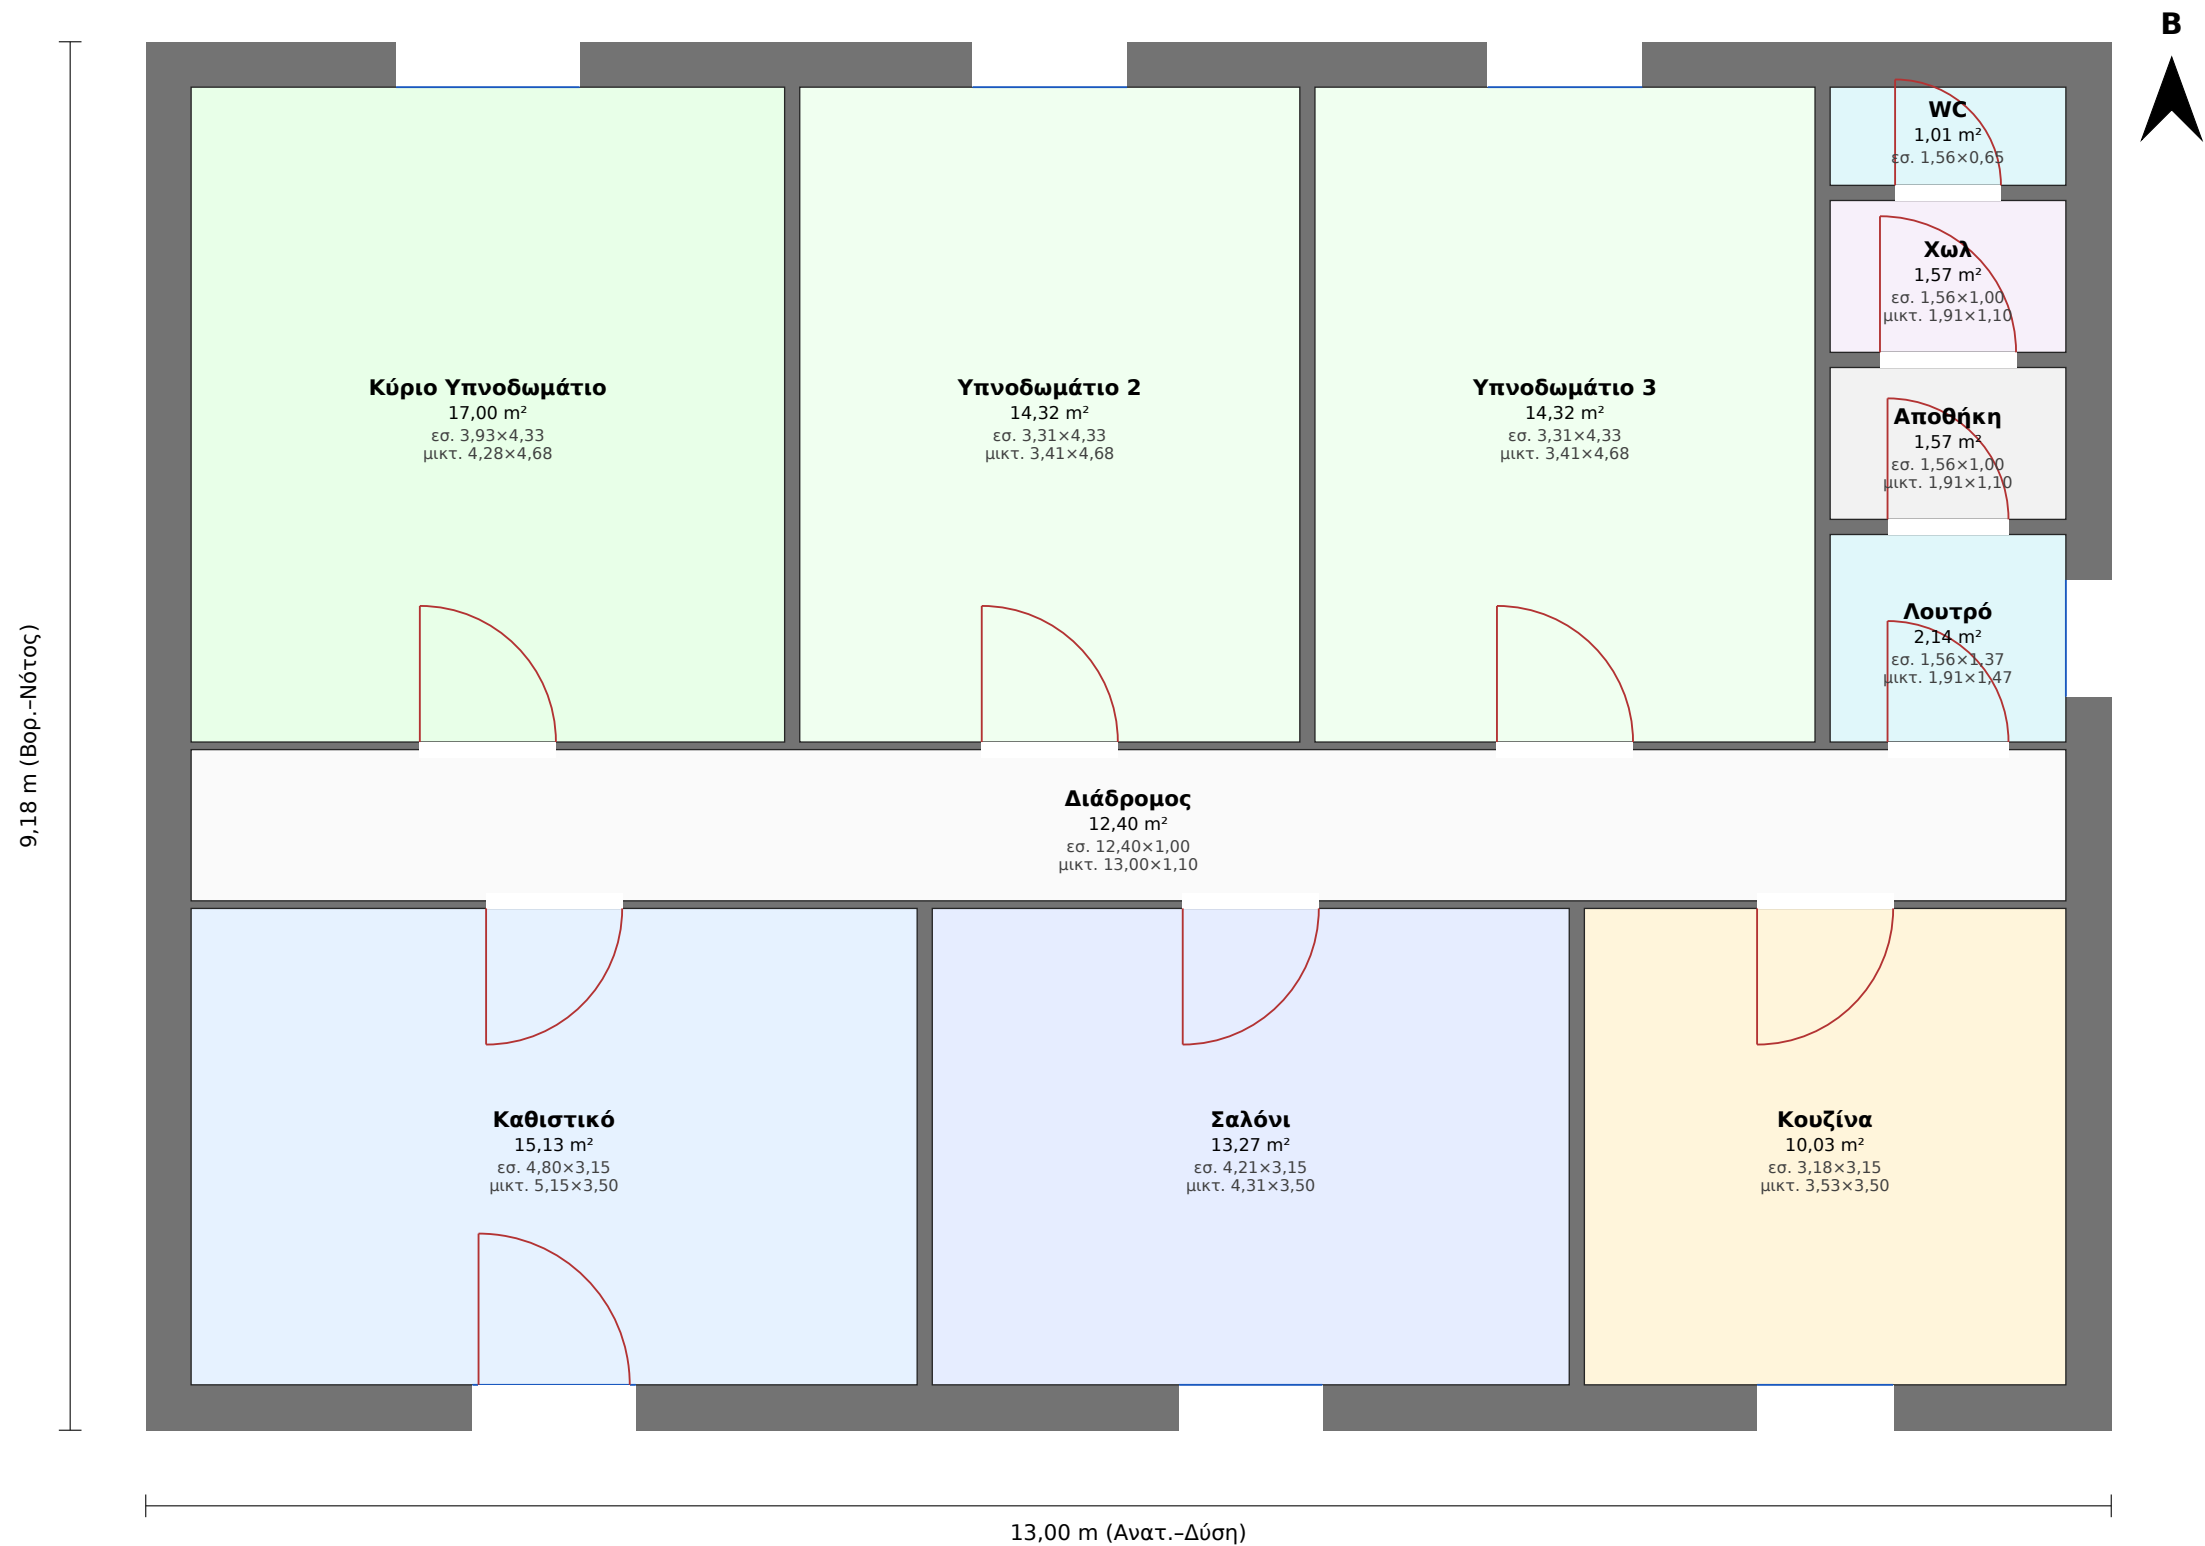

Τεχνικό Γραφείο Μελετών — Γεωργακόπουλος Χρ. / Φουντάς Αθ.
Έργο: Μονοκατοικία Αμαλιάδας
Πρόταση 3 — Ισόγειο
Κλίμακα 1:50 · Μικτό εμβ.: 119,34 m²
Είσοδος: Νότος · Αμαλιάδα, Π.Ε. Ηλείας
Ημερομηνία: 15.08.2026 · Σχεδ.: Γεωργακόπουλος Χρ. (ΑΜ ΤΕΕ 101893)

Μονοκατοικία Αμαλιάδας — Πρόταση 3: Πίνακες χώρων & έλεγχοι

Διαστάσεις: «καθαρές» = εσωτερικές ελεύθερες · «μικτές» = με τοίχους (εξωτ. πλήρες πάχος, εσωτ. μισό). Βορράς: επάνω.

■ Ισόγειο (μικτό 119,34 m², καθαρό 102,76 m²)

#	Χώρος	Καθ. εμβ. (m²)	Καθ. Α×Β (m)	Μικτές Α×Β (m)	Ζώνη
1	Καθιστικό	15,13	4,80×3,15	5,15×3,50	κύρια
2	Σαλόνι	13,27	4,21×3,15	4,31×3,50	κύρια
3	Κουζίνα	10,03	3,18×3,15	3,53×3,50	κύρια
4	Κύριο Υπνοδωμάτιο	17,00	3,93×4,33	4,28×4,68	κύρια
5	Υπνοδωμάτιο 2	14,32	3,31×4,33	3,41×4,68	κύρια
6	Υπνοδωμάτιο 3	14,32	3,31×4,33	3,41×4,68	κύρια
7	Λουτρό	2,14	1,56×1,37	1,91×1,47	βοηθ.
8	Αποθήκη	1,57	1,56×1,00	1,91×1,10	βοηθ.
9	Χωλ	1,57	1,56×1,00	1,91×1,10	βοηθ.
10	WC	1,01	1,56×0,65	1,91×1,00	βοηθ.
11	Διάδρομος	12,40	12,40×1,00	13,00×1,10	βοηθ.

Έλεγχος φωτισμού & αερισμού (Κ.Κ. αρ. 20 §5.1.2 / αρ. 21 §5.2)

Χώρος	Εμβ.	Φως≥10%	Υαλοπ.	Αερ.≥5%	Ανοιγ.	Φως	Αερ.
Καθιστικό	15,1	1,51	1,51	0,76	0,76	✓	✓
Σαλόνι	13,3	1,33	1,33	0,66	0,66	✓	✓
Κουζίνα	10,0	1,00	1,26	0,50	0,63	✓	✓
Κύριο Υπνοδωμάτιο	17,0	1,70	1,70	0,85	0,85	✓	✓
Υπνοδωμάτιο 2	14,3	1,43	1,43	0,72	0,72	✓	✓
Υπνοδωμάτιο 3	14,3	1,43	1,43	0,72	0,72	✓	✓
Λουτρό	2,1	0,21	1,08	0,11	0,54	✓	✓
Αποθήκη	1,6	0,16	0,00	0,08	0,00	✓	✓
Χωλ	1,6	0,16	0,00	0,08	0,00	✓	✓
WC	1,0	0,10	0,00	0,05	0,00	✓	✗

→ Όλοι οι χώροι κύριας χρήσης πληρούν φωτισμό ≥10% & αερισμό ≥5%.