


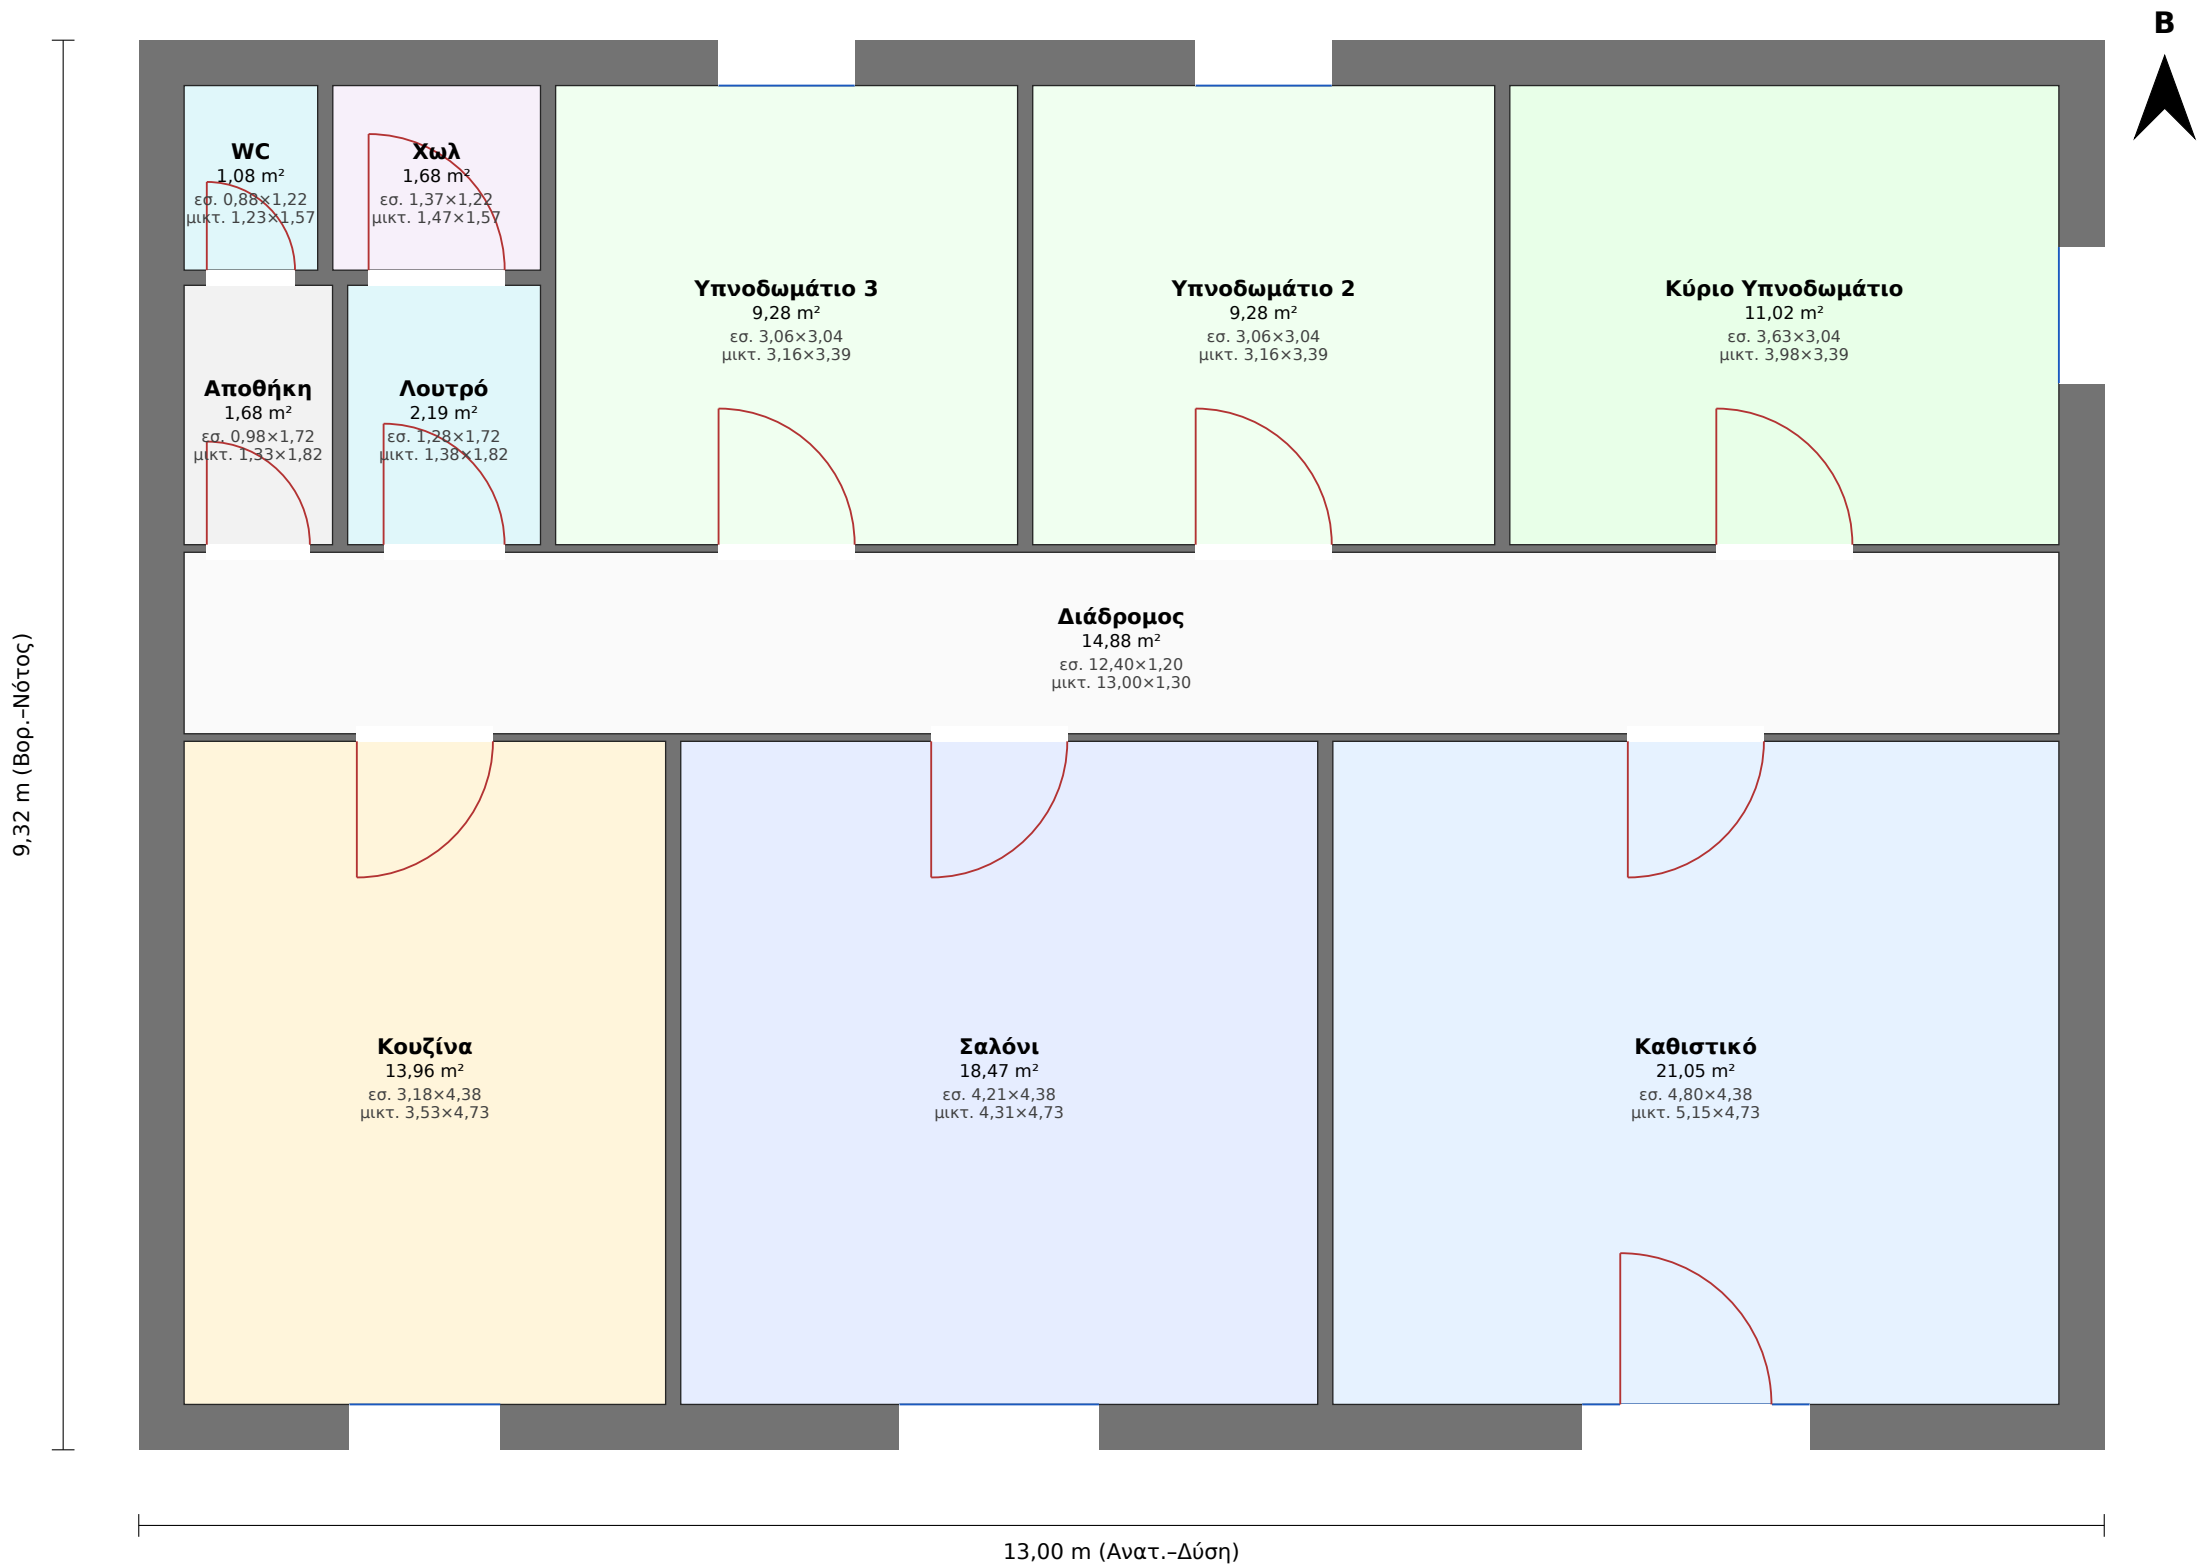

Κλίμακα 1:50



Τεχνικό Γραφείο Μελετών — Γεωργακόπουλος Χρ. / Φουντάς Αθ.
Έργο: Μονοκατοικία Αμαλιάδας
Πρόταση 2 — Ισόγειο
Κλίμακα 1:50 · Μικτό εμβ.: 121,16 m²
Είσοδος: Νότος · Αμαλιάδα, Π.Ε. Ηλείας
Ημερομηνία: 15.08.2026 · Σχεδ.: Γεωργακόπουλος Χρ. (AM TEE 101893)

Μονοκατοικία Αμαλιάδας — Πρόταση 2: Πίνακες χώρων & έλεγχοι

Διαστάσεις: «καθαρές» = εσωτερικές ελεύθερες · «μικτές» = με τοίχους (εξωτ. πλήρες πάχος, εσωτ. μισό). Βορράς: επάνω.

■ Ισόγειο (μικτό 121,16 m², καθαρό 104,57 m²)

#	Χώρος	Καθ. εμβ. (m²)	Καθ. Α×Β (m)	Μικτές Α×Β (m)	Ζώνη
1	Καθιστικό	21,05	4,80×4,38	5,15×4,73	κύρια
2	Σαλόνι	18,47	4,21×4,38	4,31×4,73	κύρια
3	Κουζίνα	13,96	3,18×4,38	3,53×4,73	κύρια
4	Κύριο Υπνοδωμάτιο	11,02	3,63×3,04	3,98×3,39	κύρια
5	Υπνοδωμάτιο 2	9,28	3,06×3,04	3,16×3,39	κύρια
6	Υπνοδωμάτιο 3	9,28	3,06×3,04	3,16×3,39	κύρια
7	Λουτρό	2,19	1,28×1,72	1,38×1,82	βοηθ.
8	Αποθήκη	1,68	0,98×1,72	1,33×1,82	βοηθ.
9	Χωλ	1,68	1,37×1,22	1,47×1,57	βοηθ.
10	WC	1,08	0,88×1,22	1,23×1,57	βοηθ.
11	Διάδρομος	14,88	12,40×1,20	13,00×1,30	βοηθ.

Έλεγχος φωτισμού & αερισμού (Κ.Κ. αρ. 20 §5.1.2 / αρ. 21 §5.2)

Χώρος	Εμβ.	Φως≥10%	Υαλοπ.	Αερ.≥5%	Ανοιγ.	Φως	Αερ.
Καθιστικό	21,1	2,11	2,11	1,05	1,05	✓	✓
Σαλόνι	18,5	1,85	1,85	0,92	0,92	✓	✓
Κουζίνα	14,0	1,40	1,40	0,70	0,70	✓	✓
Κύριο Υπνοδωμάτιο	11,0	1,10	1,26	0,55	0,63	✓	✓
Υπνοδωμάτιο 2	9,3	0,93	1,26	0,46	0,63	✓	✓
Υπνοδωμάτιο 3	9,3	0,93	1,26	0,46	0,63	✓	✓
Λουτρό	2,2	0,22	0,00	0,11	0,00	✓	✓
Αποθήκη	1,7	0,17	0,00	0,08	0,00	✓	✓
Χωλ	1,7	0,17	0,00	0,08	0,00	✓	✓
WC	1,1	0,11	0,00	0,05	0,00	✓	✗

→ Όλοι οι χώροι κύριας χρήσης πληρούν φωτισμό ≥10% & αερισμό ≥5%.