


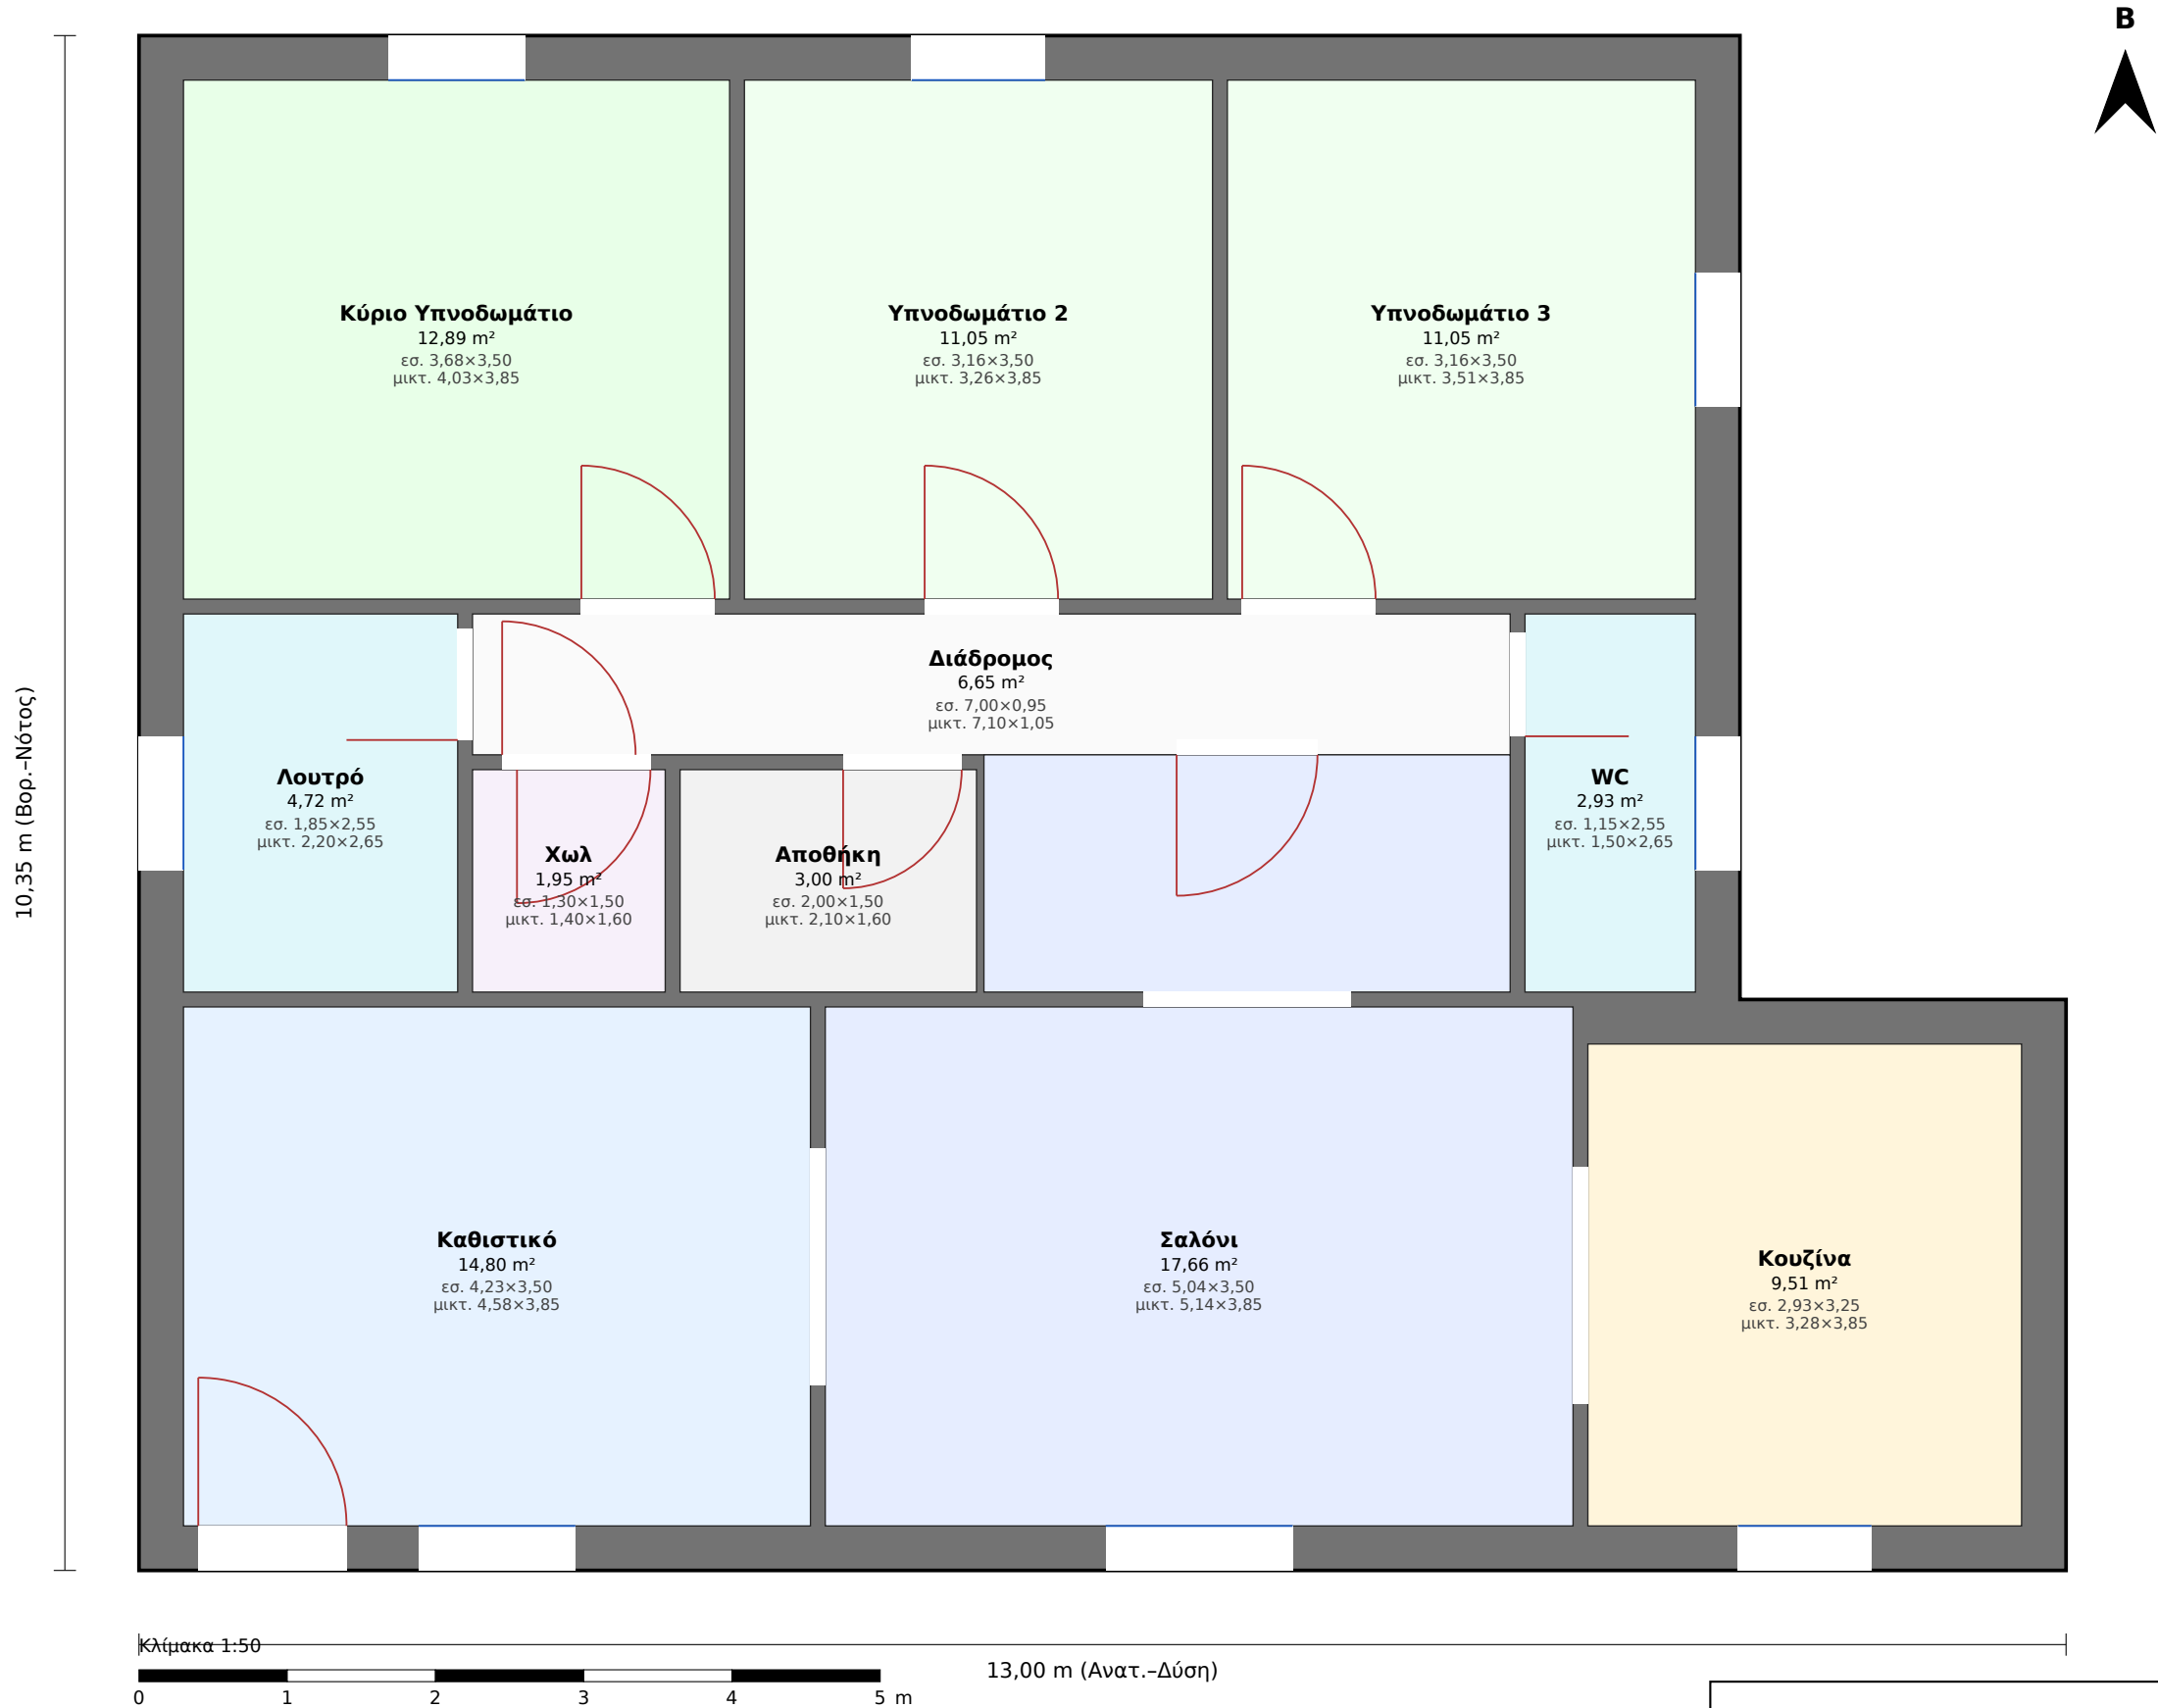

Τεχνικό Γραφείο Μελετών — Γεωργακόπουλος Χρ. / Φουντάς Αθ.
Έργο: Μονοκατοικία Αμαλιάδας
Πρόταση 1 — Ισόγειο
Κλίμακα 1:50 · Μικτό εμβ.: 120,25 m²
Είσοδος: Νότος · Αμαλιάδα, Π.Ε. Ηλείας
Ημερομηνία: 28.08.2026 · Σχεδ.: Γεωργακόπουλος Χρ. (AM TEE 101893)

Μονοκατοικία Αμαλιάδας — Πρόταση 1: Πίνακες χώρων & έλεγχοι

Διαστάσεις: «καθαρές» = εσωτερικές ελεύθερες · «μικτές» = με τοίχους (εξωτ. πλήρες πάχος, εσωτ. μισό). Βορράς: επάνω.

■ Ισόγειο (μικτό 120,25 m², καθαρό 101,90 m²)

#	Χώρος	Καθ. εμβ. (m²)	Καθ. Α×Β (m)	Μικτές Α×Β (m)	Ζώνη
1	Καθιστικό	14,80	4,23×3,50	4,58×3,85	κύρια
2	Σαλόνι	17,66	5,04×3,50	5,14×3,85	κύρια
3	Κουζίνα	9,51	2,93×3,25	3,28×3,85	κύρια
4	Κύριο Υπνοδωμάτιο	12,89	3,68×3,50	4,03×3,85	κύρια
5	Υπνοδωμάτιο 2	11,05	3,16×3,50	3,26×3,85	κύρια
6	Υπνοδωμάτιο 3	11,05	3,16×3,50	3,51×3,85	κύρια
7	Λουτρό	4,72	1,85×2,55	2,20×2,65	βοηθ.
8	Χωλ	1,95	1,30×1,50	1,40×1,60	βοηθ.
9	Αποθήκη	3,00	2,00×1,50	2,10×1,60	βοηθ.
10	WC	2,93	1,15×2,55	1,50×2,65	βοηθ.
11	Διάδρομος	6,65	7,00×0,95	7,10×1,05	βοηθ.
12		5,68	3,55×1,60	3,65×1,70	κύρια

Έλεγχος φωτισμού & αερισμού (Κ.Κ. αρ. 20 §5.1.2 / αρ. 21 §5.2)

Χώρος	Εμβ.	Φως≥10%	Υαλοπ.	Αερ.≥5%	Ανοιγ.	Φως	Αερ.
Καθιστικό	14,8	1,48	1,48	0,74	0,74	✓	✓
Σαλόνι	17,7	1,77	1,77	0,88	0,88	✓	✓
Κουζίνα	9,5	0,95	1,26	0,48	0,63	✓	✓
Κύριο Υπνοδωμάτιο	12,9	1,29	1,29	0,64	0,64	✓	✓
Υπνοδωμάτιο 2	11,1	1,11	1,26	0,55	0,63	✓	✓
Υπνοδωμάτιο 3	11,1	1,11	1,26	0,55	0,63	✓	✓
Λουτρό	4,7	0,47	1,26	0,24	0,63	✓	✓
Χωλ	2,0	0,20	0,00	0,10	0,00	✓	✓
Αποθήκη	3,0	0,30	0,00	0,15	0,00	✓	✓
WC	2,9	0,29	1,26	0,15	0,63	✓	✓
	5,7	0,57	0,00	0,28	0,00	✗	✗

→ 1 χώρος/οι κύριας χρήσης χρειάζονται μεγαλύτερο άνοιγμα.