


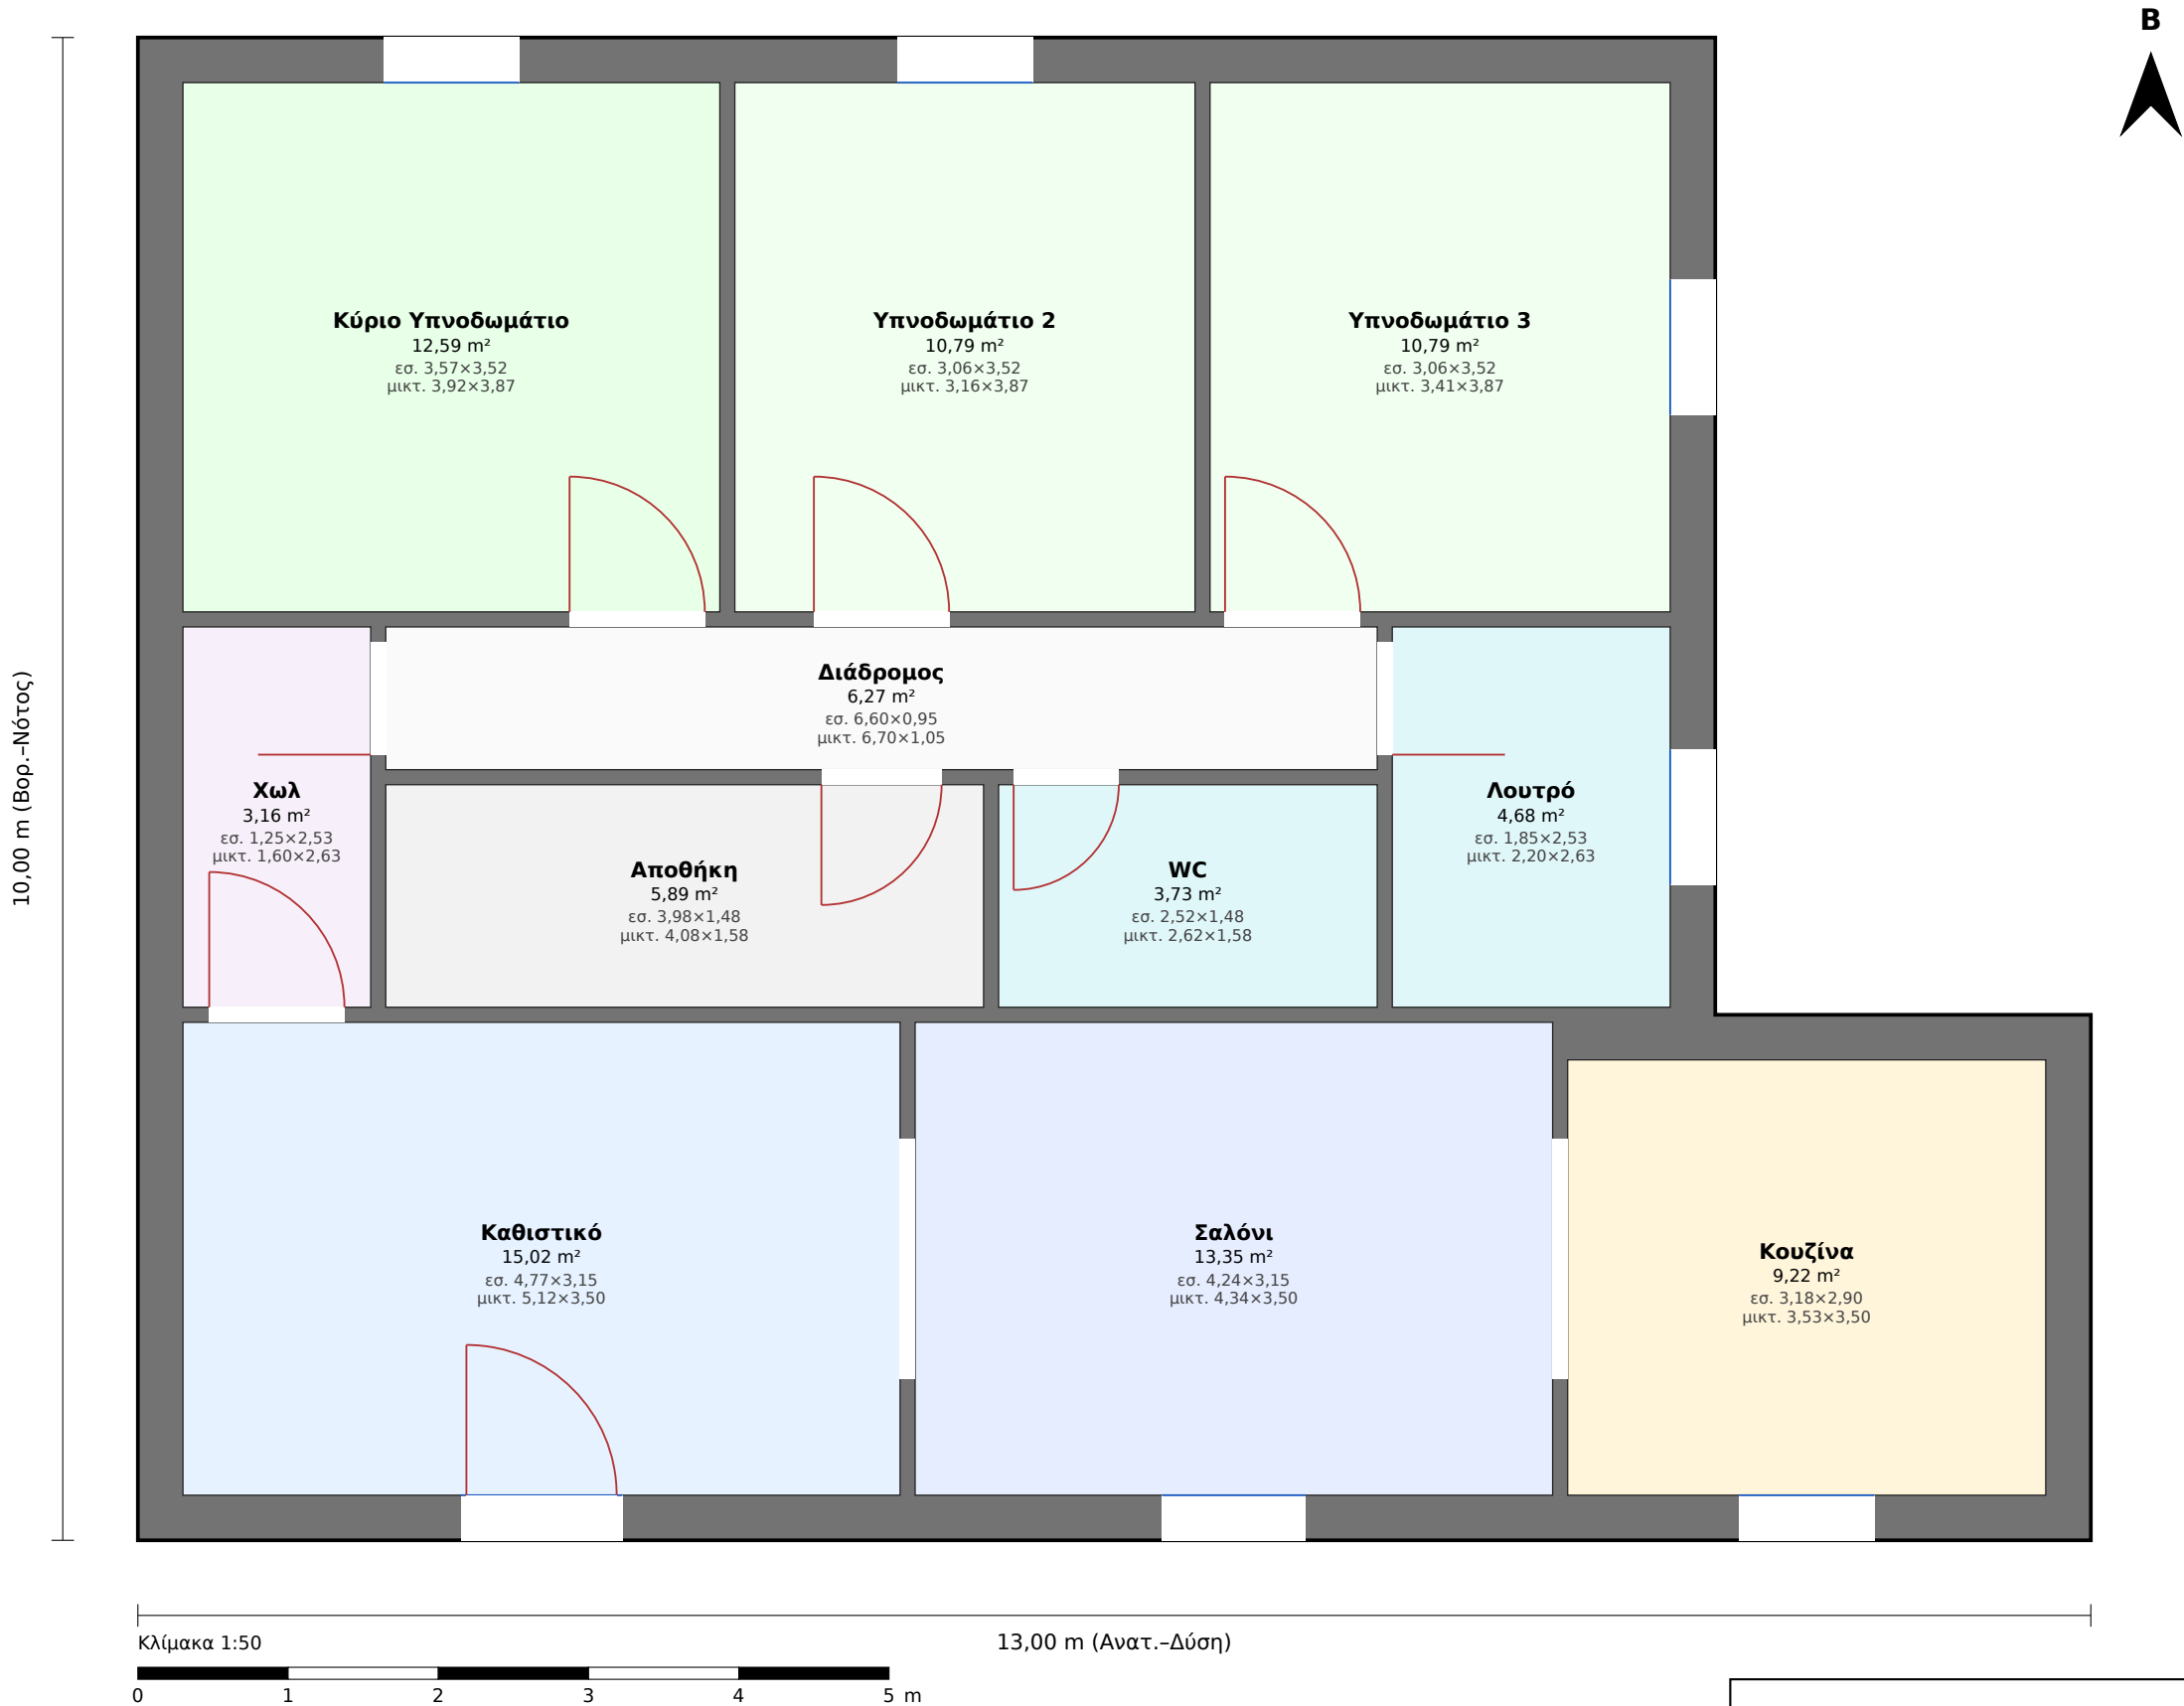

**Τεχνικό Γραφείο Μελετών — Γεωργακόπουλος Χρ. / Φουντάς Αθ.**  
Έργο: Μονοκατοικία Αμαλιάδας  
Πρόταση 1 — Ισόγειο  
Κλίμακα 1:50 · Μικτό εμβ.: 113,74 m<sup>2</sup>  
Είσοδος: Νότος · Αμαλιάδα, Π.Ε. Ηλείας  
Ημερομηνία: 15.08.2026 · Σχεδ.: Γεωργακόπουλος Χρ. (AM TEE 101893)

# Μονοκατοικία Αμαλιάδας — Πρόταση 1: Πίνακες χώρων & έλεγχοι

Διαστάσεις: «καθαρές» = εσωτερικές ελεύθερες · «μικτές» = με τοίχους (εξωτ. πλήρες πάχος, εσωτ. μισό). Βορράς: επάνω.


■ **Ισόγειο (μικτό 113,74 m², καθαρό 95,50 m²)**

| #  | Χώρος             | Καθ. εμβ. (m²) | Καθ. Α×Β (m) | Μικτές Α×Β (m) | Ζώνη  |
|----|-------------------|----------------|--------------|----------------|-------|
| 1  | Καθιστικό         | 15,02          | 4,77×3,15    | 5,12×3,50      | κύρια |
| 2  | Σαλόνι            | 13,35          | 4,24×3,15    | 4,34×3,50      | κύρια |
| 3  | Κουζίνα           | 9,22           | 3,18×2,90    | 3,53×3,50      | κύρια |
| 4  | Κύριο Υπνοδωμάτιο | 12,59          | 3,57×3,52    | 3,92×3,87      | κύρια |
| 5  | Υπνοδωμάτιο 2     | 10,79          | 3,06×3,52    | 3,16×3,87      | κύρια |
| 6  | Υπνοδωμάτιο 3     | 10,79          | 3,06×3,52    | 3,41×3,87      | κύρια |
| 7  | Χωλ               | 3,16           | 1,25×2,53    | 1,60×2,63      | βοηθ. |
| 8  | Αποθήκη           | 5,89           | 3,98×1,48    | 4,08×1,58      | βοηθ. |
| 9  | WC                | 3,73           | 2,52×1,48    | 2,62×1,58      | βοηθ. |
| 10 | Λουτρό            | 4,68           | 1,85×2,53    | 2,20×2,63      | βοηθ. |
| 11 | Διάδρομος         | 6,27           | 6,60×0,95    | 6,70×1,05      | βοηθ. |

## Έλεγχος φωτισμού & αερισμού (Κ.Κ. αρ. 20 §5.1.2 / αρ. 21 §5.2)

| Χώρος             | Εμβ. | Φως≥10% | Υαλοπ. | Αερ.≥5% | Ανοιγ. | Φως | Αερ. |
|-------------------|------|---------|--------|---------|--------|-----|------|
| Καθιστικό         | 15,0 | 1,50    | 1,50   | 0,75    | 0,75   | ✓   | ✓    |
| Σαλόνι            | 13,4 | 1,34    | 1,34   | 0,67    | 0,67   | ✓   | ✓    |
| Κουζίνα           | 9,2  | 0,92    | 1,26   | 0,46    | 0,63   | ✓   | ✓    |
| Κύριο Υπνοδωμάτιο | 12,6 | 1,26    | 1,26   | 0,63    | 0,63   | ✓   | ✓    |
| Υπνοδωμάτιο 2     | 10,8 | 1,08    | 1,26   | 0,54    | 0,63   | ✓   | ✓    |
| Υπνοδωμάτιο 3     | 10,8 | 1,08    | 1,26   | 0,54    | 0,63   | ✓   | ✓    |
| Χωλ               | 3,2  | 0,32    | 0,00   | 0,16    | 0,00   | ✓   | ✓    |
| Αποθήκη           | 5,9  | 0,59    | 0,00   | 0,29    | 0,00   | ✓   | ✓    |
| WC                | 3,7  | 0,37    | 0,00   | 0,19    | 0,00   | ✓   | ✓    |
| Λουτρό            | 4,7  | 0,47    | 1,26   | 0,23    | 0,63   | ✓   | ✓    |

→ Όλοι οι χώροι κύριας χρήσης πληρούν φωτισμό ≥10% & αερισμό ≥5%.

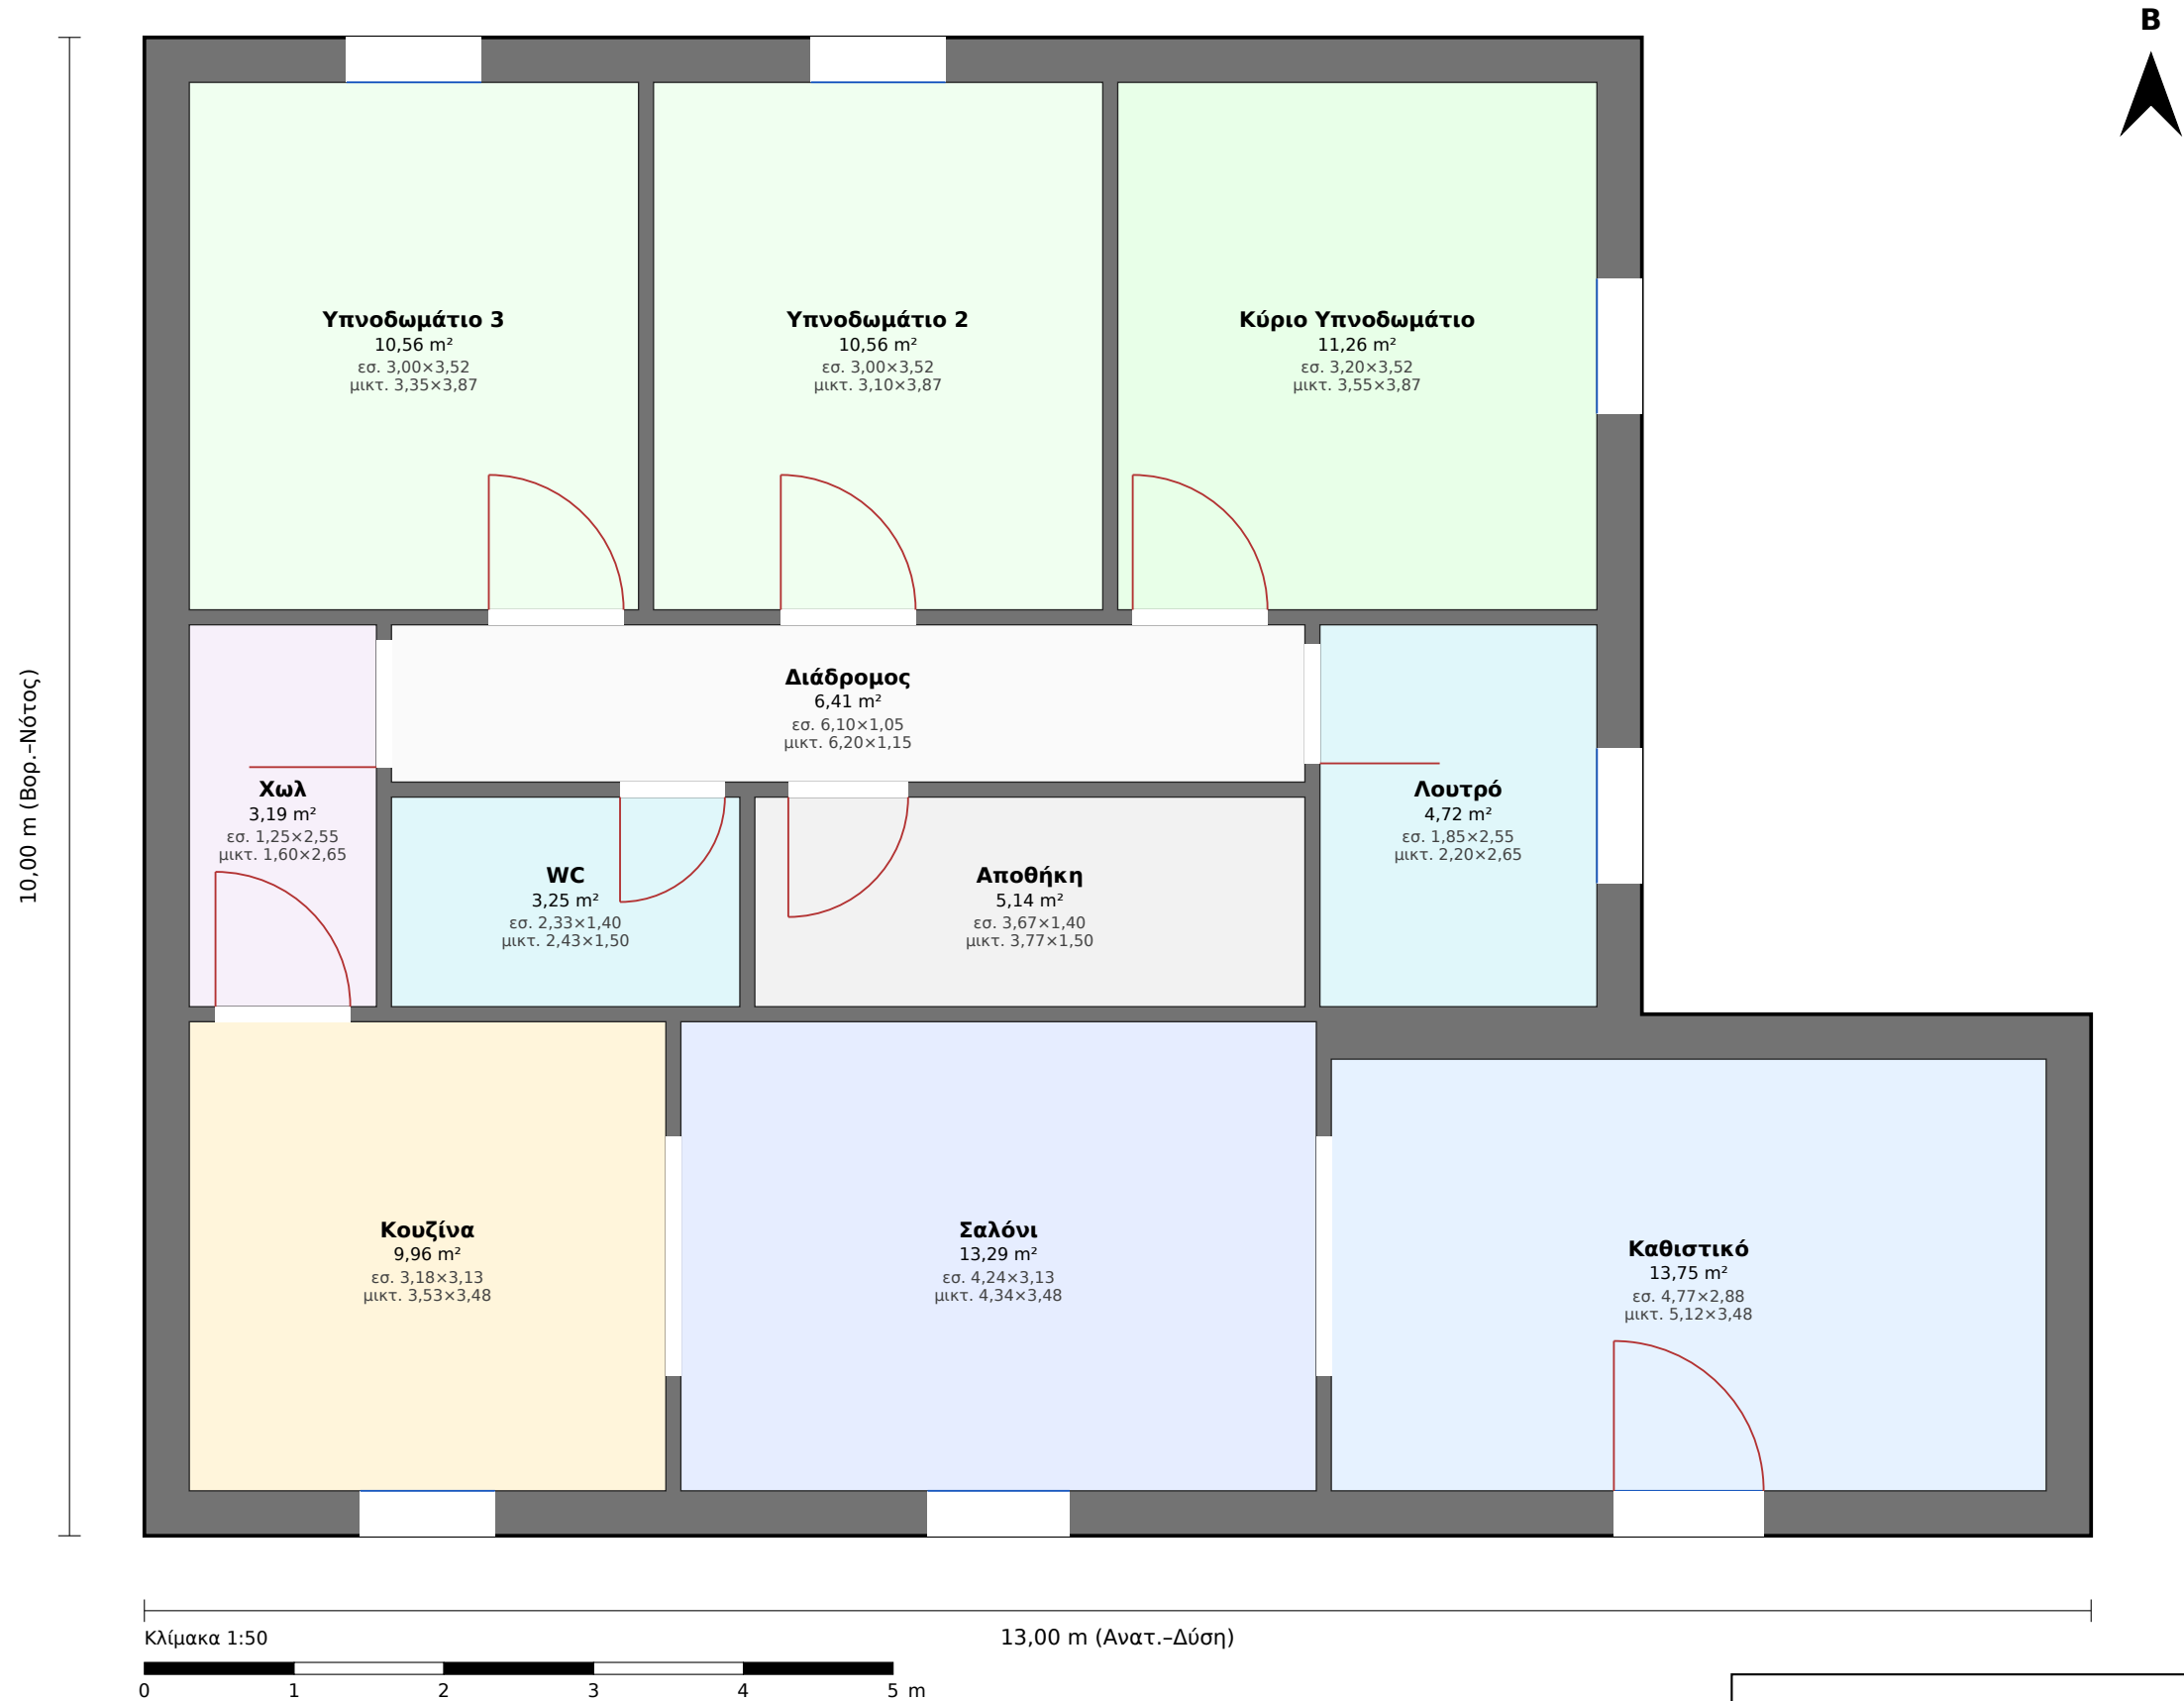

**Τεχνικό Γραφείο Μελετών — Γεωργακόπουλος Χρ. / Φουντάς Αθ.**  
Έργο: Μονοκατοικία Αμαλιάδας  
Πρόταση 2 — Ισόγειο  
Κλίμακα 1:50 · Μικτό εμβ.: 110,44 m<sup>2</sup>  
Είσοδος: Νότος · Αμαλιάδα, Π.Ε. Ηλείας  
Ημερομηνία: 15.08.2026 · Σχεδ.: Γεωργακόπουλος Χρ. (ΑΜ ΤΕΕ 101893)

## Μονοκατοικία Αμαλιάδας — Πρόταση 2: Πίνακες χώρων & έλεγχοι

Διαστάσεις: «καθαρές» = εσωτερικές ελεύθερες · «μικτές» = με τοίχους (εξωτ. πλήρες πάχος, εσωτ. μισό). Βορράς: επάνω.

■ **Ισόγειο (μικτό 110,44 m², καθαρό 92,09 m²)**

| #  | Χώρος             | Καθ. εμβ. (m²) | Καθ. Α×Β (m) | Μικτές Α×Β (m) | Ζώνη  |
|----|-------------------|----------------|--------------|----------------|-------|
| 1  | Κουζίνα           | 9,96           | 3,18×3,13    | 3,53×3,48      | κύρια |
| 2  | Σαλόνι            | 13,29          | 4,24×3,13    | 4,34×3,48      | κύρια |
| 3  | Καθιστικό         | 13,75          | 4,77×2,88    | 5,12×3,48      | κύρια |
| 4  | Υπνοδωμάτιο 3     | 10,56          | 3,00×3,52    | 3,35×3,87      | κύρια |
| 5  | Υπνοδωμάτιο 2     | 10,56          | 3,00×3,52    | 3,10×3,87      | κύρια |
| 6  | Κύριο Υπνοδωμάτιο | 11,26          | 3,20×3,52    | 3,55×3,87      | κύρια |
| 7  | Χωλ               | 3,19           | 1,25×2,55    | 1,60×2,65      | βοηθ. |
| 8  | WC                | 3,25           | 2,33×1,40    | 2,43×1,50      | βοηθ. |
| 9  | Αποθήκη           | 5,14           | 3,67×1,40    | 3,77×1,50      | βοηθ. |
| 10 | Λουτρό            | 4,72           | 1,85×2,55    | 2,20×2,65      | βοηθ. |
| 11 | Διάδρομος         | 6,41           | 6,10×1,05    | 6,20×1,15      | βοηθ. |

### Έλεγχος φωτισμού & αερισμού (Κ.Κ. αρ. 20 §5.1.2 / αρ. 21 §5.2)

| Χώρος             | Εμβ. | Φως≥10% | Υαλοπ. | Αερ.≥5% | Ανοιγ. | Φως | Αερ. |
|-------------------|------|---------|--------|---------|--------|-----|------|
| Κουζίνα           | 10,0 | 1,00    | 1,26   | 0,50    | 0,63   | ✓   | ✓    |
| Σαλόνι            | 13,3 | 1,33    | 1,33   | 0,66    | 0,66   | ✓   | ✓    |
| Καθιστικό         | 13,8 | 1,38    | 1,38   | 0,69    | 0,69   | ✓   | ✓    |
| Υπνοδωμάτιο 3     | 10,6 | 1,06    | 1,26   | 0,53    | 0,63   | ✓   | ✓    |
| Υπνοδωμάτιο 2     | 10,6 | 1,06    | 1,26   | 0,53    | 0,63   | ✓   | ✓    |
| Κύριο Υπνοδωμάτιο | 11,3 | 1,13    | 1,26   | 0,56    | 0,63   | ✓   | ✓    |
| Χωλ               | 3,2  | 0,32    | 0,00   | 0,16    | 0,00   | ✓   | ✓    |
| WC                | 3,3  | 0,33    | 0,00   | 0,16    | 0,00   | ✓   | ✓    |
| Αποθήκη           | 5,1  | 0,51    | 0,00   | 0,26    | 0,00   | ✓   | ✓    |
| Λουτρό            | 4,7  | 0,47    | 1,26   | 0,24    | 0,63   | ✓   | ✓    |

→ Όλοι οι χώροι κύριας χρήσης πληρούν φωτισμό ≥10% & αερισμό ≥5%.



Τεχνικό Γραφείο Μελετών — Γεωργακόπουλος Χρ. / Φουντάς Αθ.  
Έργο: Μονοκατοικία Αμαλιάδας  
Πρόταση 3 — Ισόγειο  
Κλίμακα 1:50 · Μικτό εμβ.: 114,44 m²  
Είσοδος: Νότος · Αμαλιάδα, Π.Ε. Ηλείας  
Ημερομηνία: 15.08.2026 · Σχεδ.: Γεωργακόπουλος Χρ. (AM TEE 101893)

Μονοκατοικία Αμαλιάδας — Πρόταση 3: Πίνακες χώρων & έλεγχοι

Διαστάσεις: «καθαρές» = εσωτερικές ελεύθερες · «μικτές» = με τοίχους (εξωτ. πλήρες πάχος, εσωτ. μισό). Βορράς: επάνω.

■ Ισόγειο (μικτό 114,44 m², καθαρό 96,09 m²)

| #  | Χώρος             | Καθ. εμβ. (m²) | Καθ. Α×Β (m) | Μικτές Α×Β (m) | Ζώνη  |
|----|-------------------|----------------|--------------|----------------|-------|
| 1  | Καθιστικό         | 14,38          | 4,77×3,01    | 5,12×3,36      | κύρια |
| 2  | Σαλόνι            | 12,78          | 4,24×3,01    | 4,34×3,36      | κύρια |
| 3  | Κουζίνα           | 8,79           | 3,18×2,76    | 3,53×3,36      | κύρια |
| 4  | Κύριο Υπνοδωμάτιο | 12,68          | 3,77×3,37    | 4,12×3,72      | κύρια |
| 5  | Υπνοδωμάτιο 2     | 10,87          | 3,23×3,37    | 3,33×3,72      | κύρια |
| 6  | Υπνοδωμάτιο 3     | 10,87          | 3,23×3,37    | 3,58×3,72      | κύρια |
| 7  | Χωλ               | 3,25           | 1,25×2,60    | 1,60×2,70      | βοηθ. |
| 8  | Αποθήκη           | 6,45           | 4,30×1,50    | 4,40×1,60      | βοηθ. |
| 9  | WC                | 4,09           | 2,72×1,50    | 2,82×1,60      | βοηθ. |
| 10 | Λουτρό            | 4,81           | 1,85×2,60    | 2,20×2,70      | βοηθ. |
| 11 | Διάδρομος         | 7,12           | 7,12×1,00    | 7,22×1,10      | βοηθ. |

Έλεγχος φωτισμού & αερισμού (Κ.Κ. αρ. 20 §5.1.2 / αρ. 21 §5.2)

| Χώρος             | Εμβ. | Φως≥10% | Υαλοπ. | Αερ.≥5% | Ανοιγ. | Φως | Αερ. |
|-------------------|------|---------|--------|---------|--------|-----|------|
| Καθιστικό         | 14,4 | 1,44    | 1,44   | 0,72    | 0,72   | ✓   | ✓    |
| Σαλόνι            | 12,8 | 1,28    | 1,28   | 0,64    | 0,64   | ✓   | ✓    |
| Κουζίνα           | 8,8  | 0,88    | 1,26   | 0,44    | 0,63   | ✓   | ✓    |
| Κύριο Υπνοδωμάτιο | 12,7 | 1,27    | 1,27   | 0,63    | 0,63   | ✓   | ✓    |
| Υπνοδωμάτιο 2     | 10,9 | 1,09    | 1,26   | 0,54    | 0,63   | ✓   | ✓    |
| Υπνοδωμάτιο 3     | 10,9 | 1,09    | 1,26   | 0,54    | 0,63   | ✓   | ✓    |
| Χωλ               | 3,2  | 0,32    | 0,00   | 0,16    | 0,00   | ✓   | ✓    |
| Αποθήκη           | 6,5  | 0,65    | 0,00   | 0,32    | 0,00   | ✓   | ✓    |
| WC                | 4,1  | 0,41    | 0,00   | 0,20    | 0,00   | ✓   | ✓    |
| Λουτρό            | 4,8  | 0,48    | 1,26   | 0,24    | 0,63   | ✓   | ✓    |

→ Όλοι οι χώροι κύριας χρήσης πληρούν φωτισμό ≥10% & αερισμό ≥5%.