


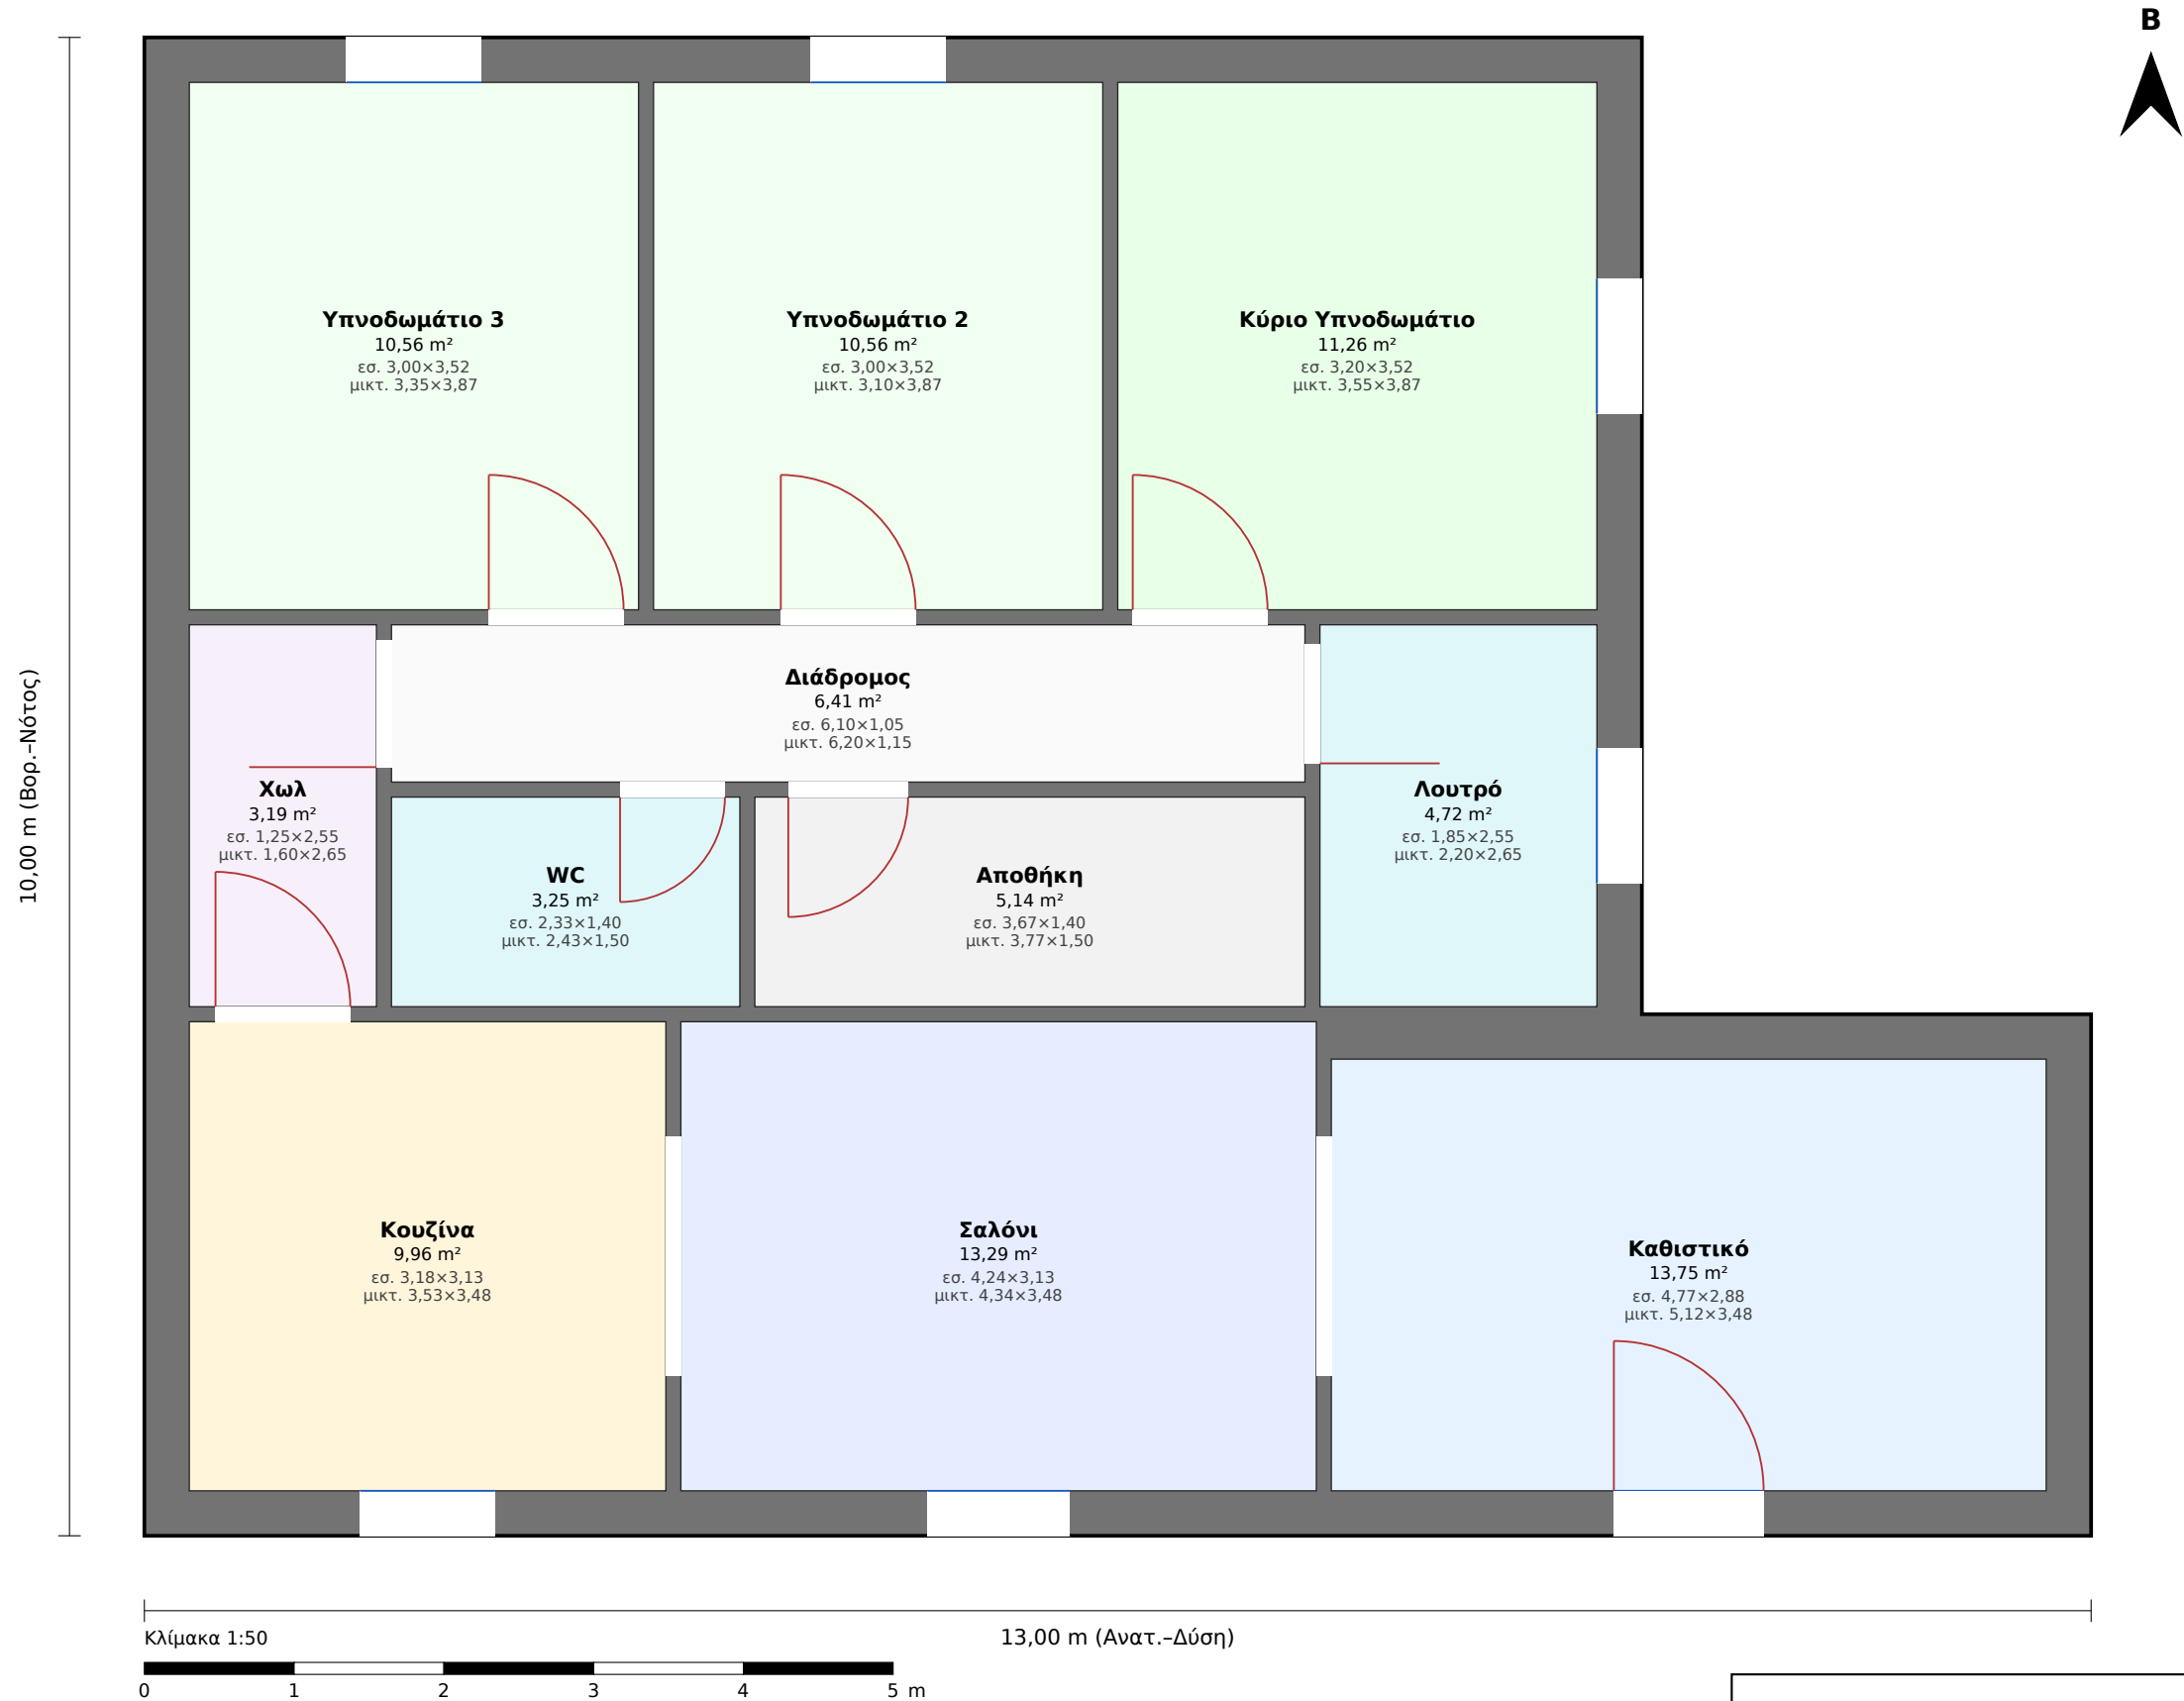

Τεχνικό Γραφείο Μελετών — Γεωργακόπουλος Χρ. / Φουντάς Αθ.
Έργο: Μονοκατοικία Αμαλιάδας
Πρόταση 2 — Ισόγειο
Κλίμακα 1:50 · Μικτό εμβ.: 110,44 m²
Είσοδος: Νότος · Αμαλιάδα, Π.Ε. Ηλείας
Ημερομηνία: 15.08.2026 · Σχεδ.: Γεωργακόπουλος Χρ. (ΑΜ ΤΕΕ 101893)

Μονοκατοικία Αμαλιάδας — Πρόταση 2: Πίνακες χώρων & έλεγχοι

Διαστάσεις: «καθαρές» = εσωτερικές ελεύθερες · «μικτές» = με τοίχους (εξωτ. πλήρες πάχος, εσωτ. μισό). Βορράς: επάνω.

■ **Ισόγειο (μικτό 110,44 m², καθαρό 92,09 m²)**

#	Χώρος	Καθ. εμβ. (m²)	Καθ. Α×Β (m)	Μικτές Α×Β (m)	Ζώνη
1	Κουζίνα	9,96	3,18×3,13	3,53×3,48	κύρια
2	Σαλόνι	13,29	4,24×3,13	4,34×3,48	κύρια
3	Καθιστικό	13,75	4,77×2,88	5,12×3,48	κύρια
4	Υπνοδωμάτιο 3	10,56	3,00×3,52	3,35×3,87	κύρια
5	Υπνοδωμάτιο 2	10,56	3,00×3,52	3,10×3,87	κύρια
6	Κύριο Υπνοδωμάτιο	11,26	3,20×3,52	3,55×3,87	κύρια
7	Χωλ	3,19	1,25×2,55	1,60×2,65	βοηθ.
8	WC	3,25	2,33×1,40	2,43×1,50	βοηθ.
9	Αποθήκη	5,14	3,67×1,40	3,77×1,50	βοηθ.
10	Λουτρό	4,72	1,85×2,55	2,20×2,65	βοηθ.
11	Διάδρομος	6,41	6,10×1,05	6,20×1,15	βοηθ.

Έλεγχος φωτισμού & αερισμού (Κ.Κ. αρ. 20 §5.1.2 / αρ. 21 §5.2)

Χώρος	Εμβ.	Φως≥10%	Υαλοπ.	Αερ.≥5%	Ανοιγ.	Φως	Αερ.
Κουζίνα	10,0	1,00	1,26	0,50	0,63	✓	✓
Σαλόνι	13,3	1,33	1,33	0,66	0,66	✓	✓
Καθιστικό	13,8	1,38	1,38	0,69	0,69	✓	✓
Υπνοδωμάτιο 3	10,6	1,06	1,26	0,53	0,63	✓	✓
Υπνοδωμάτιο 2	10,6	1,06	1,26	0,53	0,63	✓	✓
Κύριο Υπνοδωμάτιο	11,3	1,13	1,26	0,56	0,63	✓	✓
Χωλ	3,2	0,32	0,00	0,16	0,00	✓	✓
WC	3,3	0,33	0,00	0,16	0,00	✓	✓
Αποθήκη	5,1	0,51	0,00	0,26	0,00	✓	✓
Λουτρό	4,7	0,47	1,26	0,24	0,63	✓	✓

→ Όλοι οι χώροι κύριας χρήσης πληρούν φωτισμό ≥10% & αερισμό ≥5%.